

SYMBOLS AND ABBREVIATIONS

70-60

Speed sign- Passenger and Freight (Ord. #)
Eastern District only.
City Ordinance speed restrictions are applicable
approaching first public crossing and until engine has
covered last public crossing within corporate limits.

Y Yard limit

Southern Pacific Pipelines Inc. within S.P.T. Co. right of way.

Spring switches

L = 3857'

Length of siding between fouling points in feet.

RAIL

S.H. Secondhand Rail
CWR Continuous Welded Rail
W Welded Rail 76' new or 72' secondhand
C.M. Curve Master Rail 39' long
I.M. Inter Manganese Rail 39' long
F.H. Flame Hardened Rail
..... Speno Ground

DETECTORS

Y Hot Box
A Dragging Equipment
X Wide Load
+ High Water

Note: The following abbreviations and symbols will be
made commencing Jan. 1976:

78'HS, 78'72' replaced by 'W'
HS, HSR replaced by 'CWR'
..... replaced by 'A'

RULING GRADES - PERCENT -----
MAXIMUM SPEED RESTRICTIONS (miles per hour) -----
PASSENGER AND FREIGHT - EASTWARD and
WESTWARD OR WESTWARD ONLY

WESTWARD

DATE: Retied and type of ballast -----

RAIL: Year laid -----
Weight -----

CURVATURE -----

EASTWARD
AND
SINGLE

DATE: Retied and type of ballast -----

RAIL: Year laid -----
Weight -----

CURVATURE -----


MAXIMUM SPEED RESTRICTIONS (miles per hour) -----
PASSENGER AND FREIGHT - EASTWARD ONLY -----
MAXIMUM GRADE - PERCENT EASTWARD AND WESTWARD -----
ROADMASTER AND ROADMASTER'S DISTRICT -----

Centralized Traffic Control -----

20' 25' 50-40' 60-40'


0.188 W. 0.302 E.

300

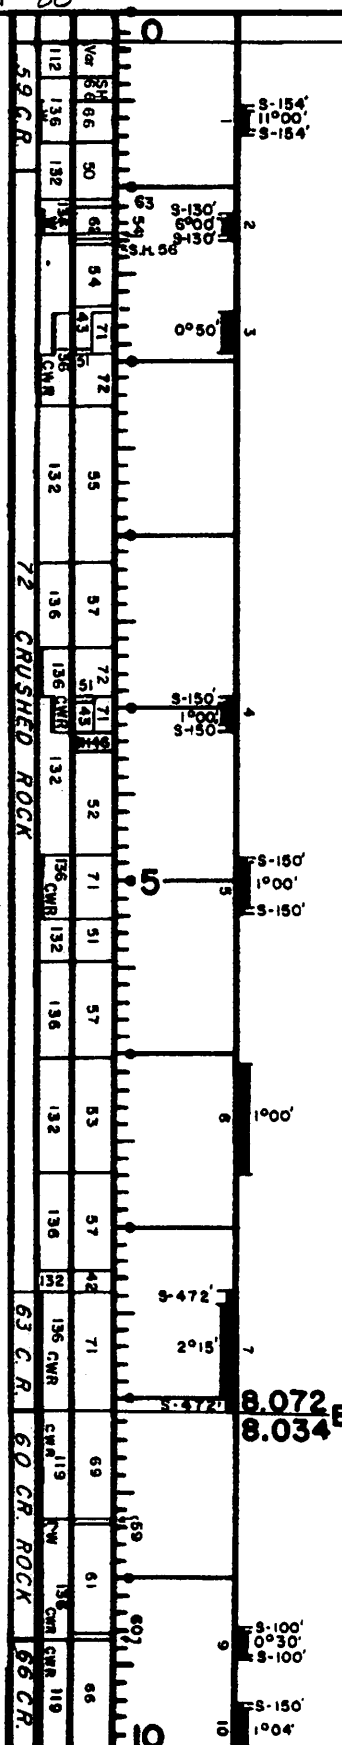

REVISED TO: 1-1-80




6.3 IN DOUBLE TRACK

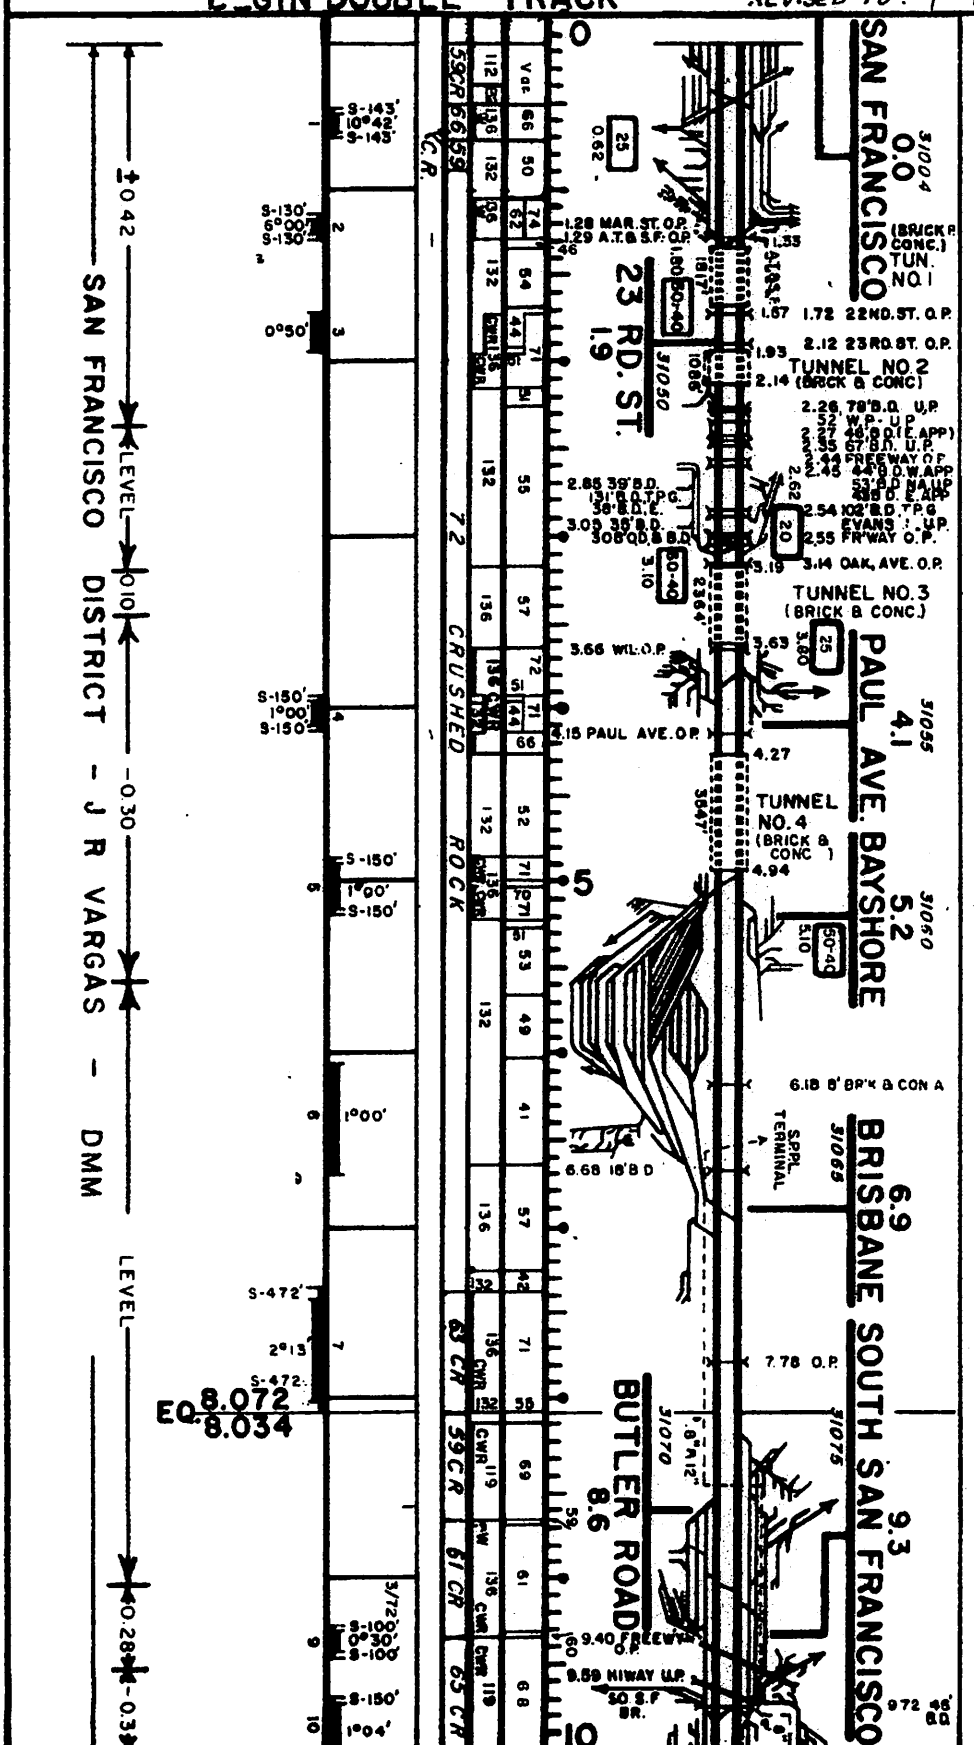

SAN FRANCISCO DISTRICT - J R VARGAS - DMM

REVISED TO: 1-1-80

0.188 W. 0.302 E. 0.419 W. 0.576 E. 301
60-40 70-55

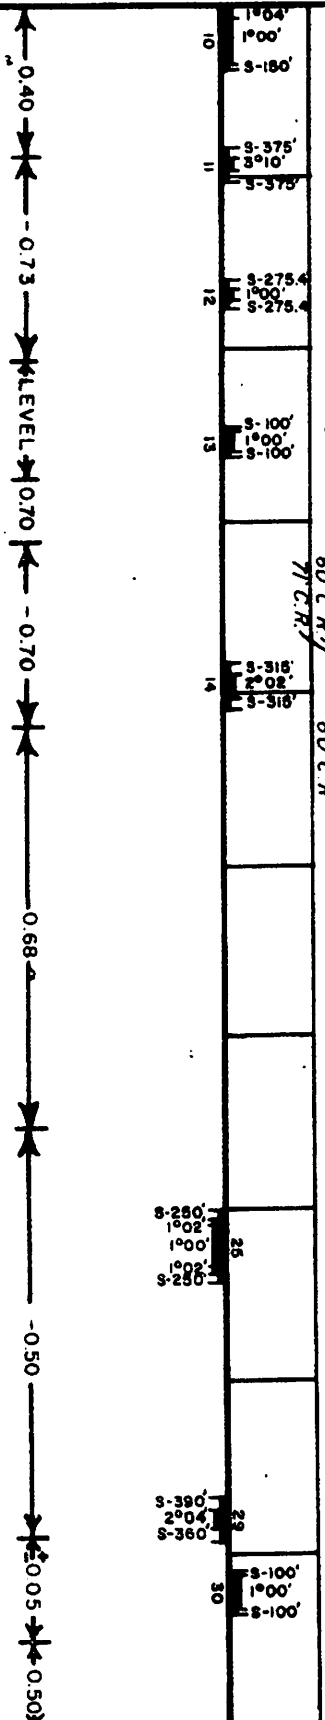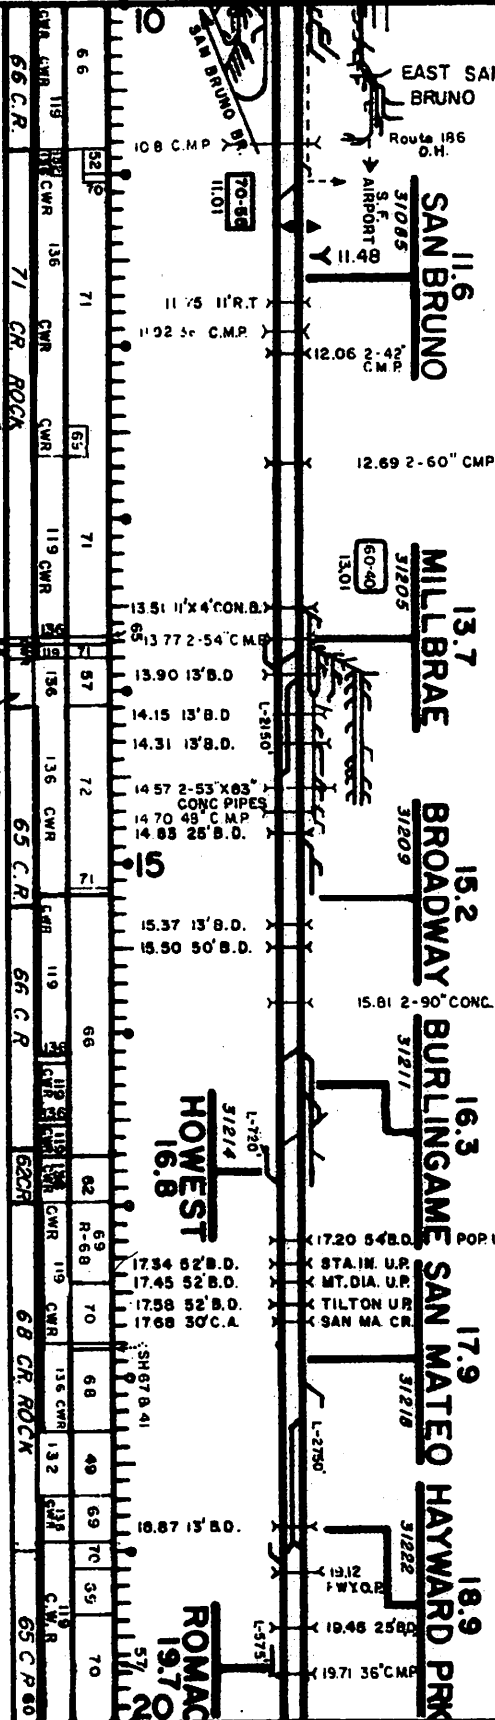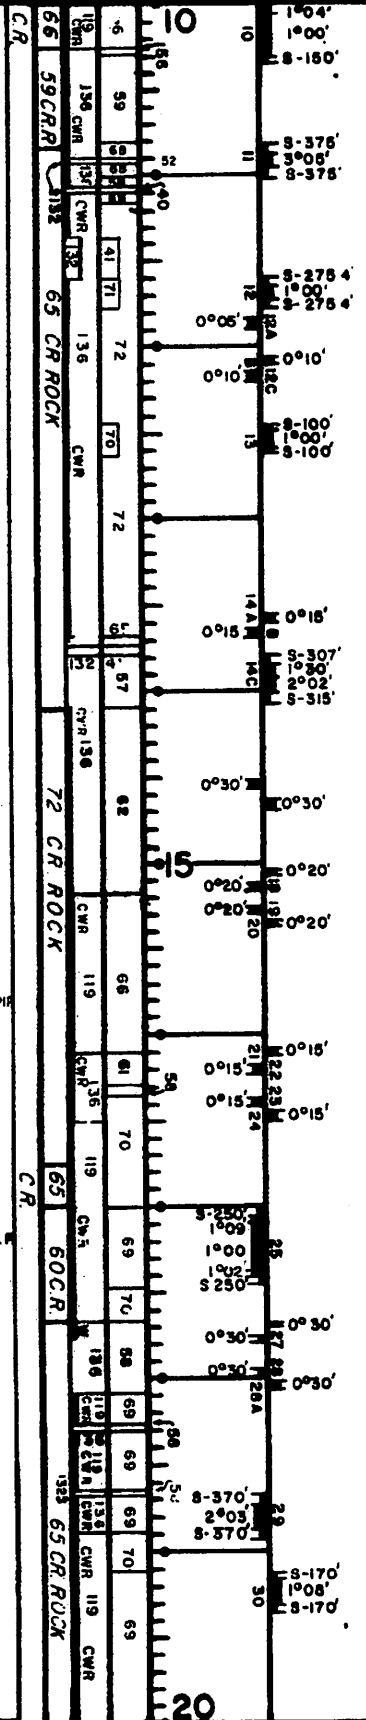

0.40 0.73 LEVEL 0.70 0.70 0.68 0.50 0.505

0.419 W

0.576 E


70-55

CITY ORD 45



0.512 W

0.477 E


302

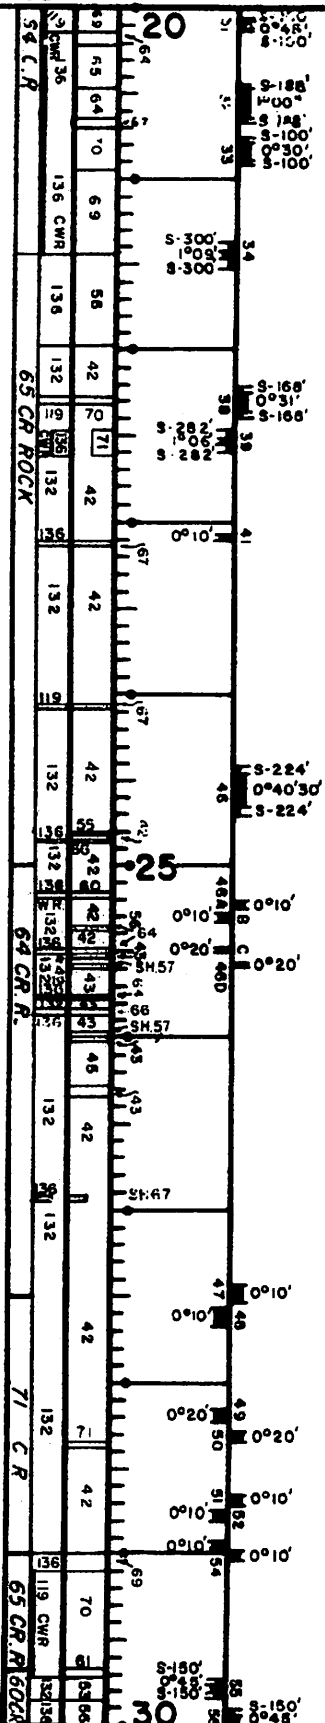


REVISED 1-1-80

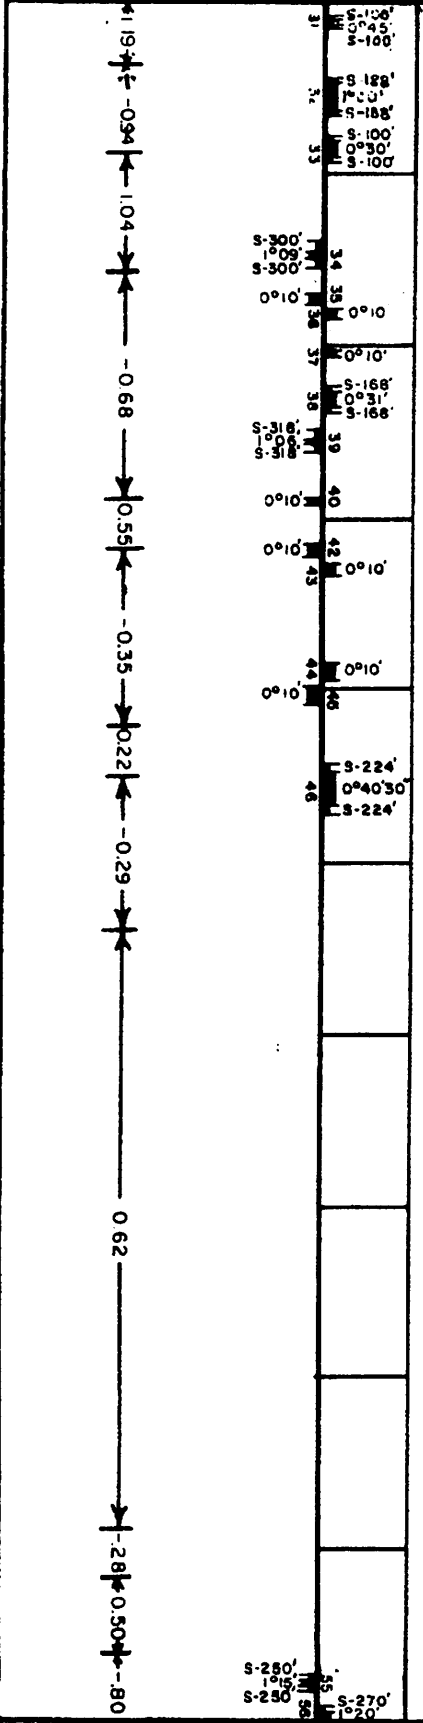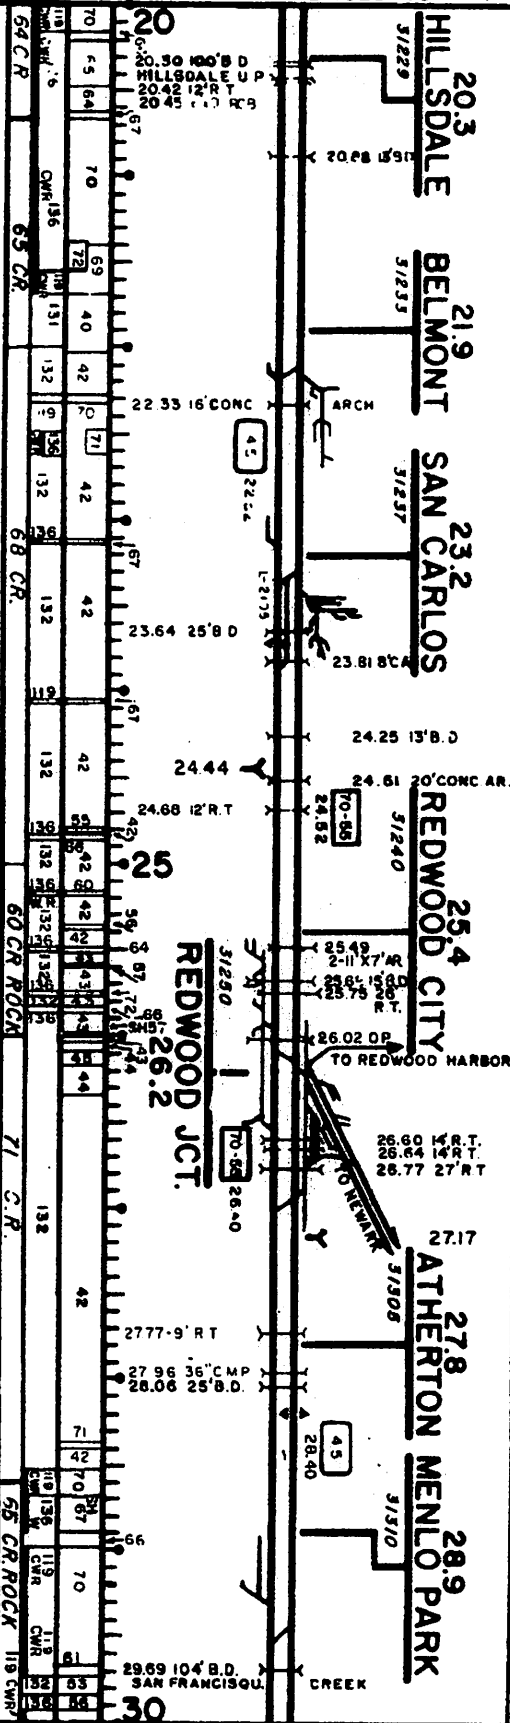


REVISED TO: 1-1-80

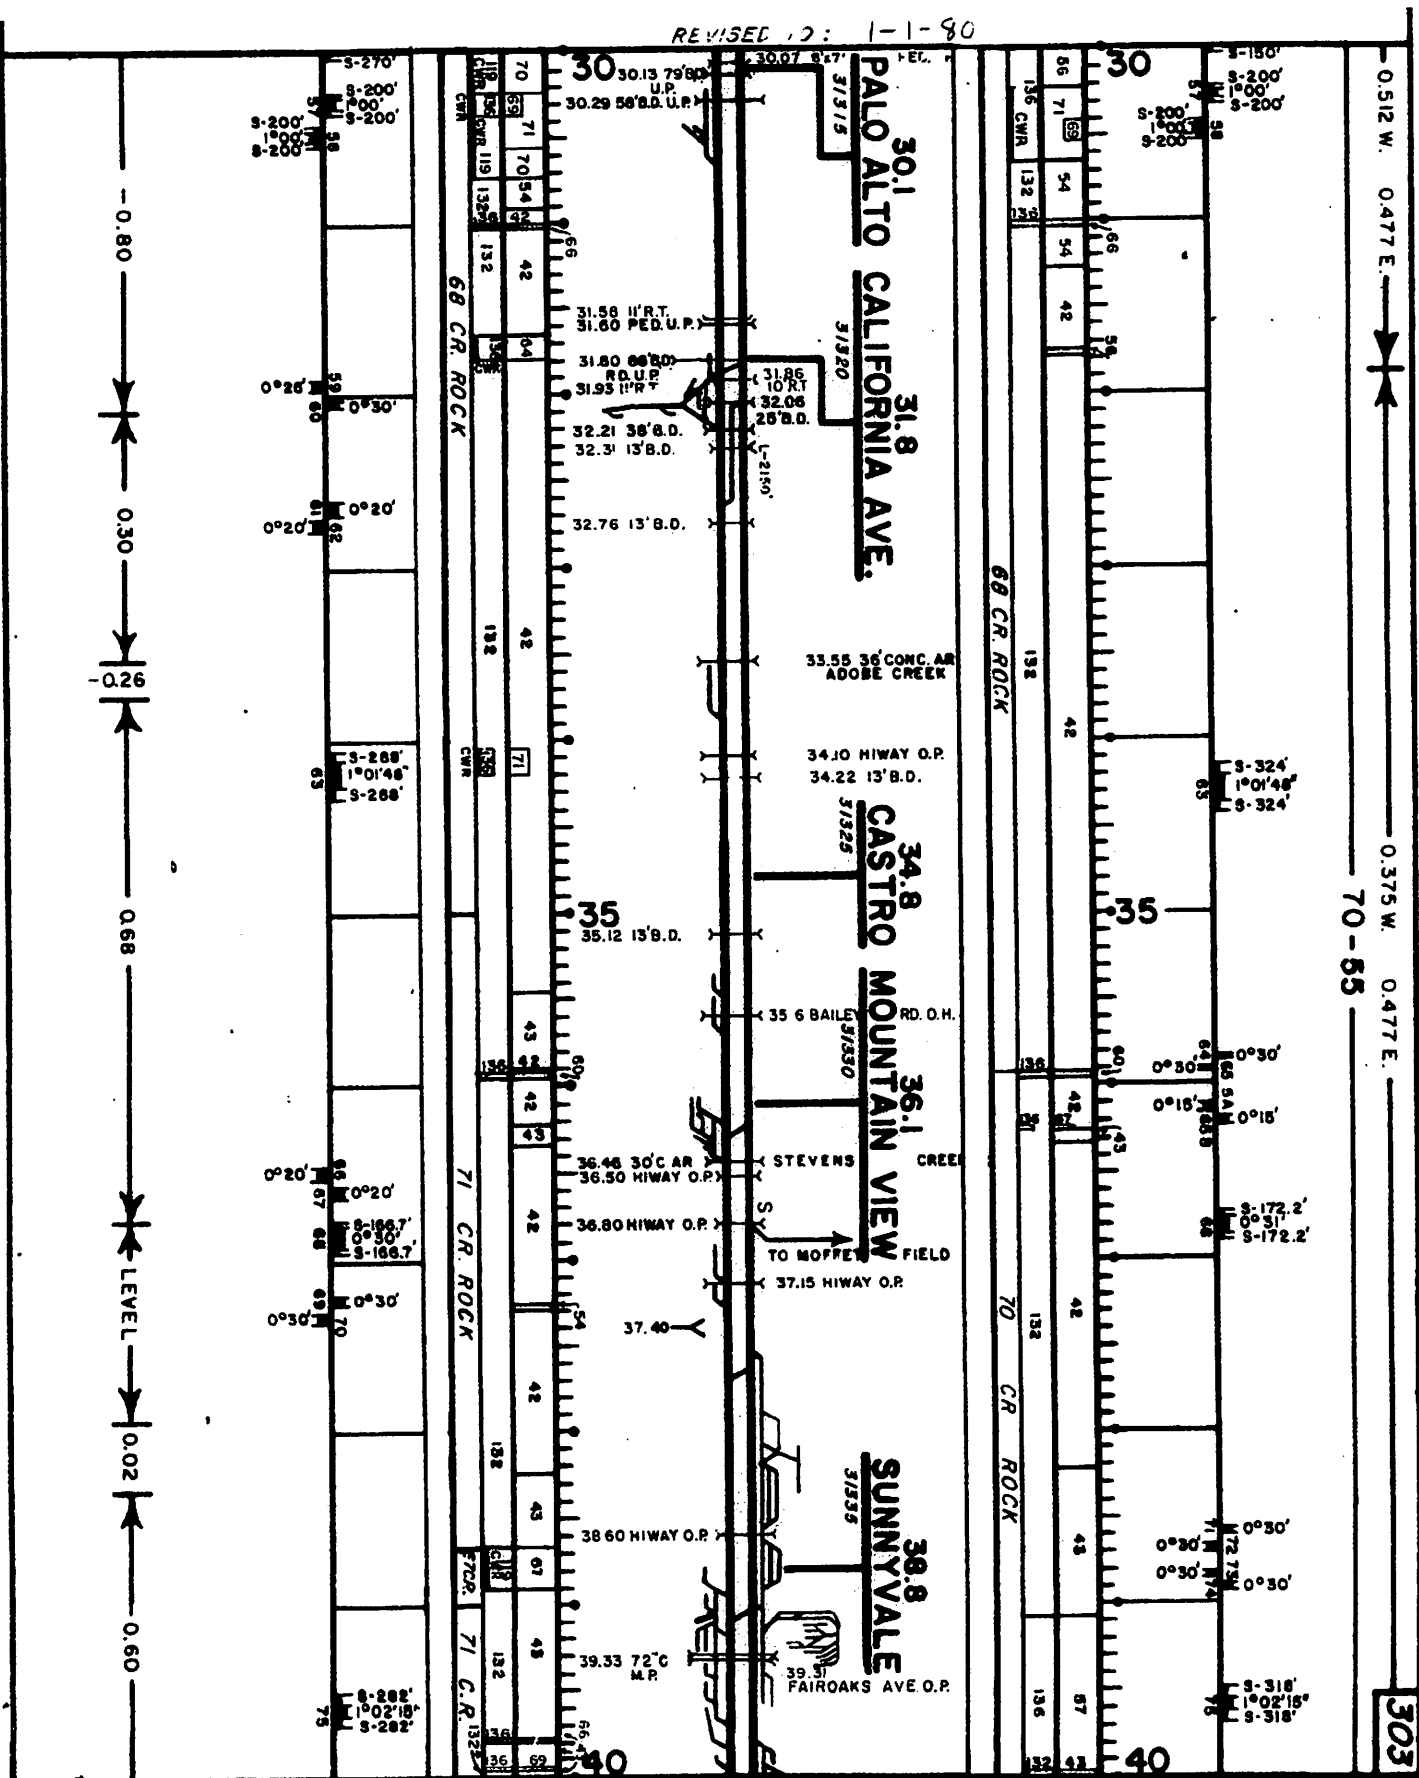


REVISED TO 1-1-80

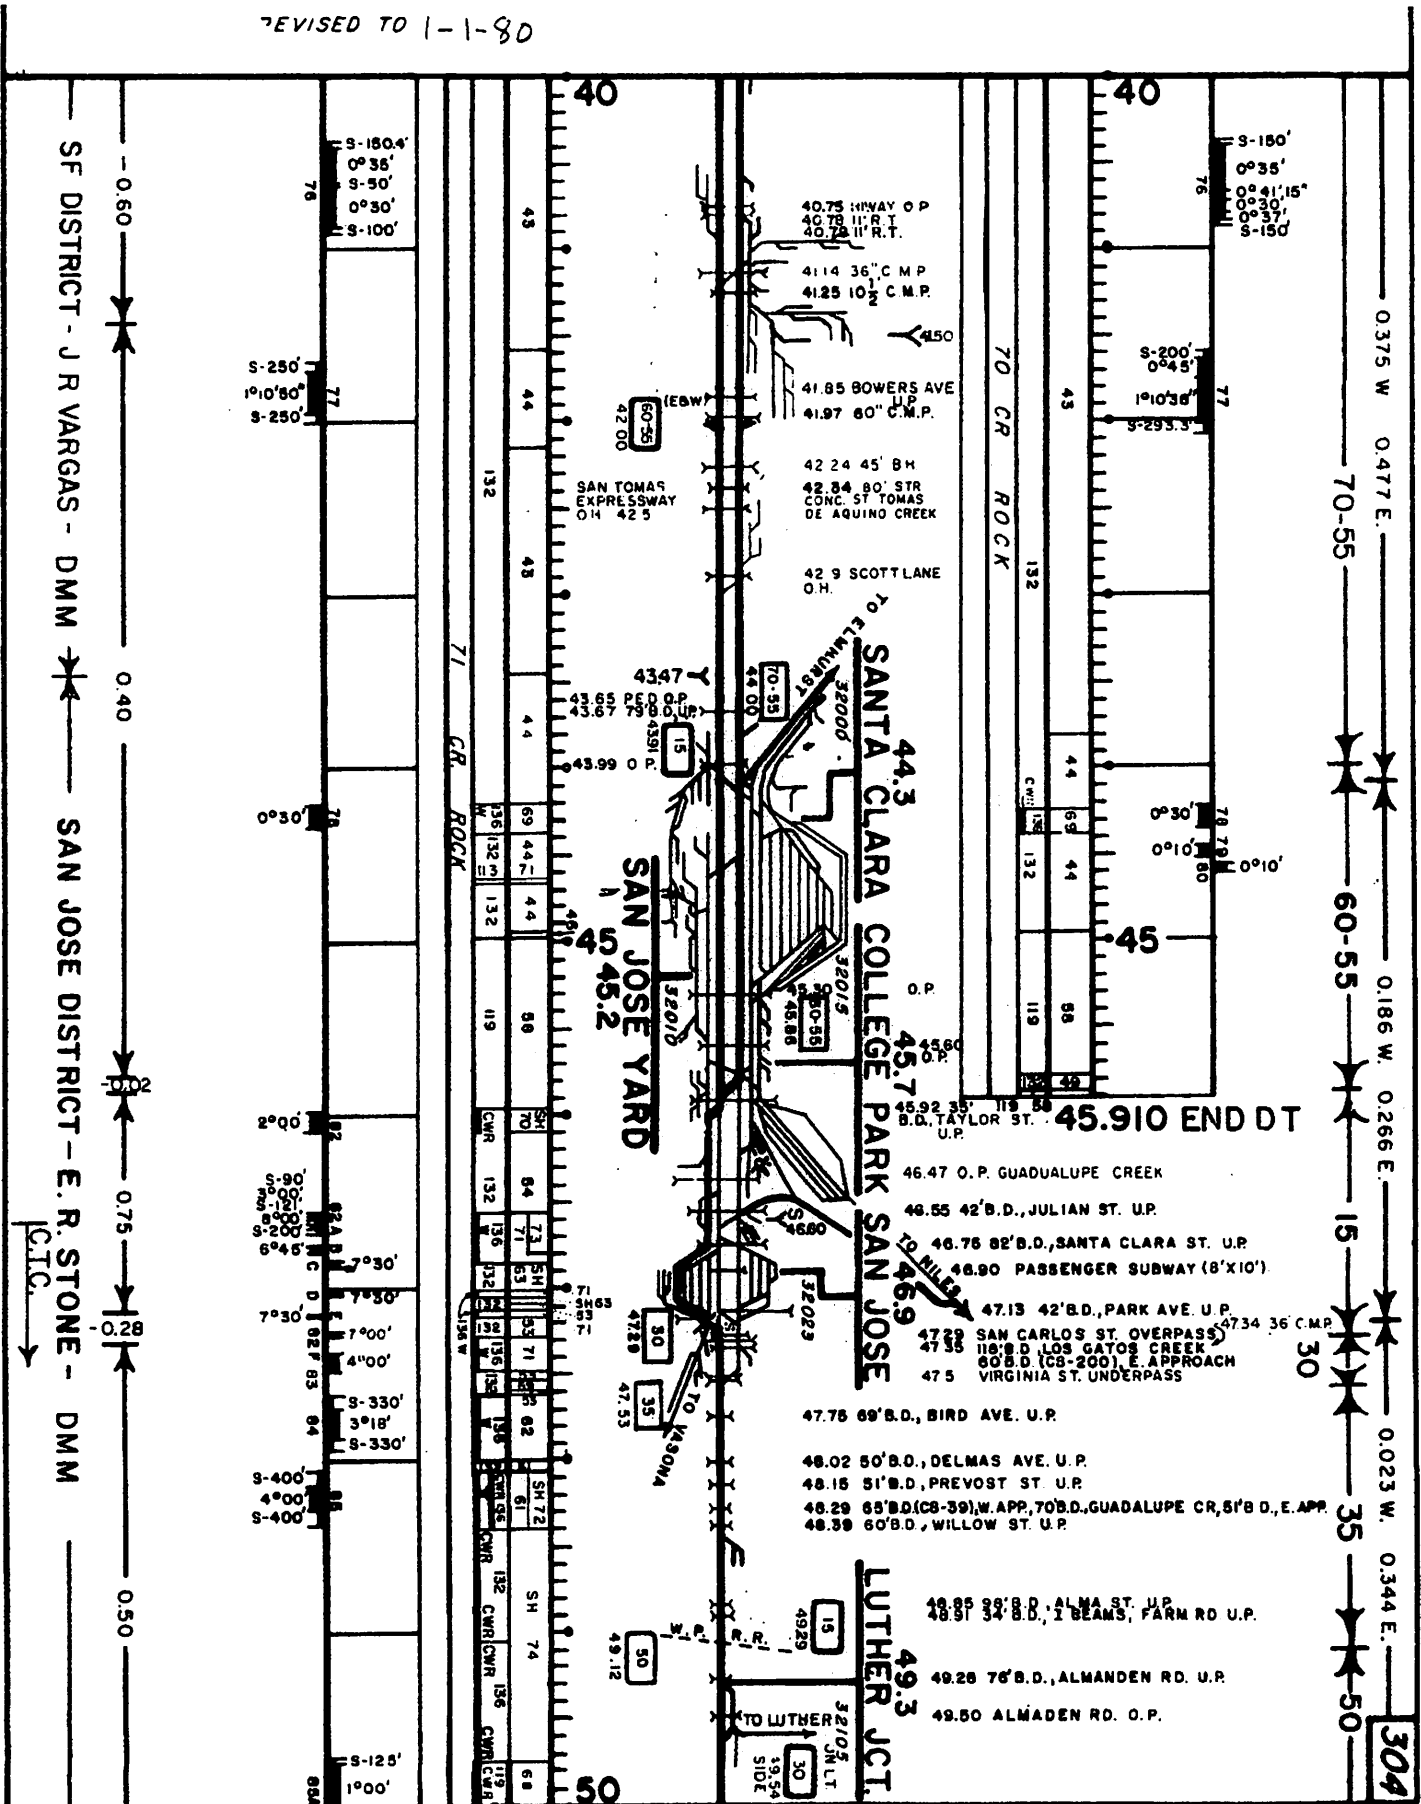

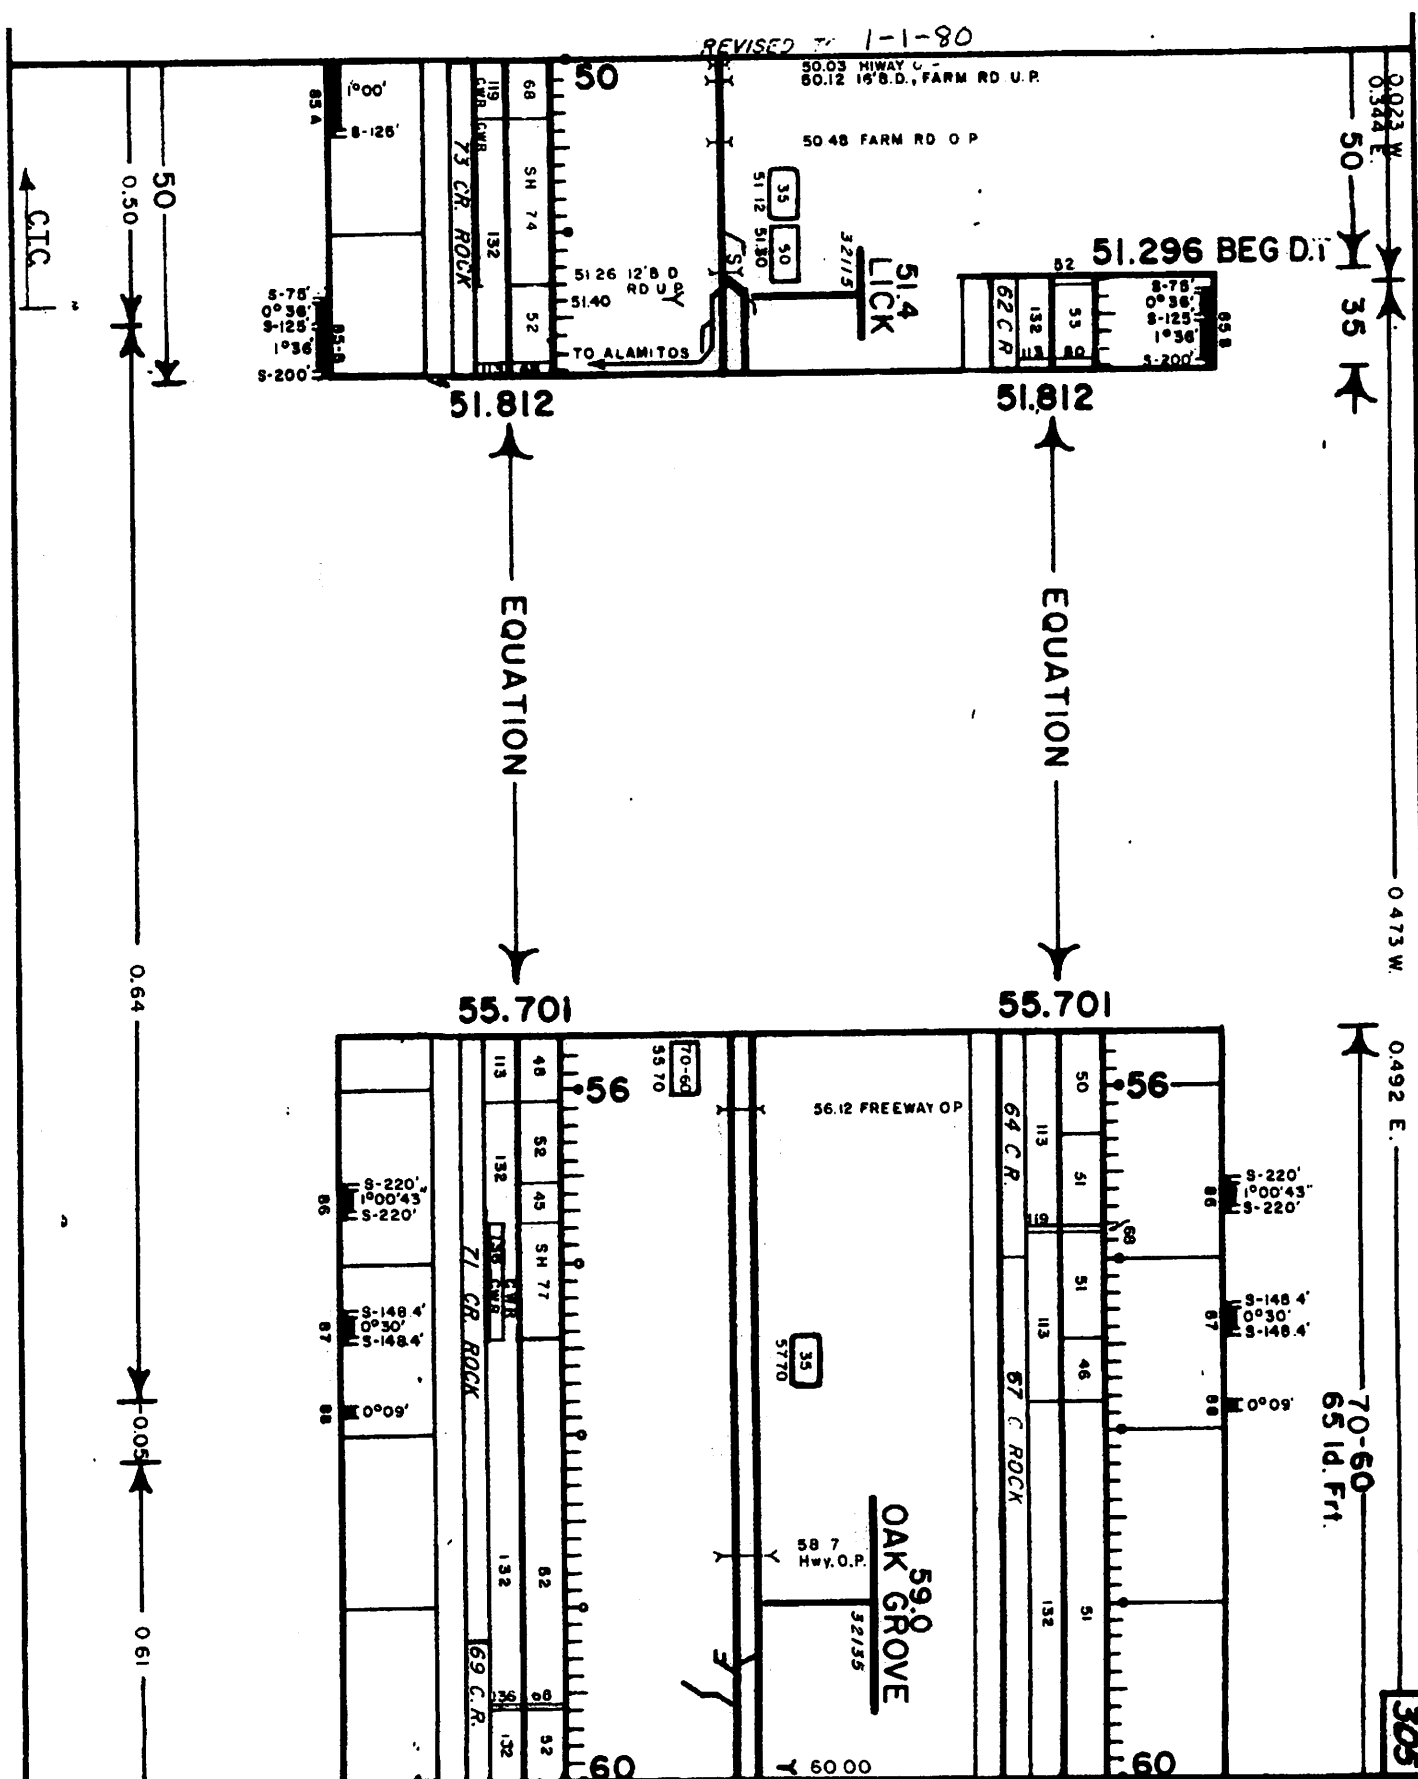

70-60
5 Id. Fri.

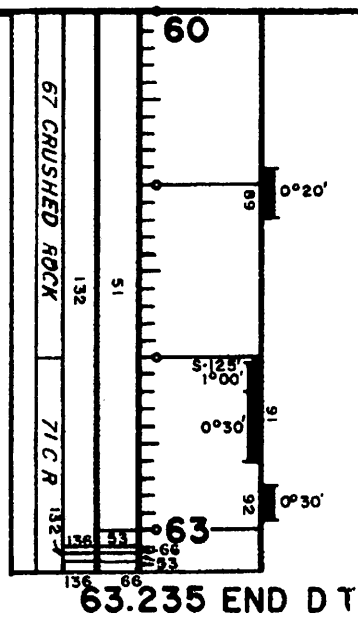

³⁶ ⁶⁸ 63.235 END D T

62.53 31' B.D.
LAGUNA SECO


63.1
COYOTE

32140

66.3
PERY
32/45

32145

69.63 36" C.M.P.
69.71 4" CONC. ARCH
69.79 93" O.D. THRU PL. GIR., HIWAY U.P.

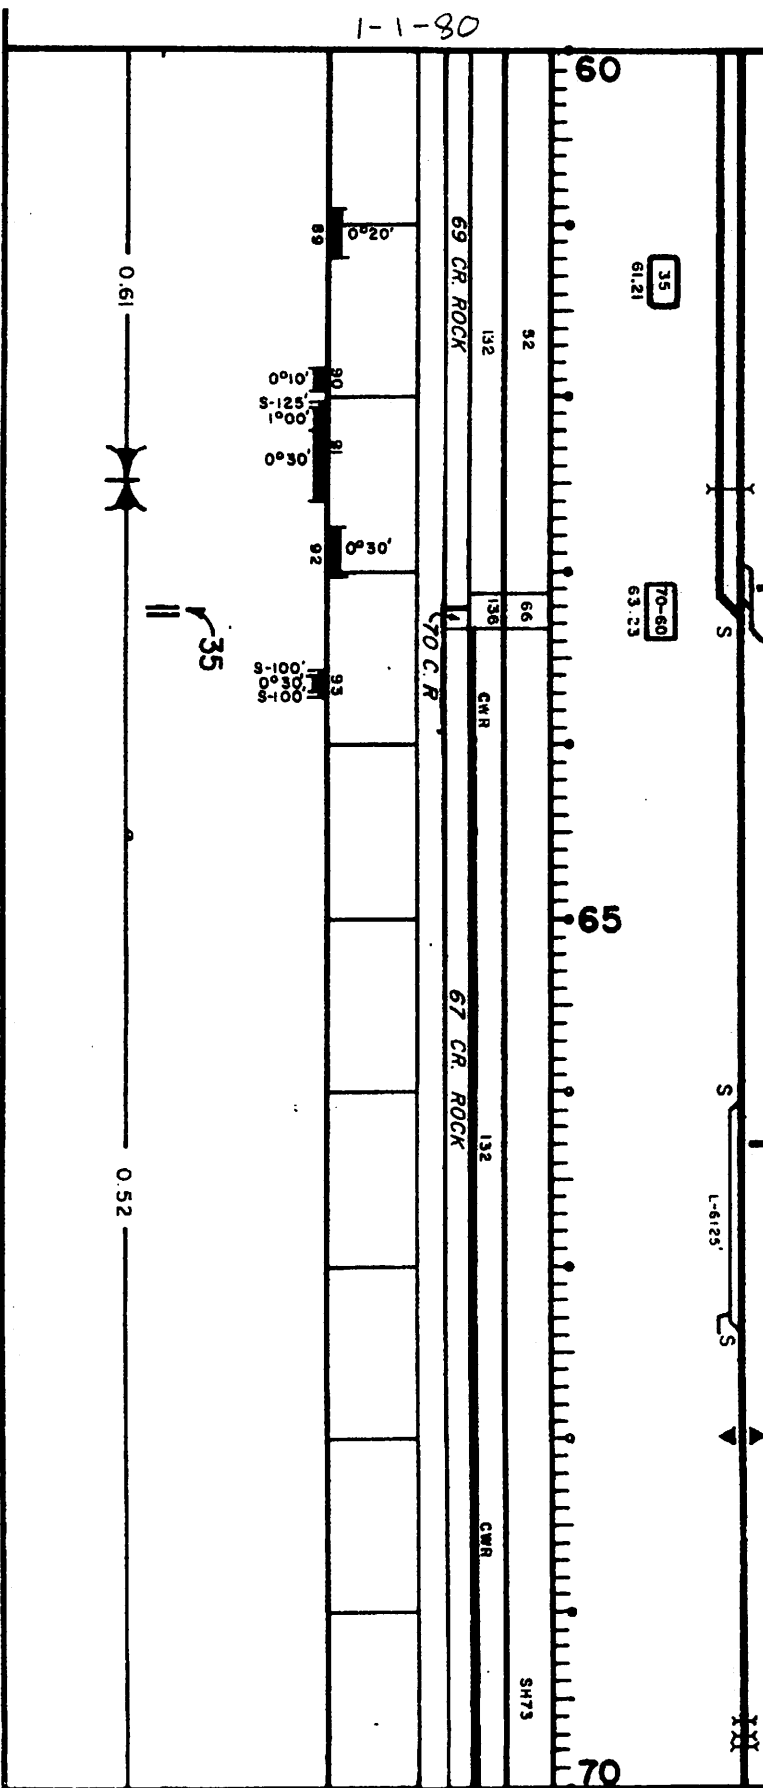

1-1-80


35

0.473 W. 0.492 E. 0.579 W. 0.221 E. 308




35 25 35 60-55 60 Id. Ft. 50 35

80.463 BEG.D.T

86.488 END D.T

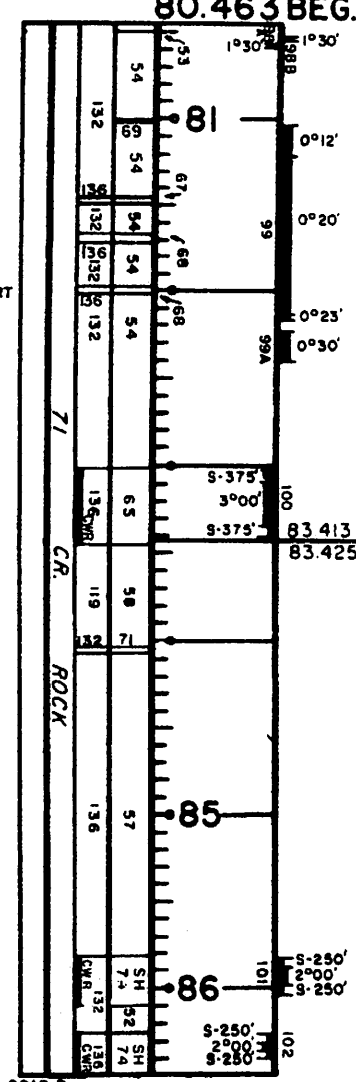

REVISED TO 1-1-80

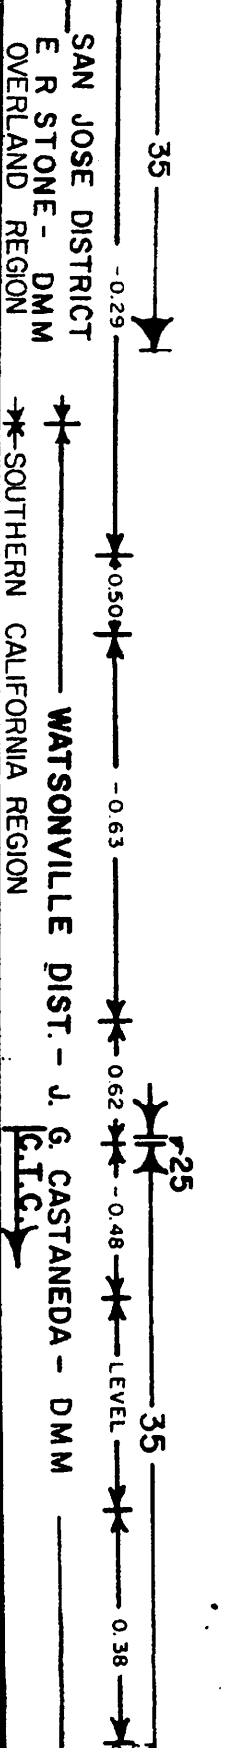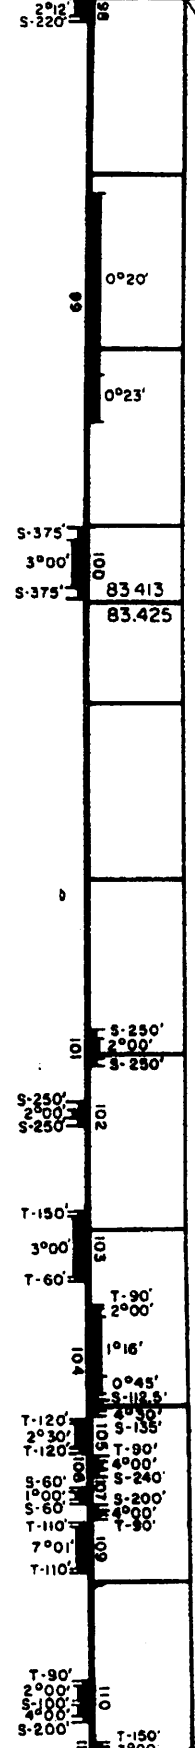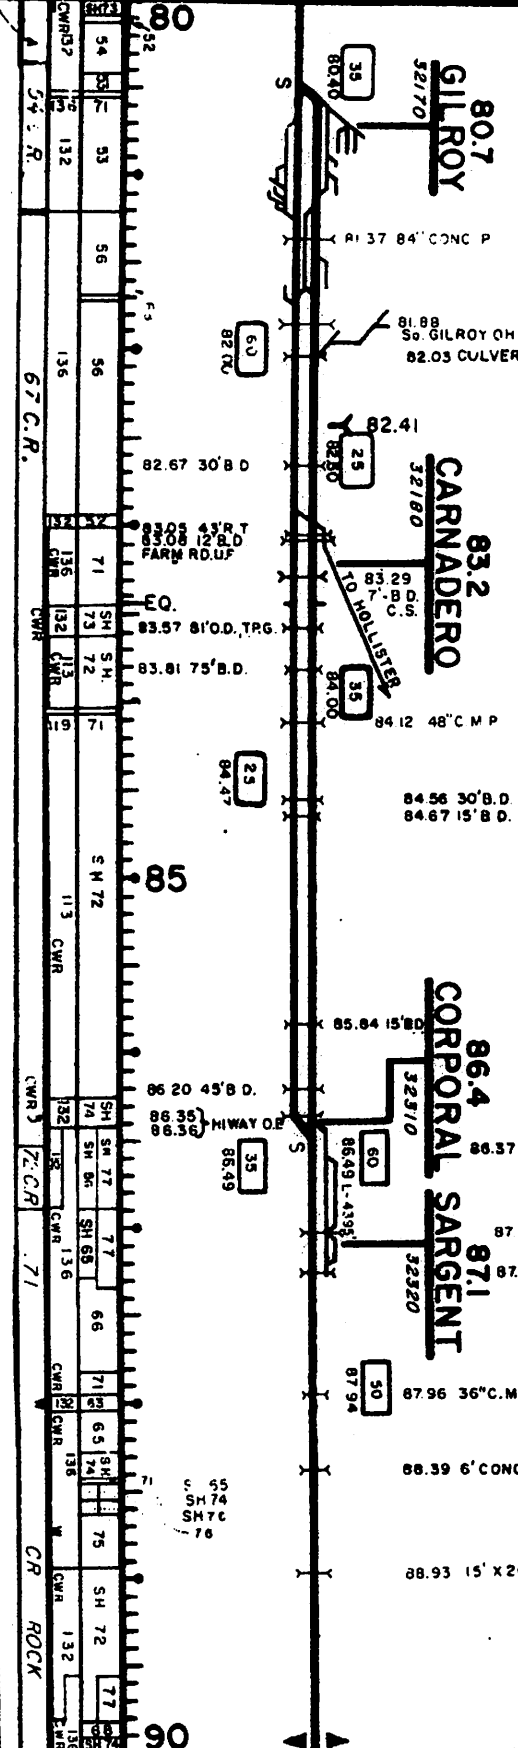



SAN JOSE DISTRICT
E R STONE - DMM
OVERLAND REGION


WATSONVILLE DIST. - J. G. CASTANEDA - DMM
SOUTHERN CALIFORNIA REGION

C.T.C.

RE. SEC TO. 1-1-80

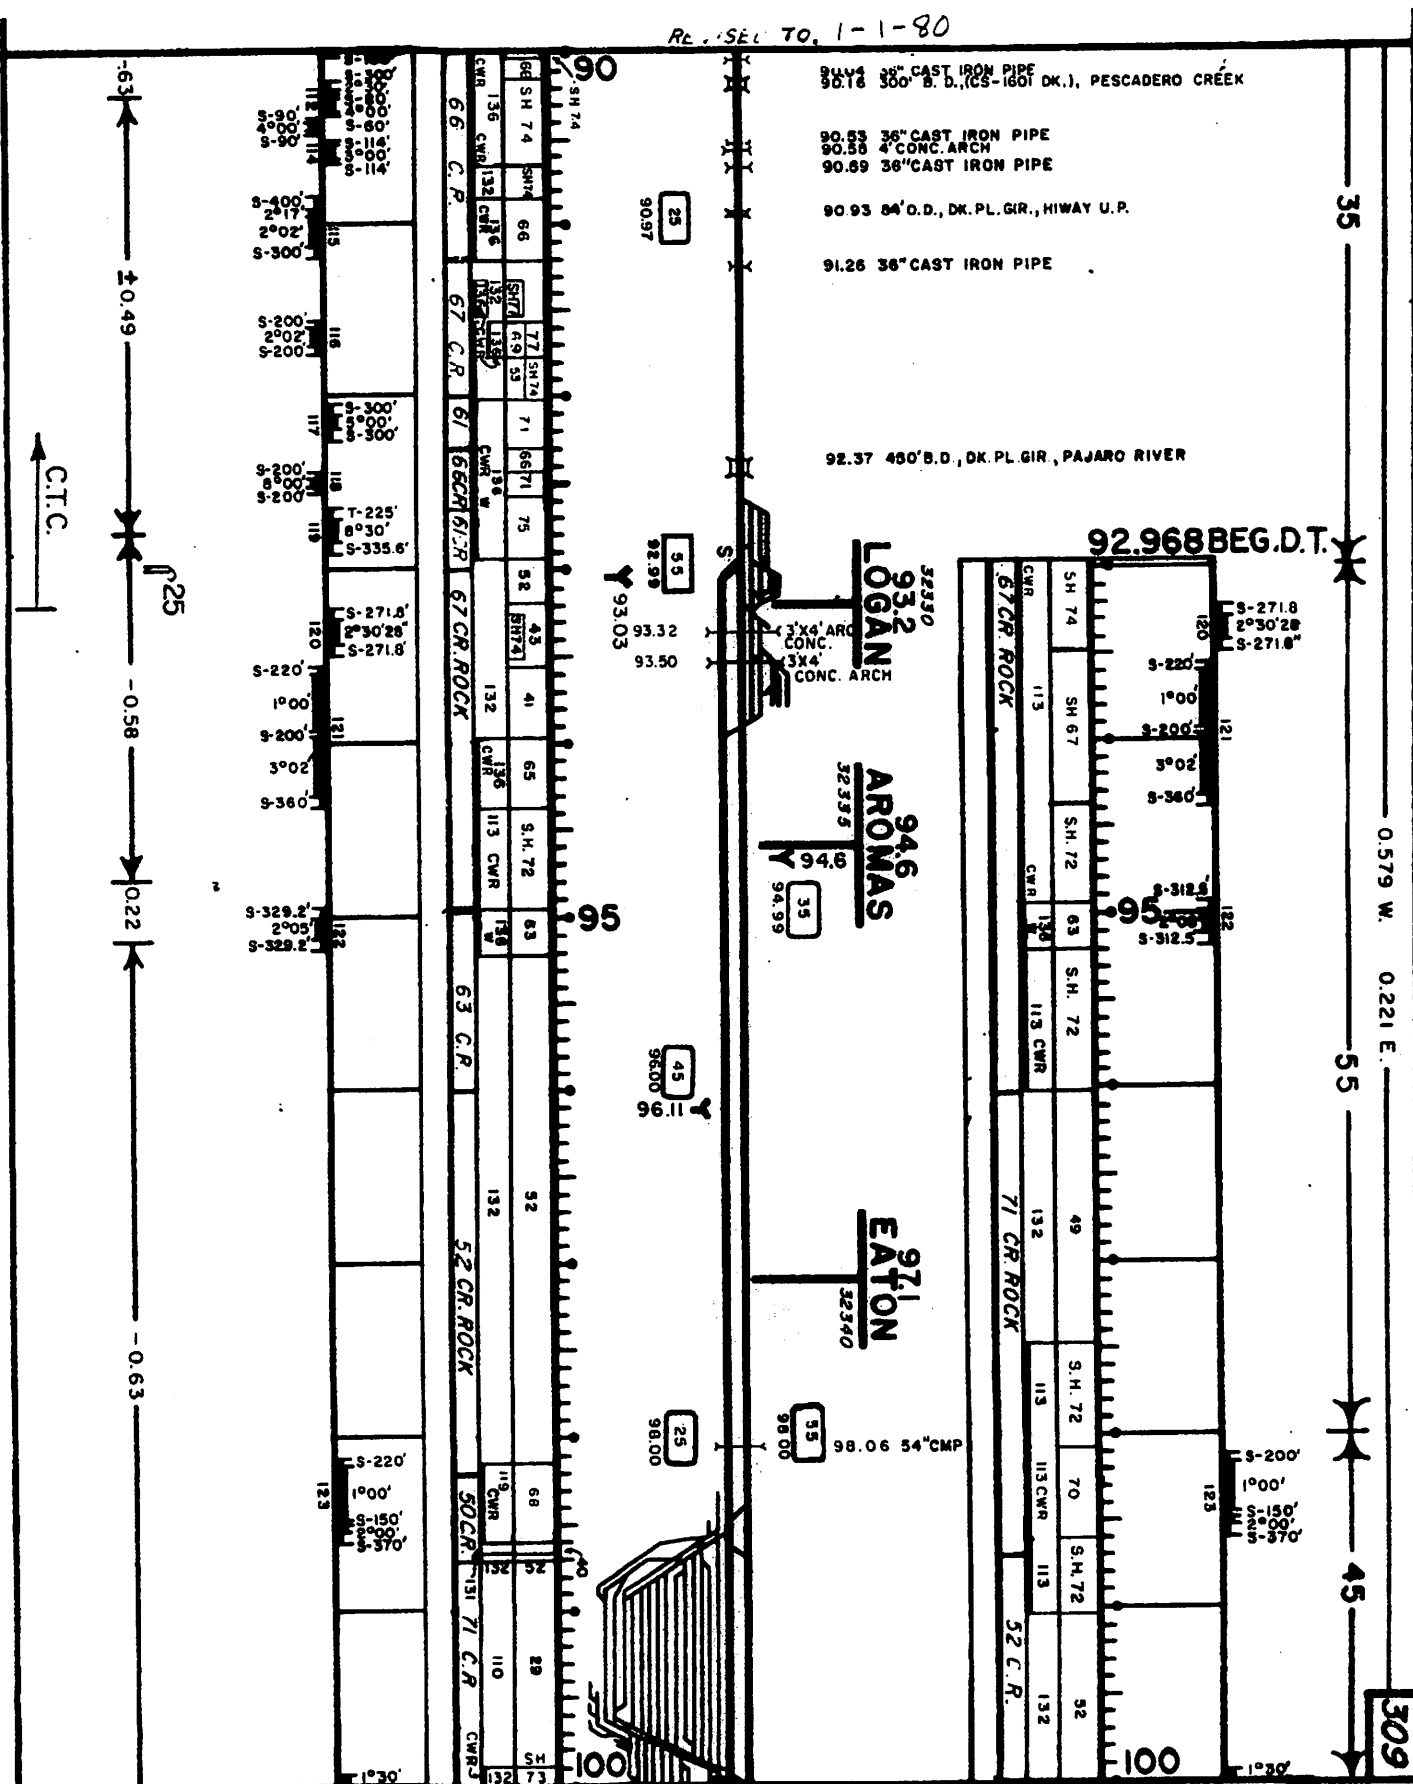

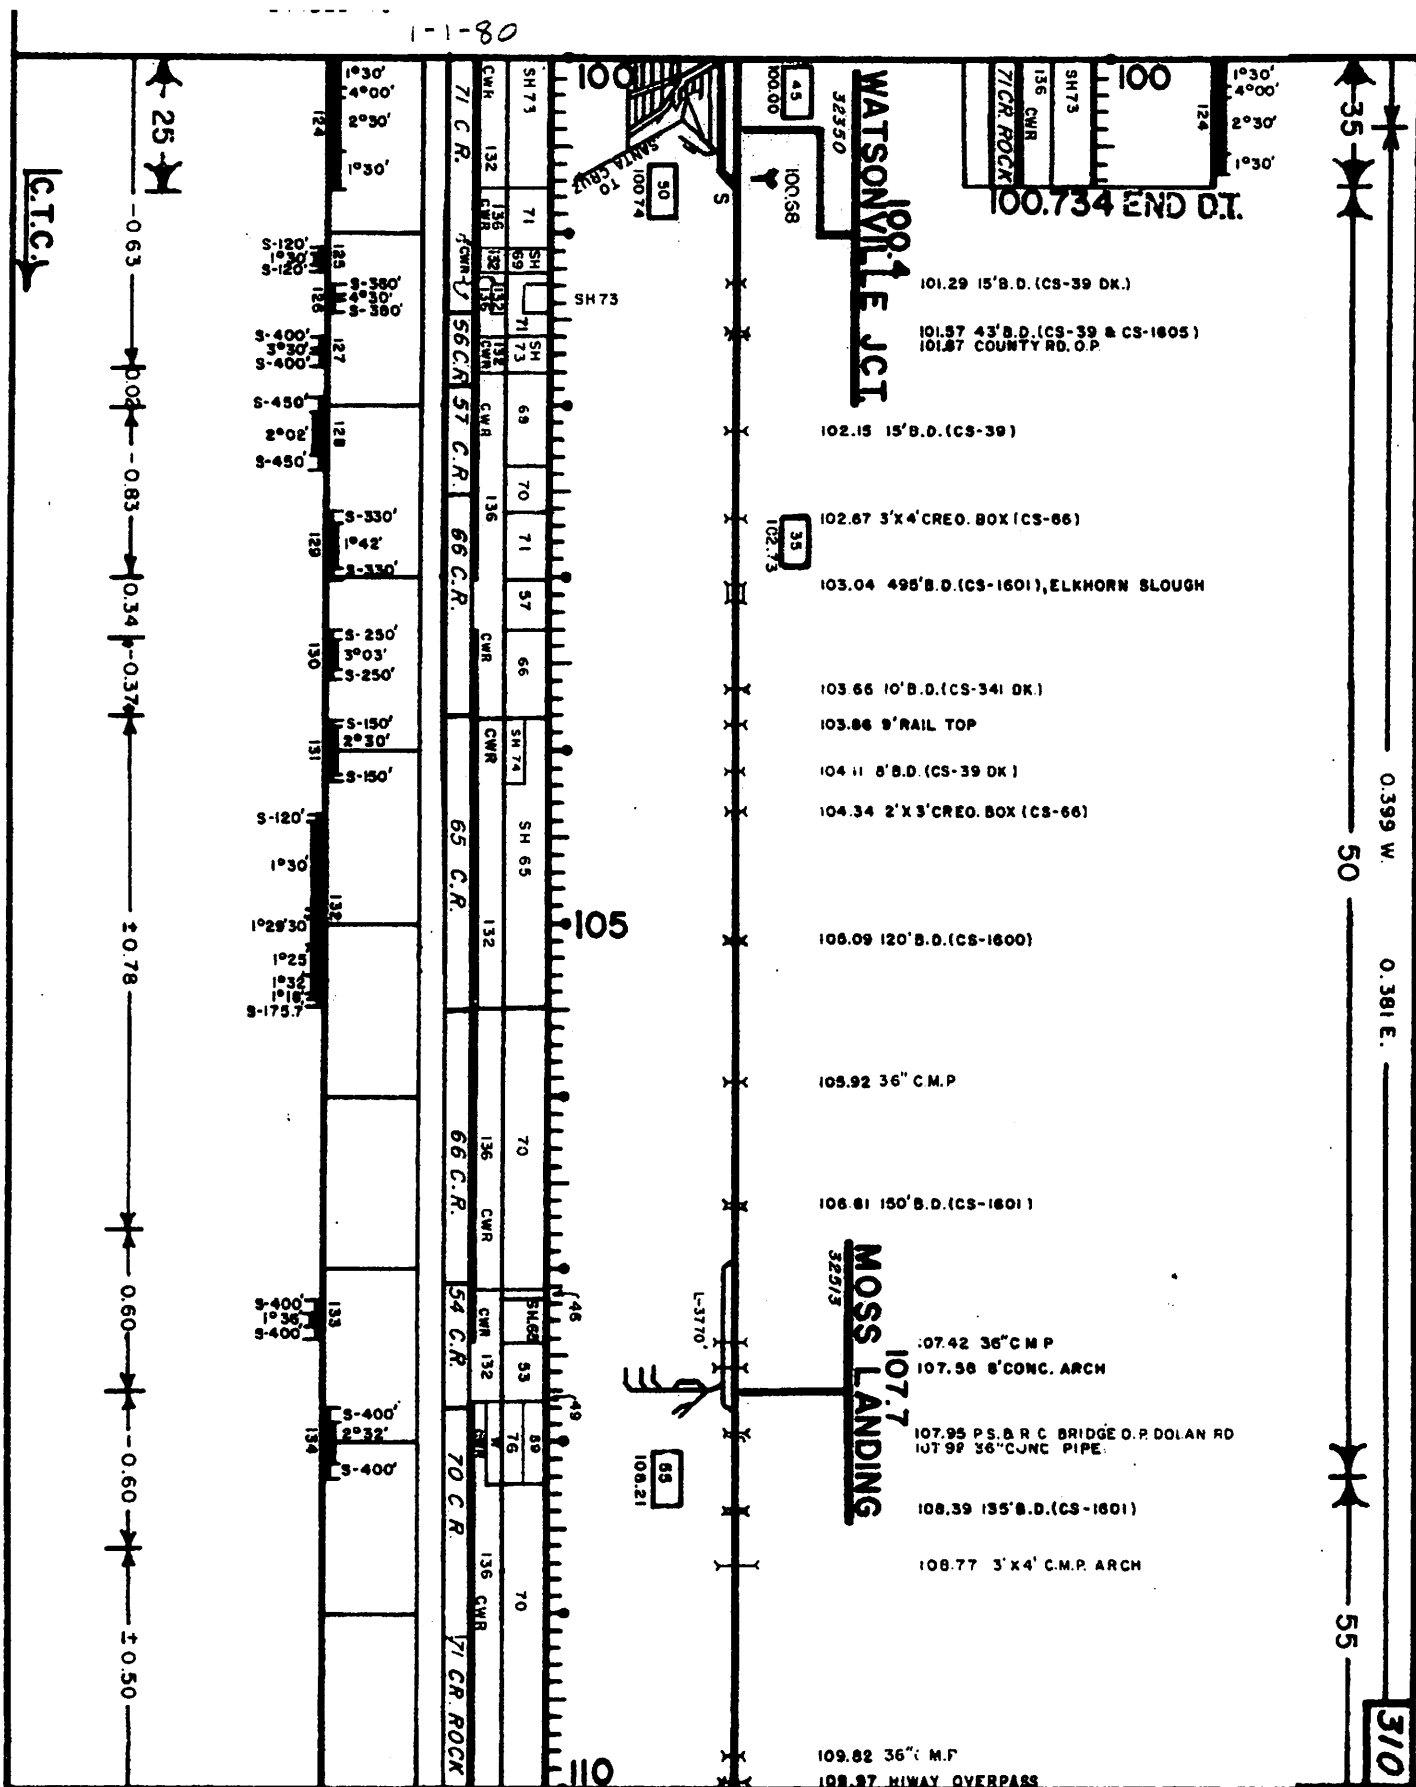

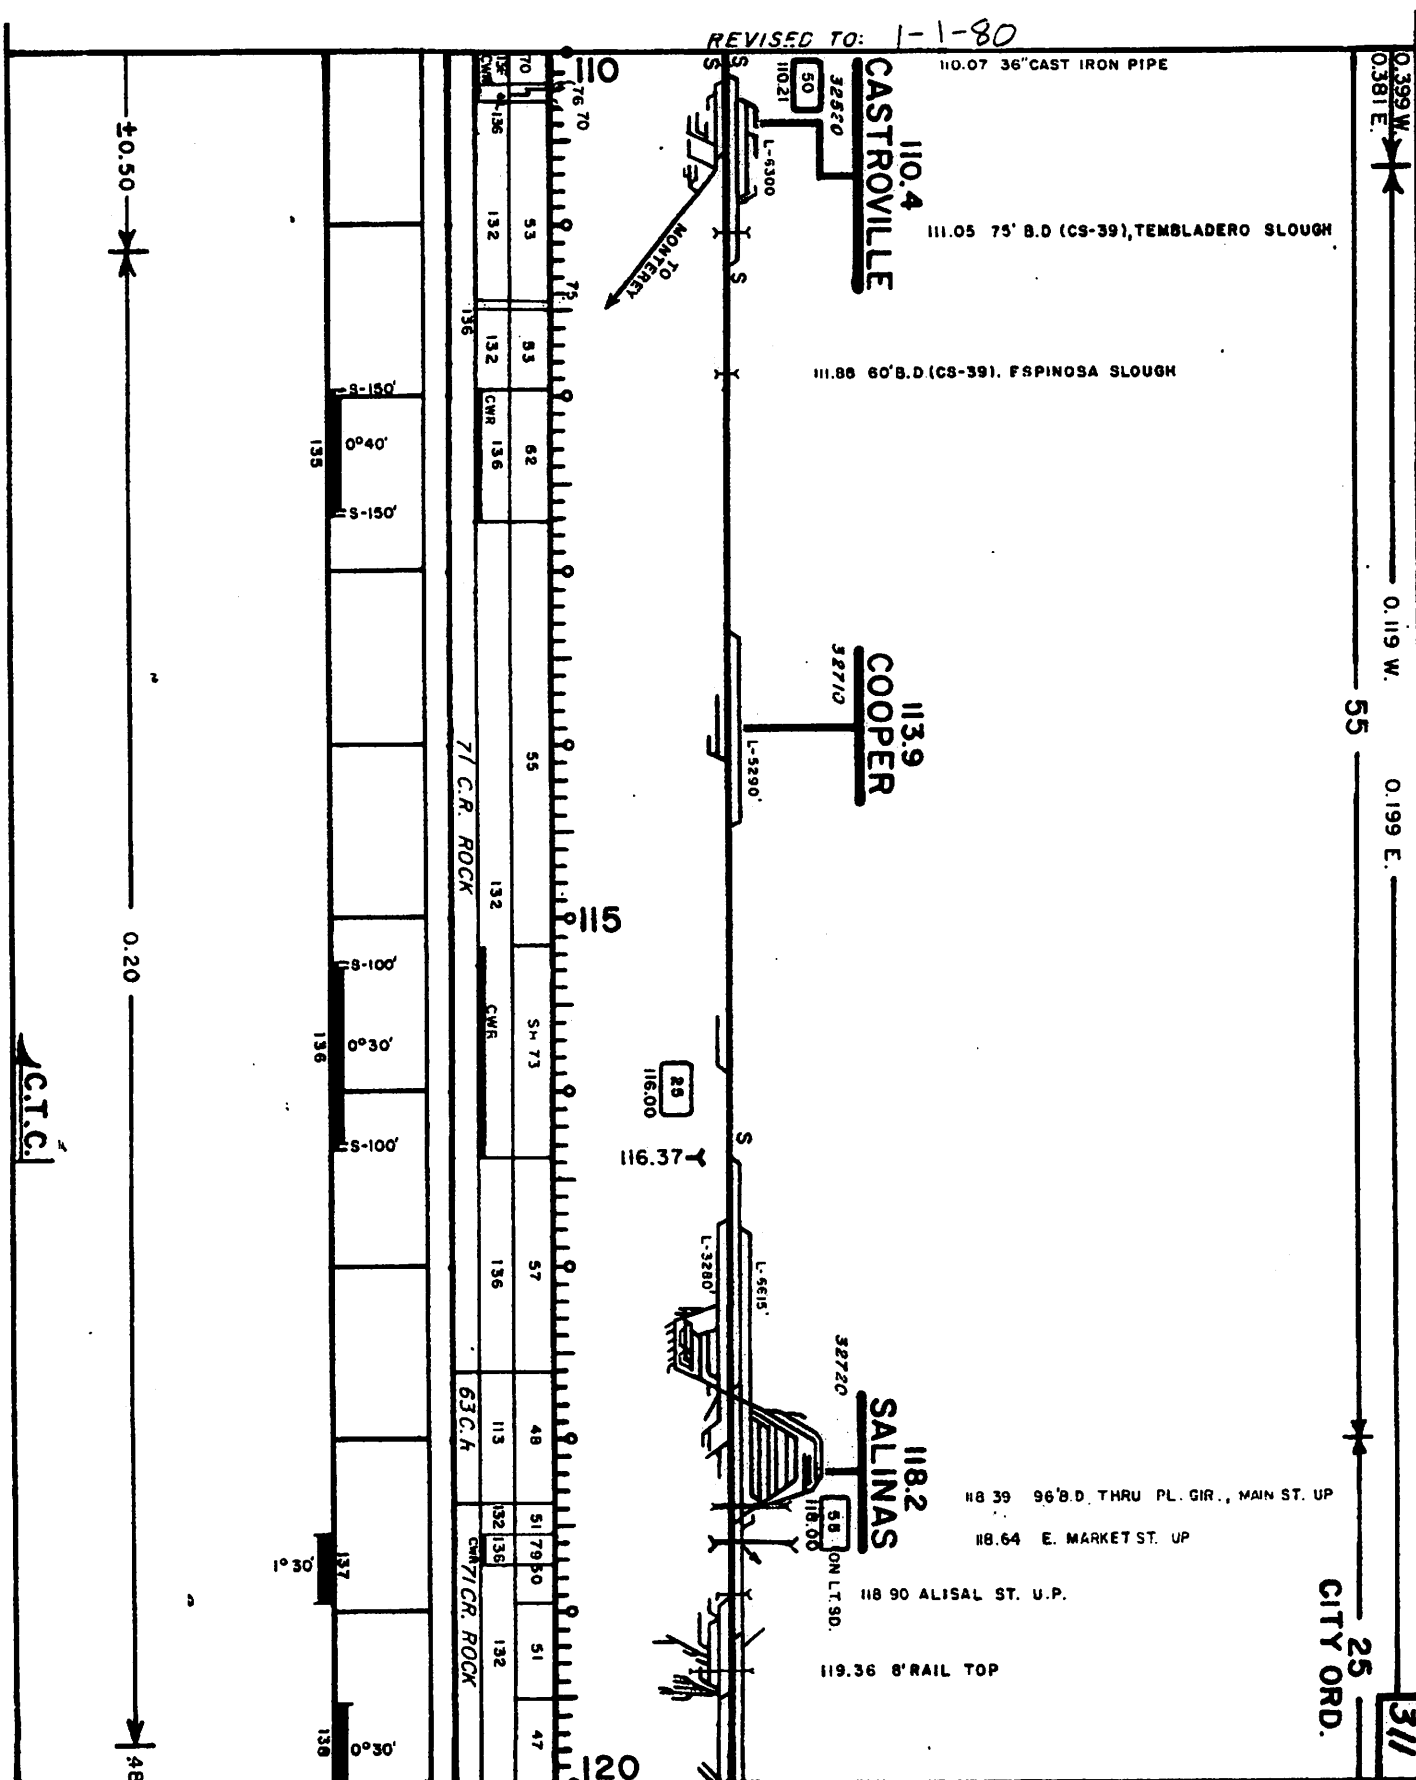


REVISED T. 1-1-80


0.552 W.

0.514 E.


70 - 55
60 Id. Frt.

3/3

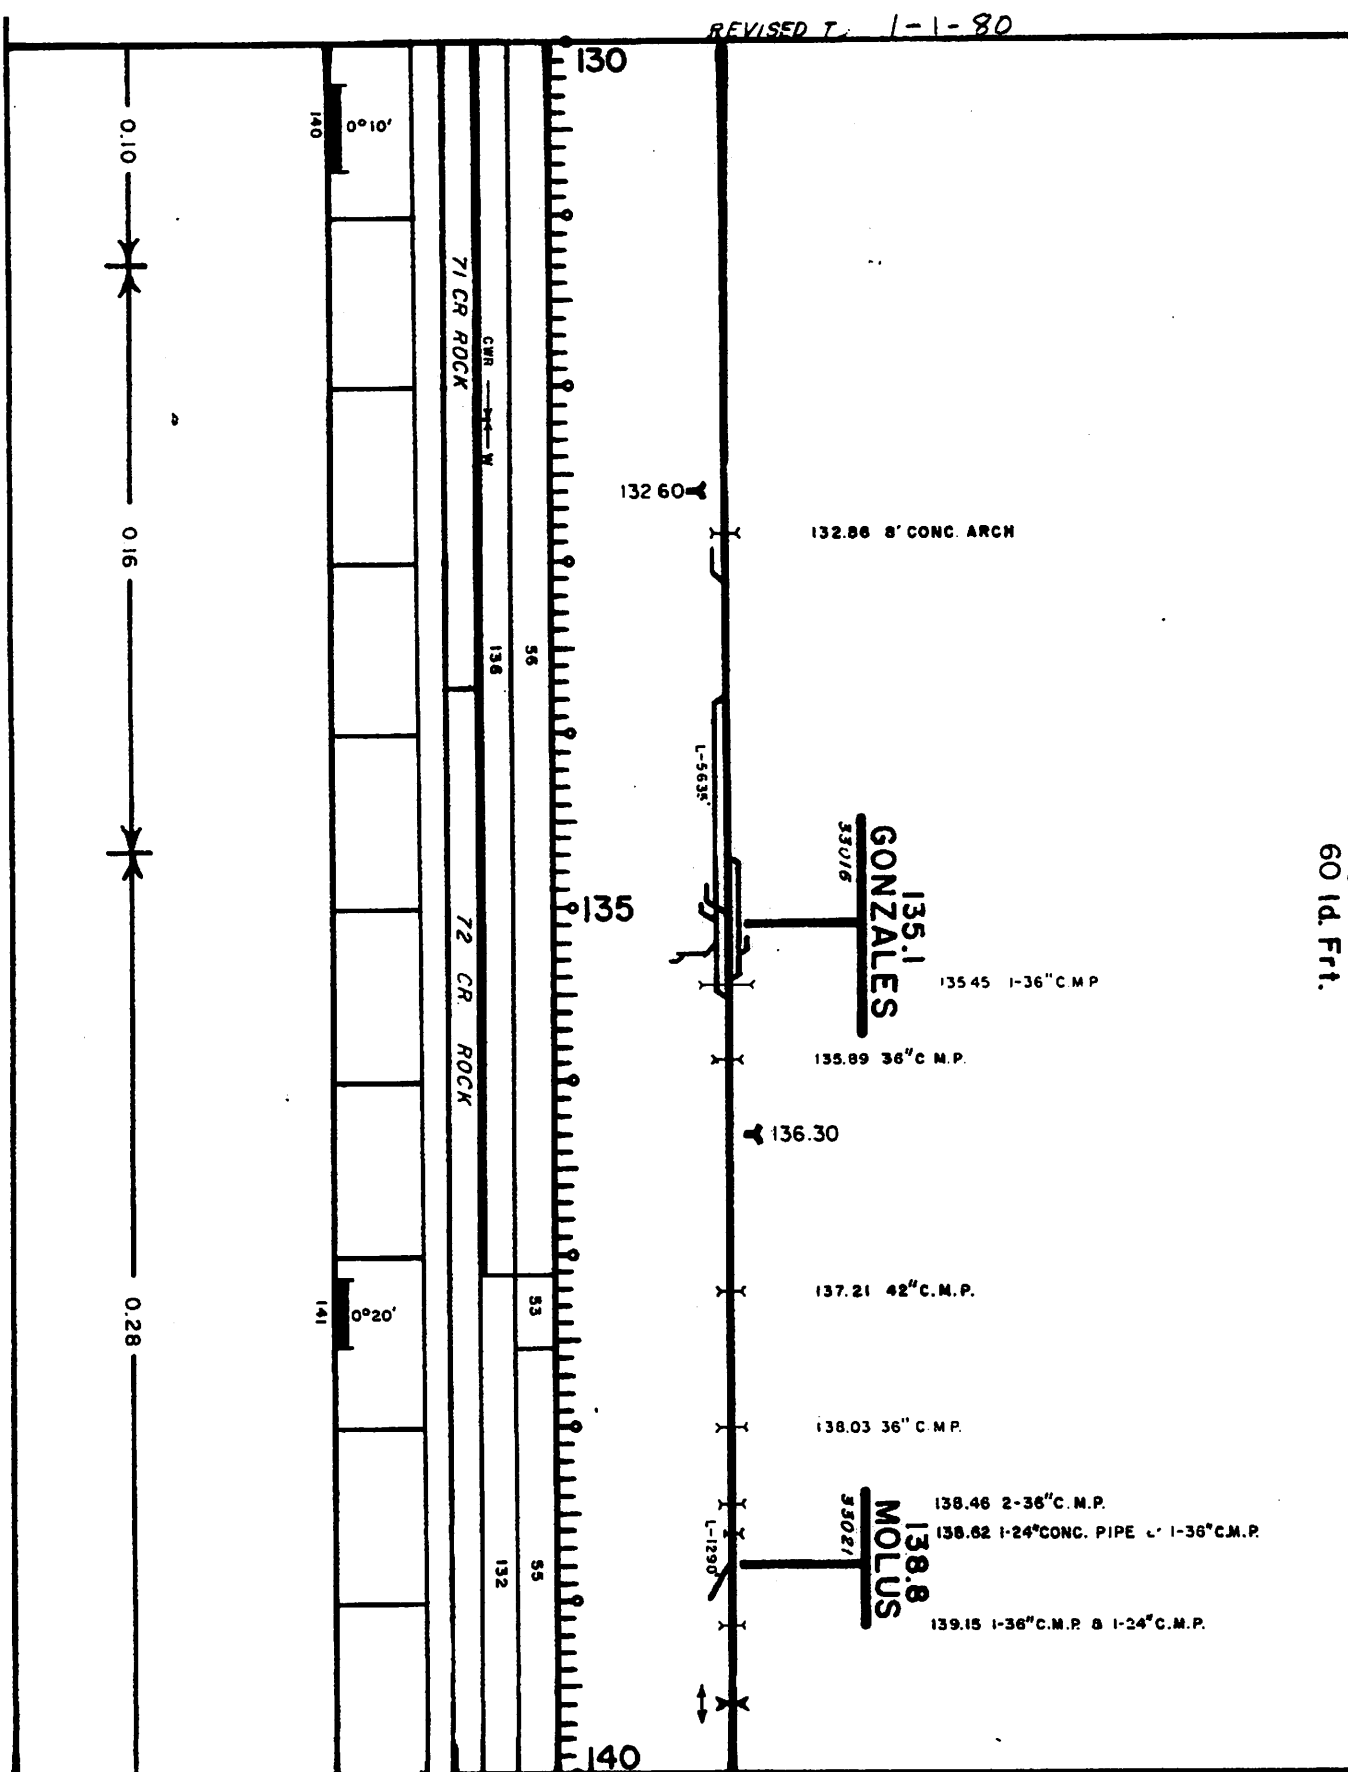

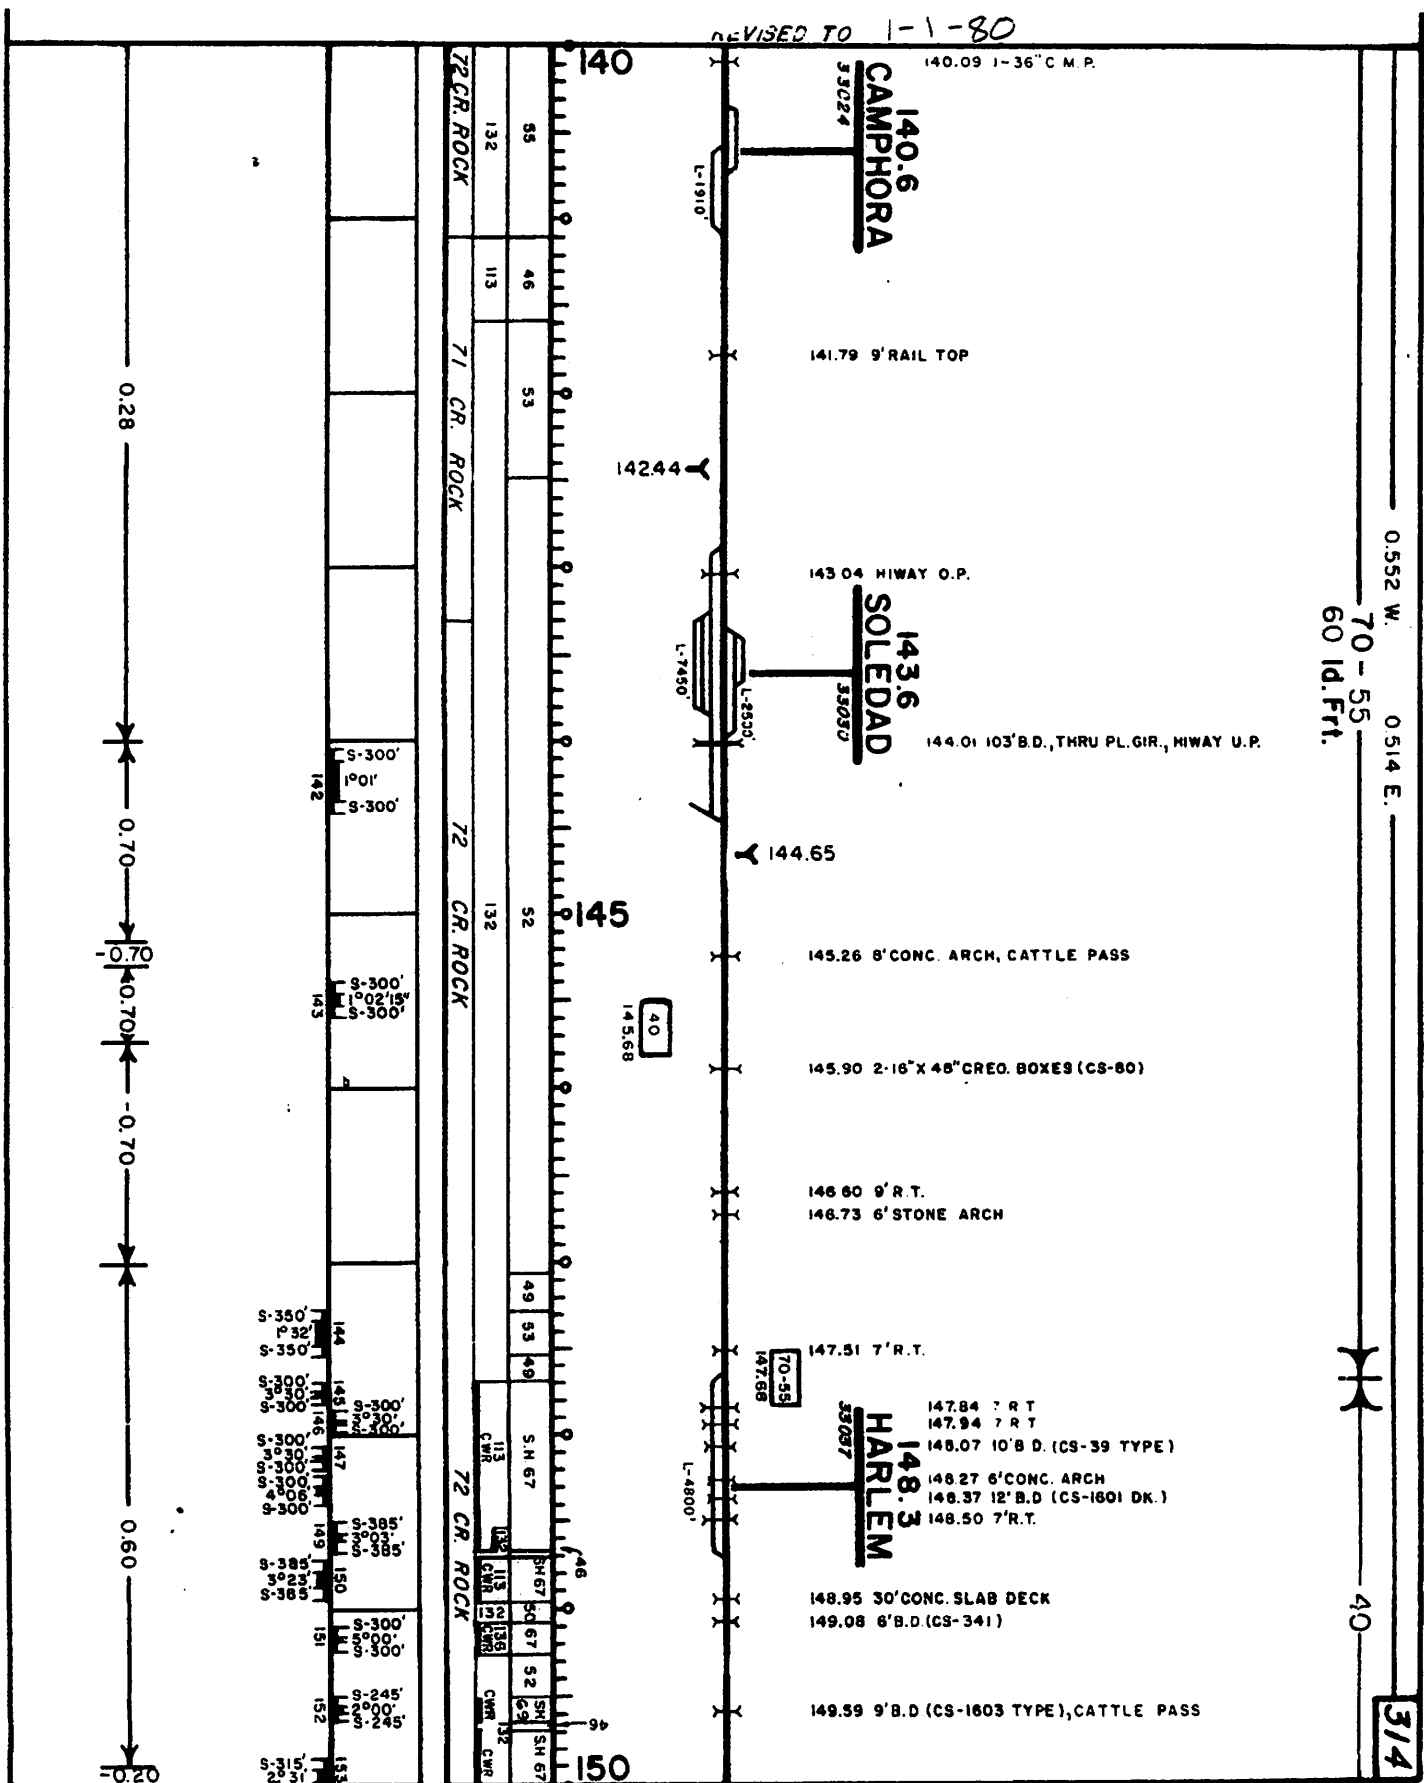

REVISED TO 1-1-80

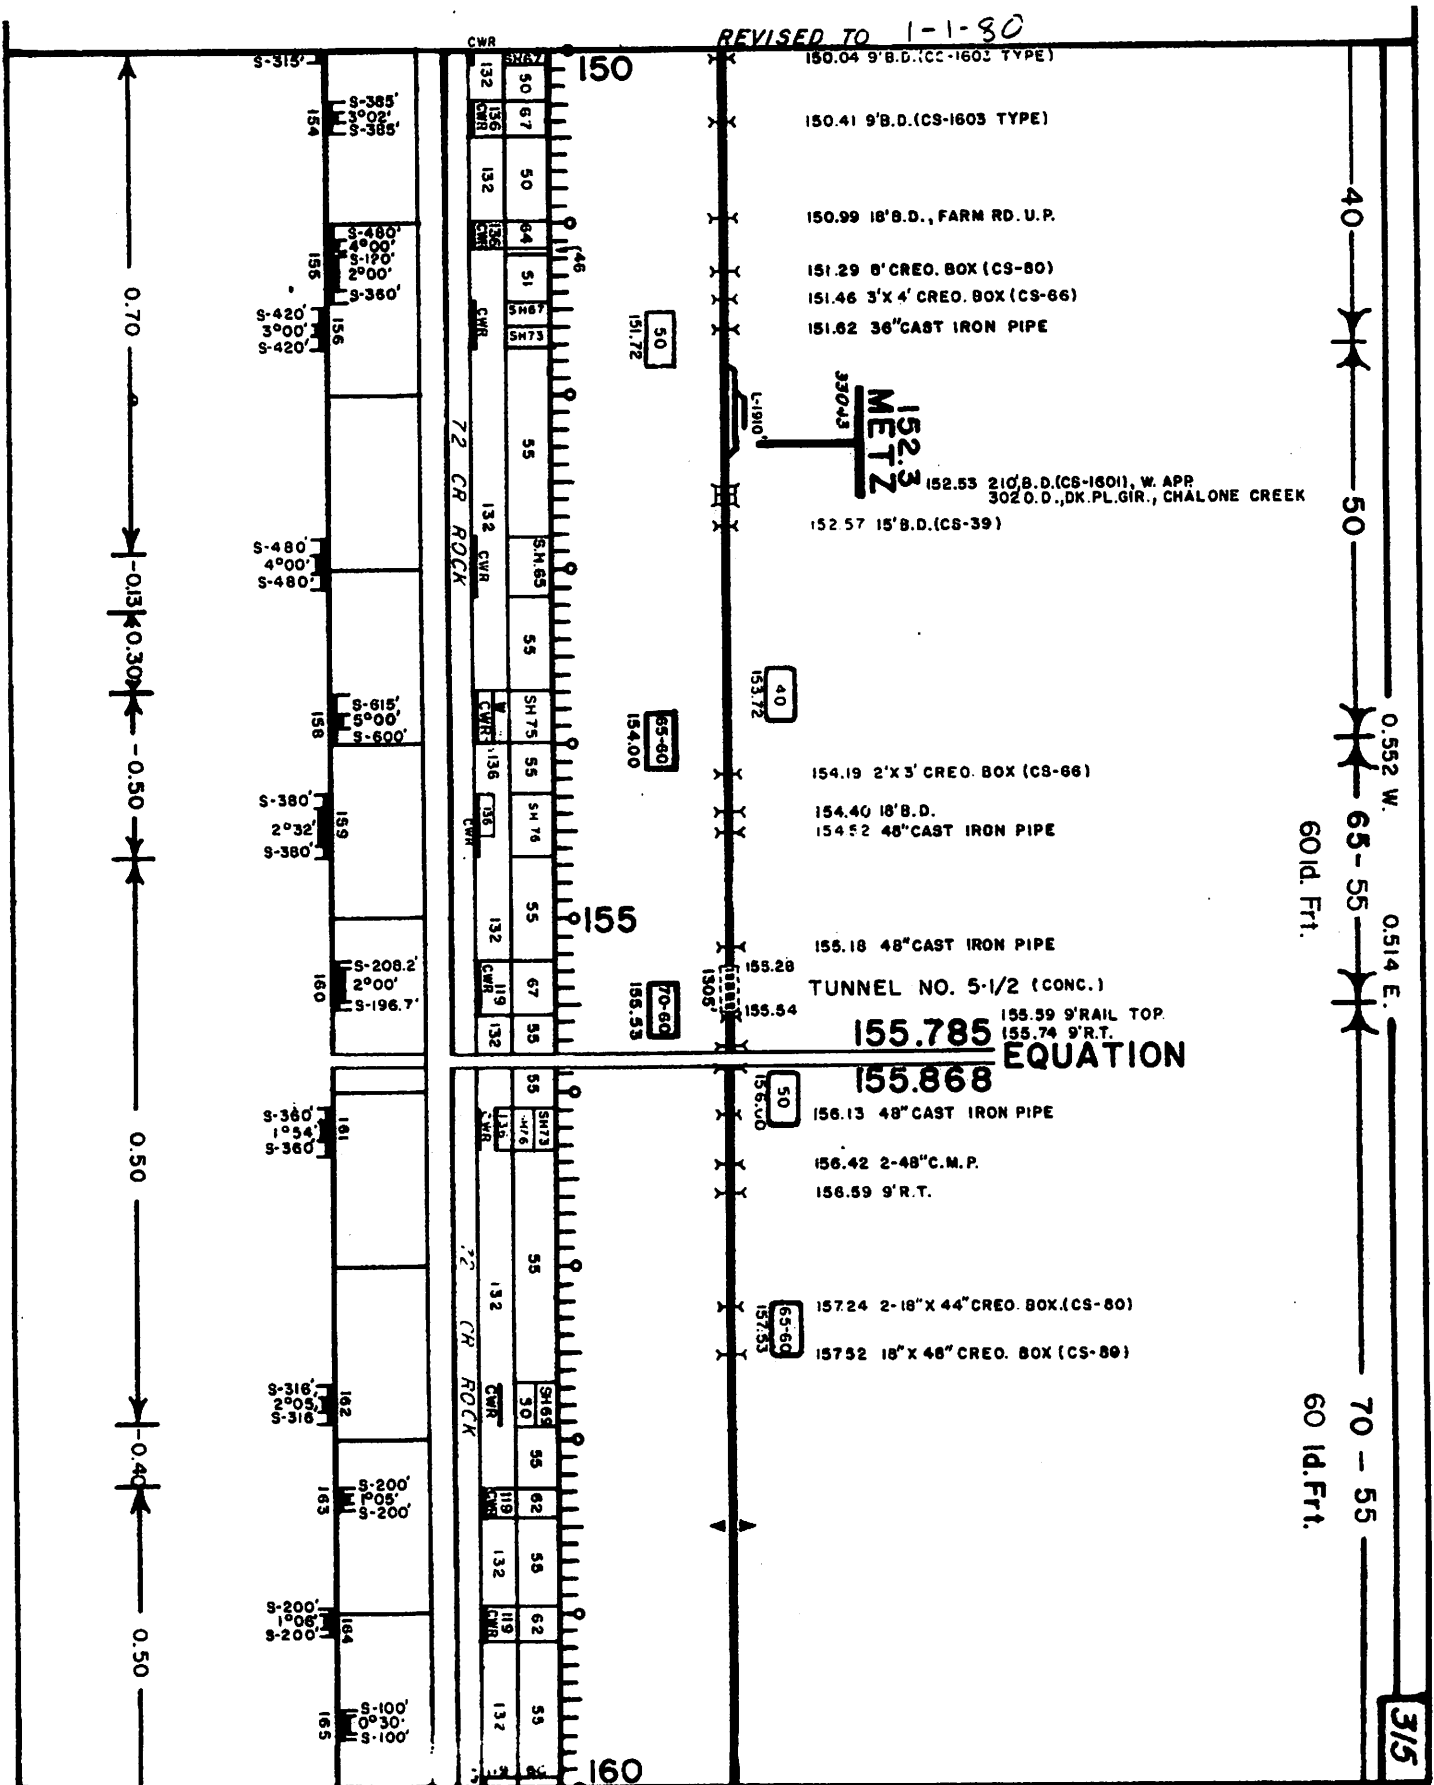

REVISED TO 1--30

0.460 W. 0.689 E.

70-55

601d.Frt.

3/7

40
170.80

170.90 13'B.D. (MW-662)

172.4
SAN LUCAS
3311

172.75 HWY U.P. (ROUTE 198)
172.85 8' STONE ARCH

L-4973'

176.66 9' RAIL TOP

177.11 2-16" X 48" CREO. BOXES (CS-60)

178.02 16' B.D. (CS-341)

178.60 3' X 4' CREO. BOX (CS-66A)
178.62 3' X 4' CREO. BOX (CS-66A)

HOT BOX DETECTOR

178.99 8' CONC. ARCH

170

175

180

33 C. ROCK

CWR

S-240'

S-240'

S-300'

S-300'

S-350'

S-350'

S-350'

S-350'

S-375'

S-375'

S-375'

S-375'

S-300'

S-300'

±0.70

0.65

-0.70

0.70

±0.70

0.70

-0.70

REVISED TO 1-1-80

70-55
60 Id. Frt.

0.460 W.

0.669 E.

60-55
60 Id. Frt.

55

3/8

180.87 11' RAIL TOP

181.35 27" X 43" C.M.P. ARCH

182.9
SAN ARDO
35/25

183.10 15' B.D., DK. PL. GIR., SAN BERNARDO CR.

L-3780'

60
183.50

70-60
185.50

186.04 6' CONC. ARCH

55
186.17

187.32 15' B.D. (CS-378)

60
188.17

188.15 12' O.D., DK. PL. GIR., SARGENTS CREEK

188.55 20" PIPE LINE CONDUIT

188.75 36" CAST IRON PIPE

189.7
WUNPOST
35/31

189.18 4' STONE ARCH

189.38 15' B.D. (CS-378)

189.96 15' B.D. (CS-39)

L-4700'

180

185

190

73 C.R.

67 C.R.

73 C.R.

67 C.R. ROCKWELL

181 182 183 184 185 186 187 188 189 190 191
S-300' S-100' S-100' S-100' S-100' S-100' S-100' S-100' S-100' S-100' S-360'

0.70 -0.25 0.65 -0.70 0.70 0.70 0.70 0.70

REVISED T 1-1-80

3/9

0.460 W.

0.689 E.

55

30

70-55
60 Id. Ft.

60-55

70-55
60 Id. Ft.

190.41 36" CONC. PIPE
190.60 36" CAST IRON PIPE

191.23 13' 8" D (MW-662)
191.34 6" RAIL TOP
191.60 16' 8" D (CS-1600 TYPE)
191.85 20' 0" D, OK PL GIR

192.15 4' CONC ARCH
192.52 7' R.T.
192.88 7' R.T.
193.01 7' R.T.
193.11 30" B.D. (CS-1601)
193.19 7' R.T.
193.36 7' R.T.

193.62 7' R.T.
193.78 7' R.T.
193.85 7' R.T.
194.00 8' 8" D (CS-1605)

194.63 6' CONC. & BRICK ARCH

195.05 7' R.T.
195.49 7' R.T.

195.9
BRADLEY
196.24 6' STONE ARCH

197.09 18' B.D., I BEAMS, COUNTY RD. U.P.

197.72 8' R.T.
197.91 8' STONE ARCH

198.61 6' STONE ARCH

199.07 10' R.T.

199.36 8' BRICK & CONC ARCH

30
191.70

70-60
194.35

60
195.43

30
196.35

70-60
197.45

70-60
197.80 198.10

60
199.80

190

195

200


67 CR ROCK

66 C.R. 67 C.R.

64 C.R.

67 CR. ROCK

74 C.R.

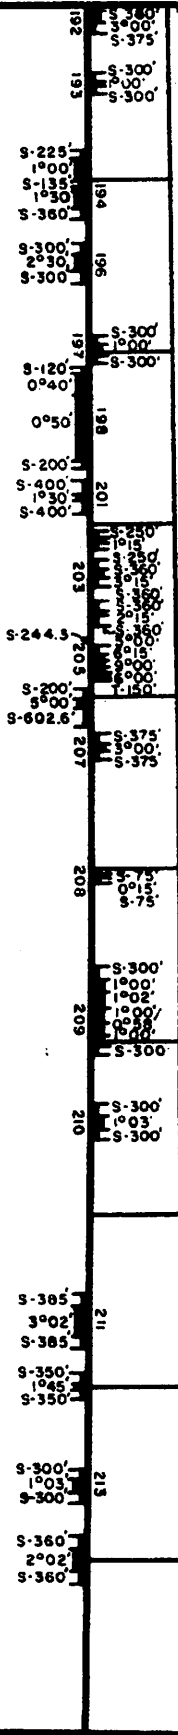



REVISED TO 1-1-80

60-55
60 Id. Ft.

150

60-55
60 Id. Ft.

0.660 W.

0.689 E.

40

321

WELLSONA
210.9
33/86

210.65 4' CONC. ARCH
210.84 9' B.D. (CS-1600 TYPE)
211.25 6' STONE ARCH

212.04 36" CAST IRON PIPE

212.66 20' B.D. (CE-18225), RD. U.P.

213.19 6' CONC. & BRICK ARCH

213.69 6' CONC. & BRICK ARCH

214.05 48" CONC. PIPE
214.06 & 214.08 HIWAY OVERPASSES

215.09 24 TH. STREET O.P.
215.21 4' CONC. ARCH
215.33 9' RAIL TOP

PASO ROBLES
216.3
35/70

215.86 7' R.T.
215.90 36" CONC. PIPE
215.95 36" C.M.P.

216.03 7' R.T.

216.59 20' B.D. (CS-369), 3RD. ST. U.P.

216.92 HIWAY O.P.
216.97 HIWAY O.P.
217.06 60" C.M.P.
217.16 36" CAST IRON PIPE

217.67 7' R.T.

218.03 7' R.T. 218.00

218.22 8' R.T.
218.29 7' R.T.

218.60 6' CONC. ARCH

219.49 6' STONE & CONC. ARCH

219.80 9' R.T.


210

215

220

0.63
0.60
0.58
±0.32
0.70
0.70
0.66
±0.59
±0.70

REVISED TO 1-1-80

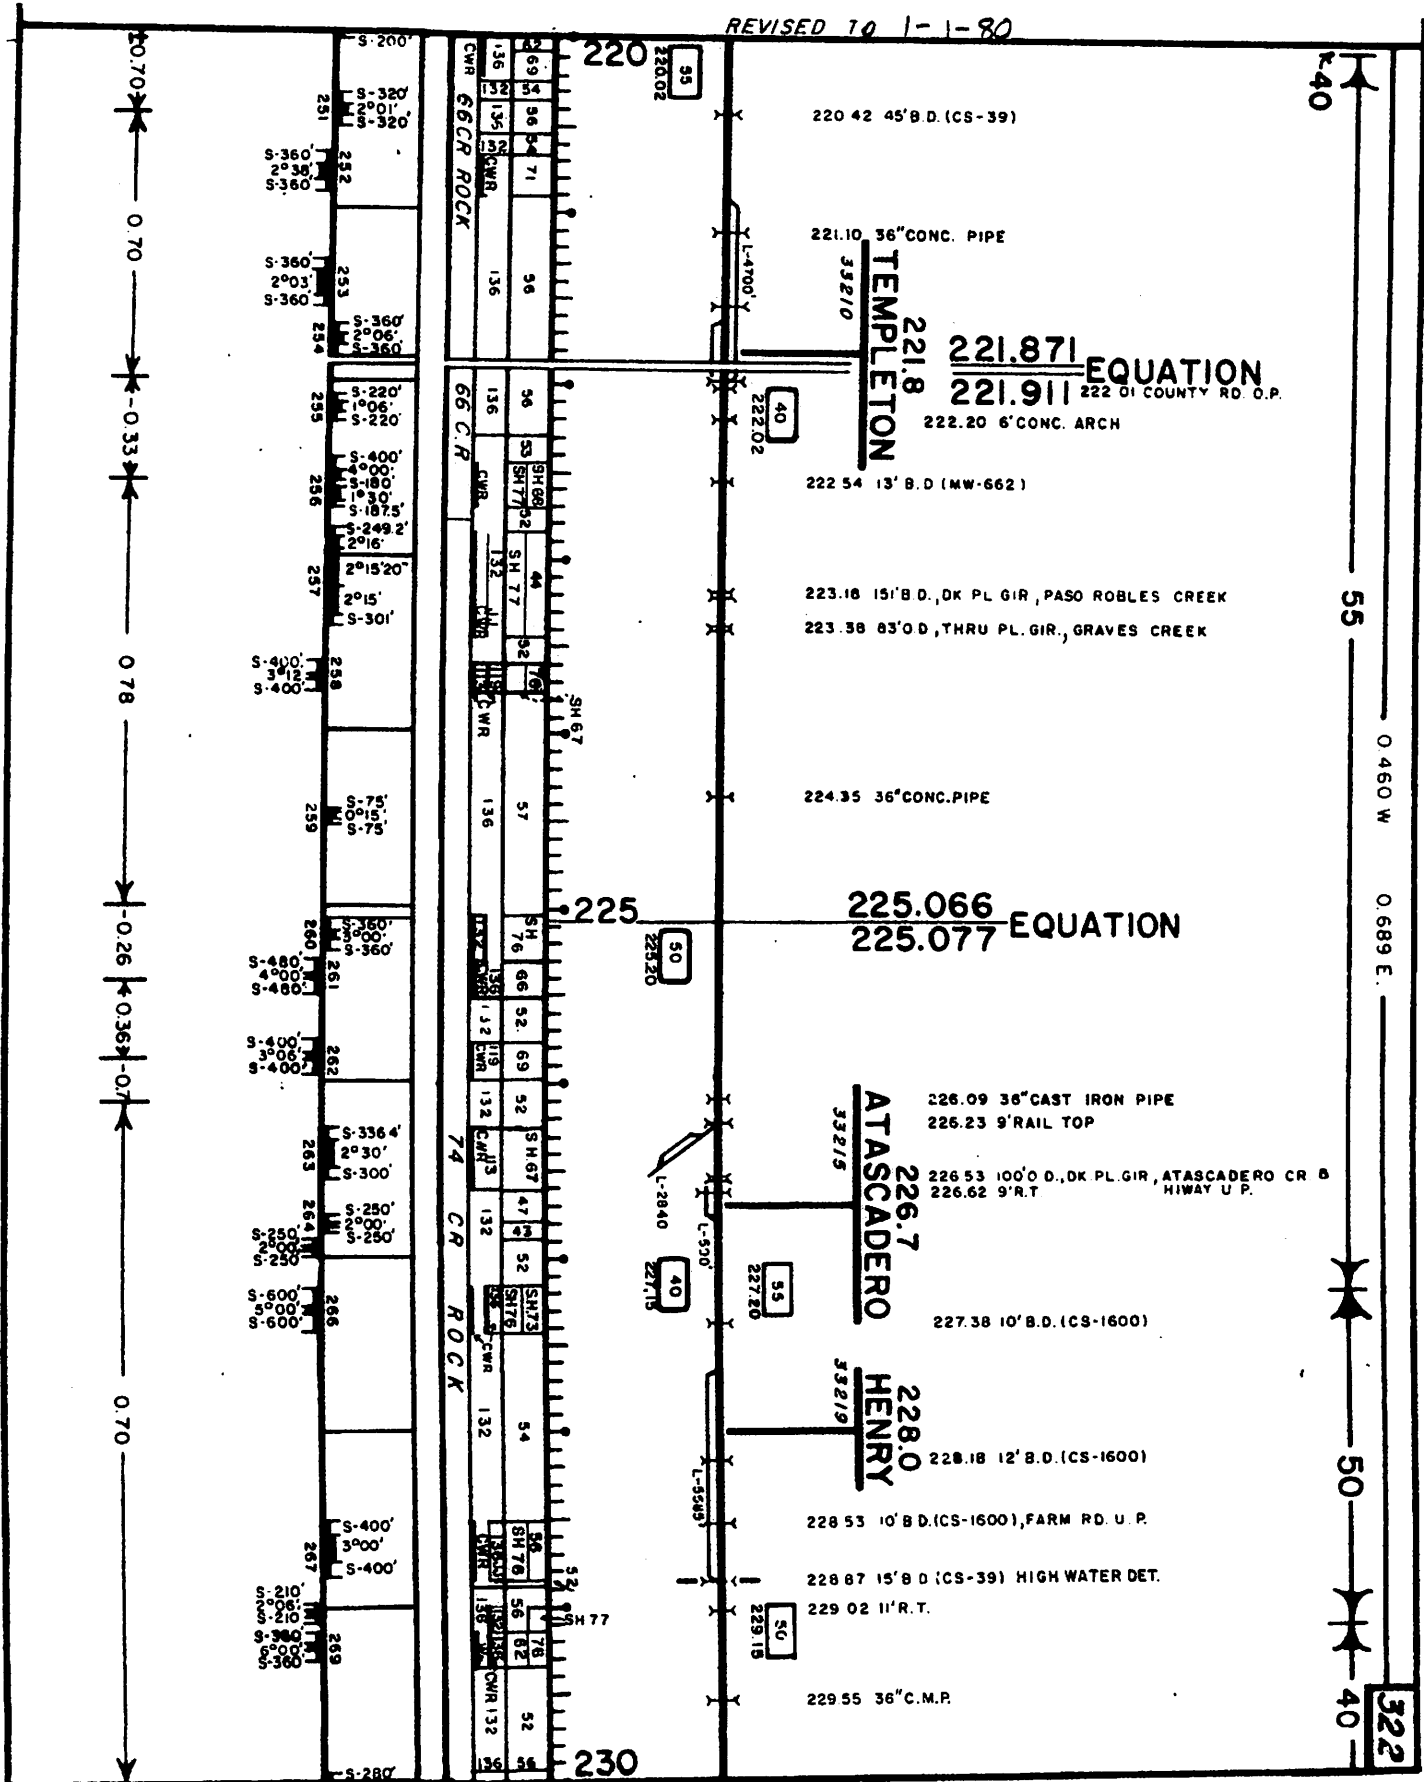

REVISED TO: 1-1-80

230.03 20' B.D. RD U.P.

40
60-55
60 ft. Ft.

0.460 W 0.689 E

35
35
2.2 W. 2.2 E.
25

323

230.822 EQ.
230.841

230.50 9' B.D. (CS-1600)

231.40 6' CONC ARCH

231.75 16' B.D. (CS-1601 TYPE)

232.30 103' O.D., THRU RIV SPANS, SANTA MARGARITA CR.

230

232.50

235

240

74 CR
ROCK

66 C.R. CR

SANTA MARGARITA
235.5

CUESTA
238.9

234.39 13' R.T.
234.47 3-17" X 48" CREO. BOXES (CS-80)
234.54 3-17" X 48" CREO. BOXES (CS-80)
234.62 13' R.T.
234.72 13' R.T.
234.83 9' RAIL TOP
234.95 13' R.T.

235.14 13' R.T.
235.22 45' B.D. (CS-39)
235.45 11' R.T.
235.67 15' B.D. (CS-39)

236.18 15' R.T.
236.41 15' B.D. (CS-1601)

236.53 4' STONE ARCH
236.55 4' STONE ARCH
236.56 4' STONE ARCH

236.92 4' STONE ARCH

237.14 11' R.T.

237.30 6' STONE ARCH
237.44 4' STONE ARCH
237.55 15' B.D. (CS-39)

237.72 4' STONE ARCH

237.94 4' STONE ARCH
238.12 36" C.M.P.
238.15 11' R.T.

238.30 11' R.T.
238.60 11' R.T.
238.76 10' B.D. (CS-39)
238.99 18' B.D.
239.01 HIWAY OVERPASS

TUNNEL NO 6 (CONC.)

239.98 239.98 11' R.T.

0.74


0.20

0.70

2.20

2.2

L.C.T.C.

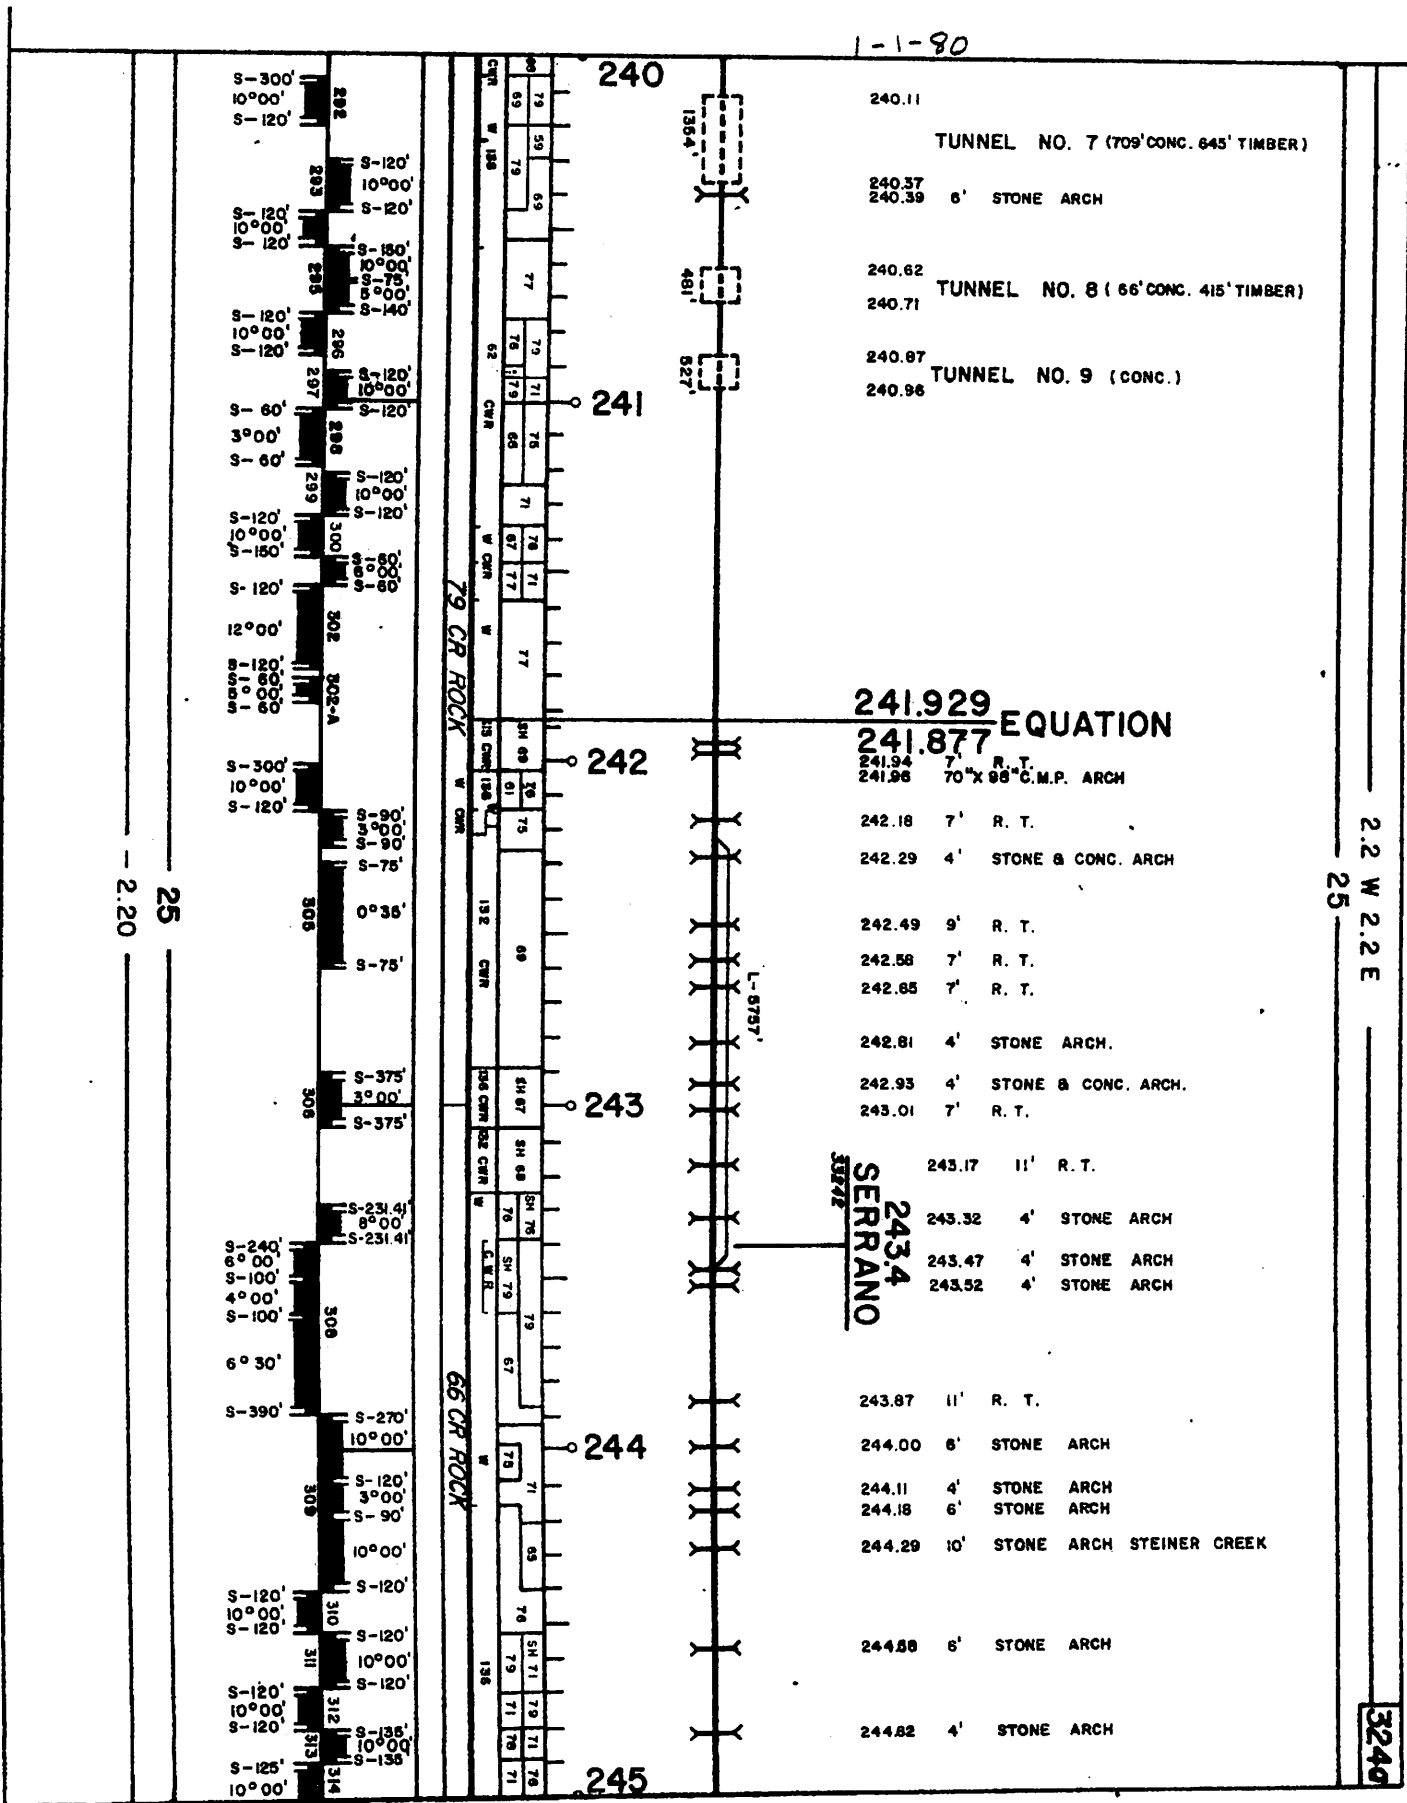

1-1-80

240.11
TUNNEL NO. 7 (709' CONC. 645' TIMBER)
240.37
240.39 6' STONE ARCH
240.62
240.71 TUNNEL NO. 8 (66' CONC. 415' TIMBER)
240.87
240.96 TUNNEL NO. 9 (CONC.)

241.929
241.877 EQUATION
241.94 7' R.T.
241.96 70" X 96" C.M.P. ARCH

242.18 7' R.T.
242.29 4' STONE & CONC. ARCH
242.49 9' R.T.
242.58 7' R.T.
242.65 7' R.T.
242.81 4' STONE ARCH.
242.93 4' STONE & CONC. ARCH.
243.01 7' R.T.

243.17 11' R.T.
243.32 4' STONE ARCH
243.47 4' STONE ARCH
243.52 4' STONE ARCH

243.87 11' R.T.
244.00 6' STONE ARCH
244.11 4' STONE ARCH
244.18 6' STONE ARCH
244.29 10' STONE ARCH STEINER CREEK
244.68 6' STONE ARCH
244.82 4' STONE ARCH

2.2 W 2.2 E

3246

324b

245.15 4' STONE ARCH

245.2B 4' STONE ARCH

245.53 4' STONE ARCH

245.61 4' STONE ARCH

245.85

TUNNEL NO. 11 (50' CONG. 673' TIMBER)

245.99

246.3
CHORRO
33247

24759 4' STONE & CONC. ARCH

247.73 4' STONE ARCH

248.0
GOLDTREE
JUL 23 1993

248.06 4' STONE ARCH

248.21 4' STONE & CONC. ARCH

248.36 931' OD. DK. PL. GIR. STEINER CREEK

248.69 4' STONE ARCH

248.89 11' R. T.

249.09 6' STONE ARCH


249.16 10' R.T.

249.40 6' STONE & CONC ARCH

249.57 6' STONE & CONC ARCH

249.70 18' 8.0.

249.97 85' B.D. THRU P.L. GIR. BRIZZIOLARI CK. @ RD. U.P.

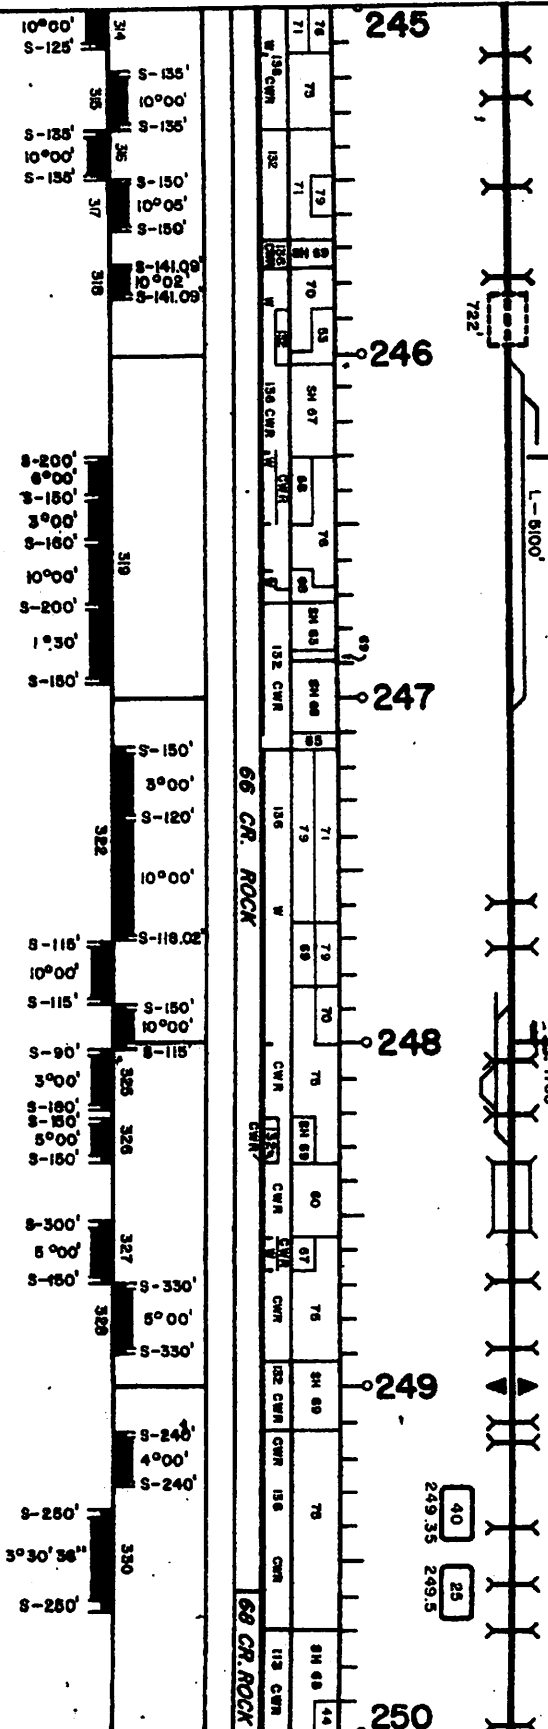

PASO ROBLES DISTRICT — A. V. NOVOA

-A. V. NOVOA

D.M.M.

WESTERN DIVISION

LOS ANGELES DIVISION


-2.20


256


249.7


to

REVISED TO: JAN 15, 1980

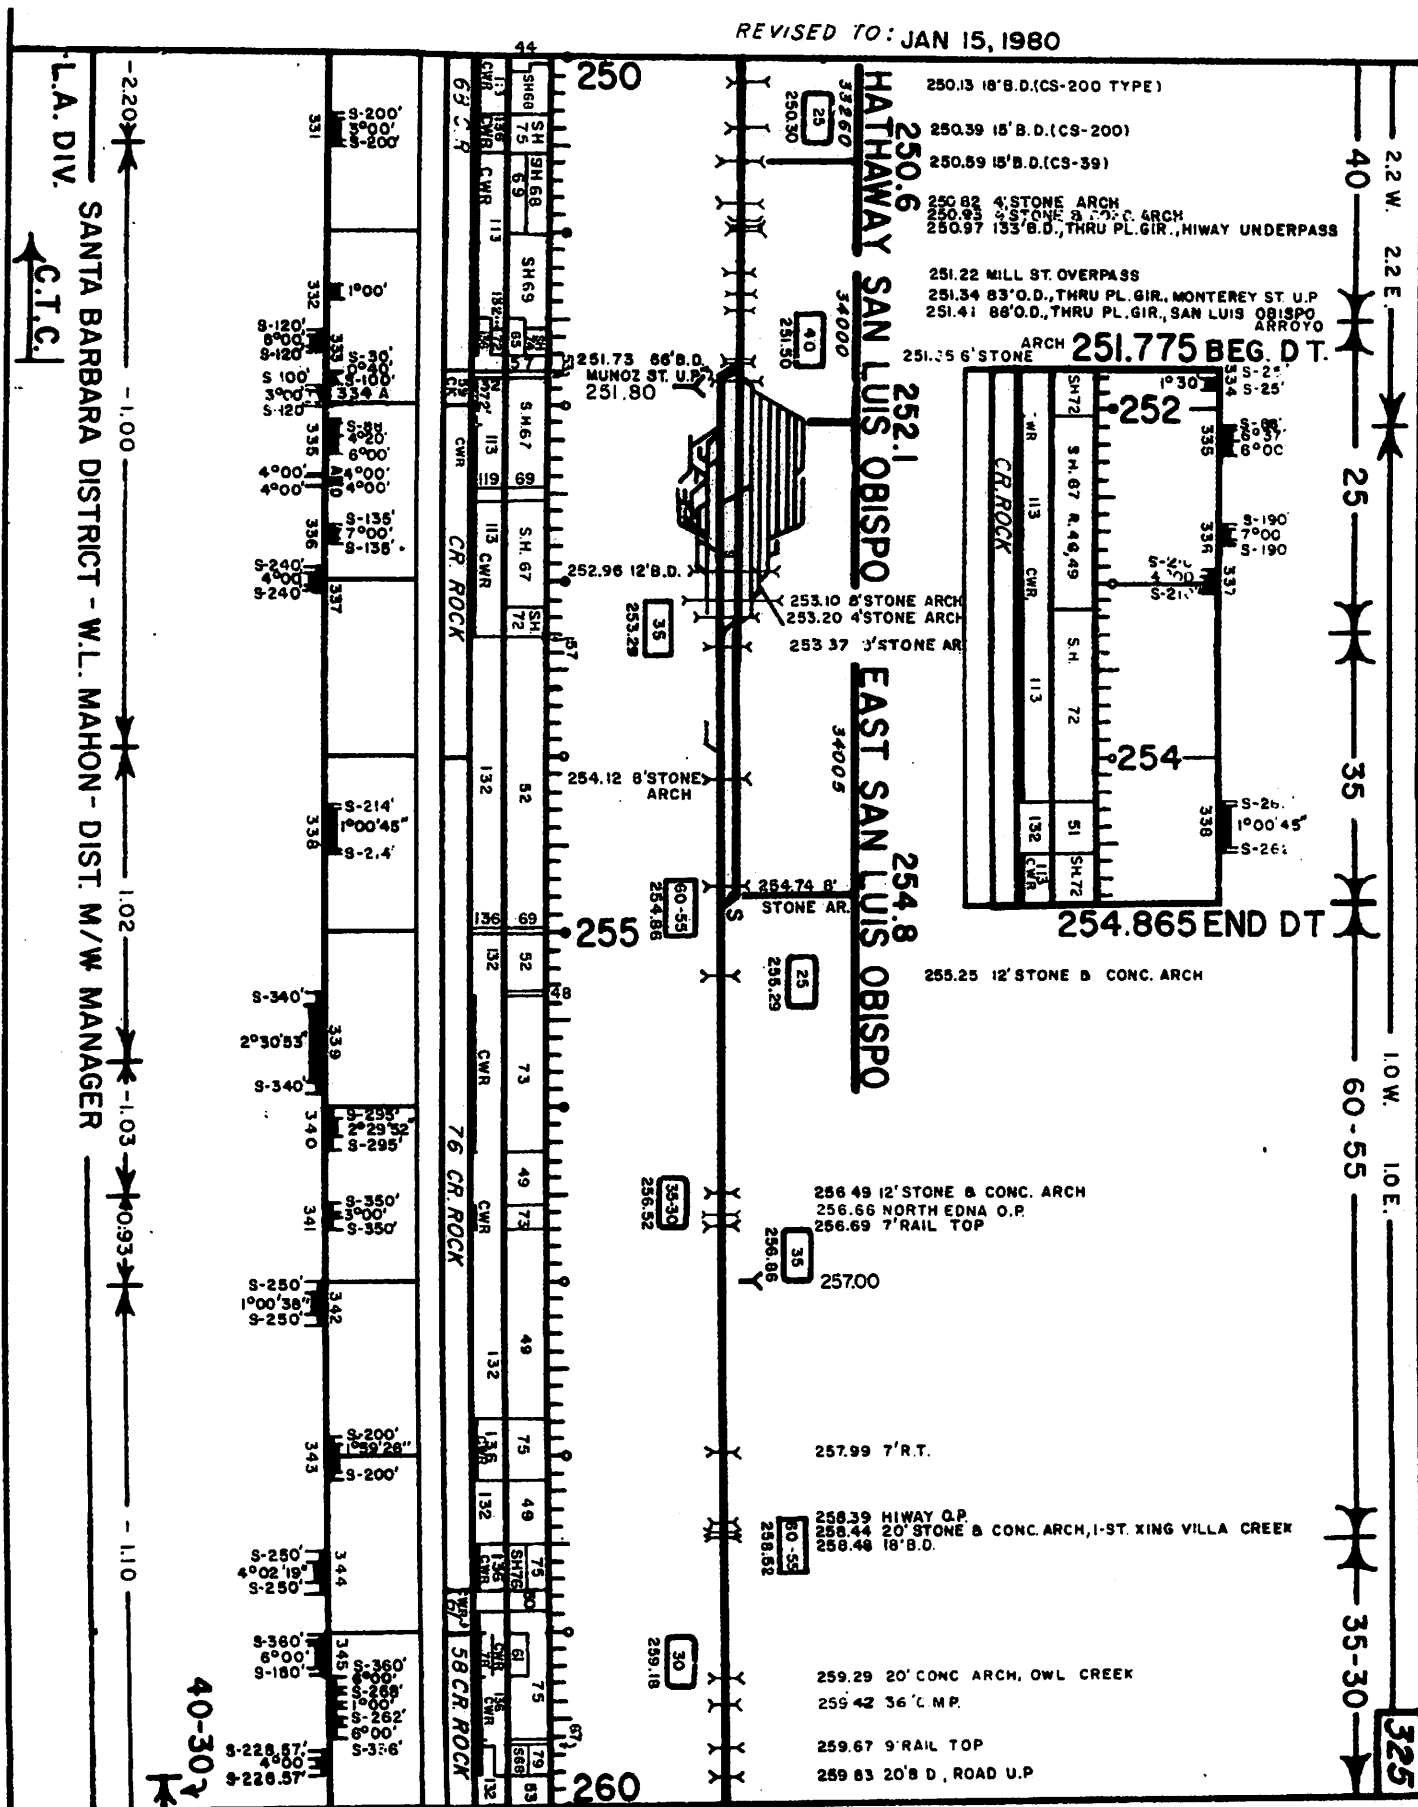


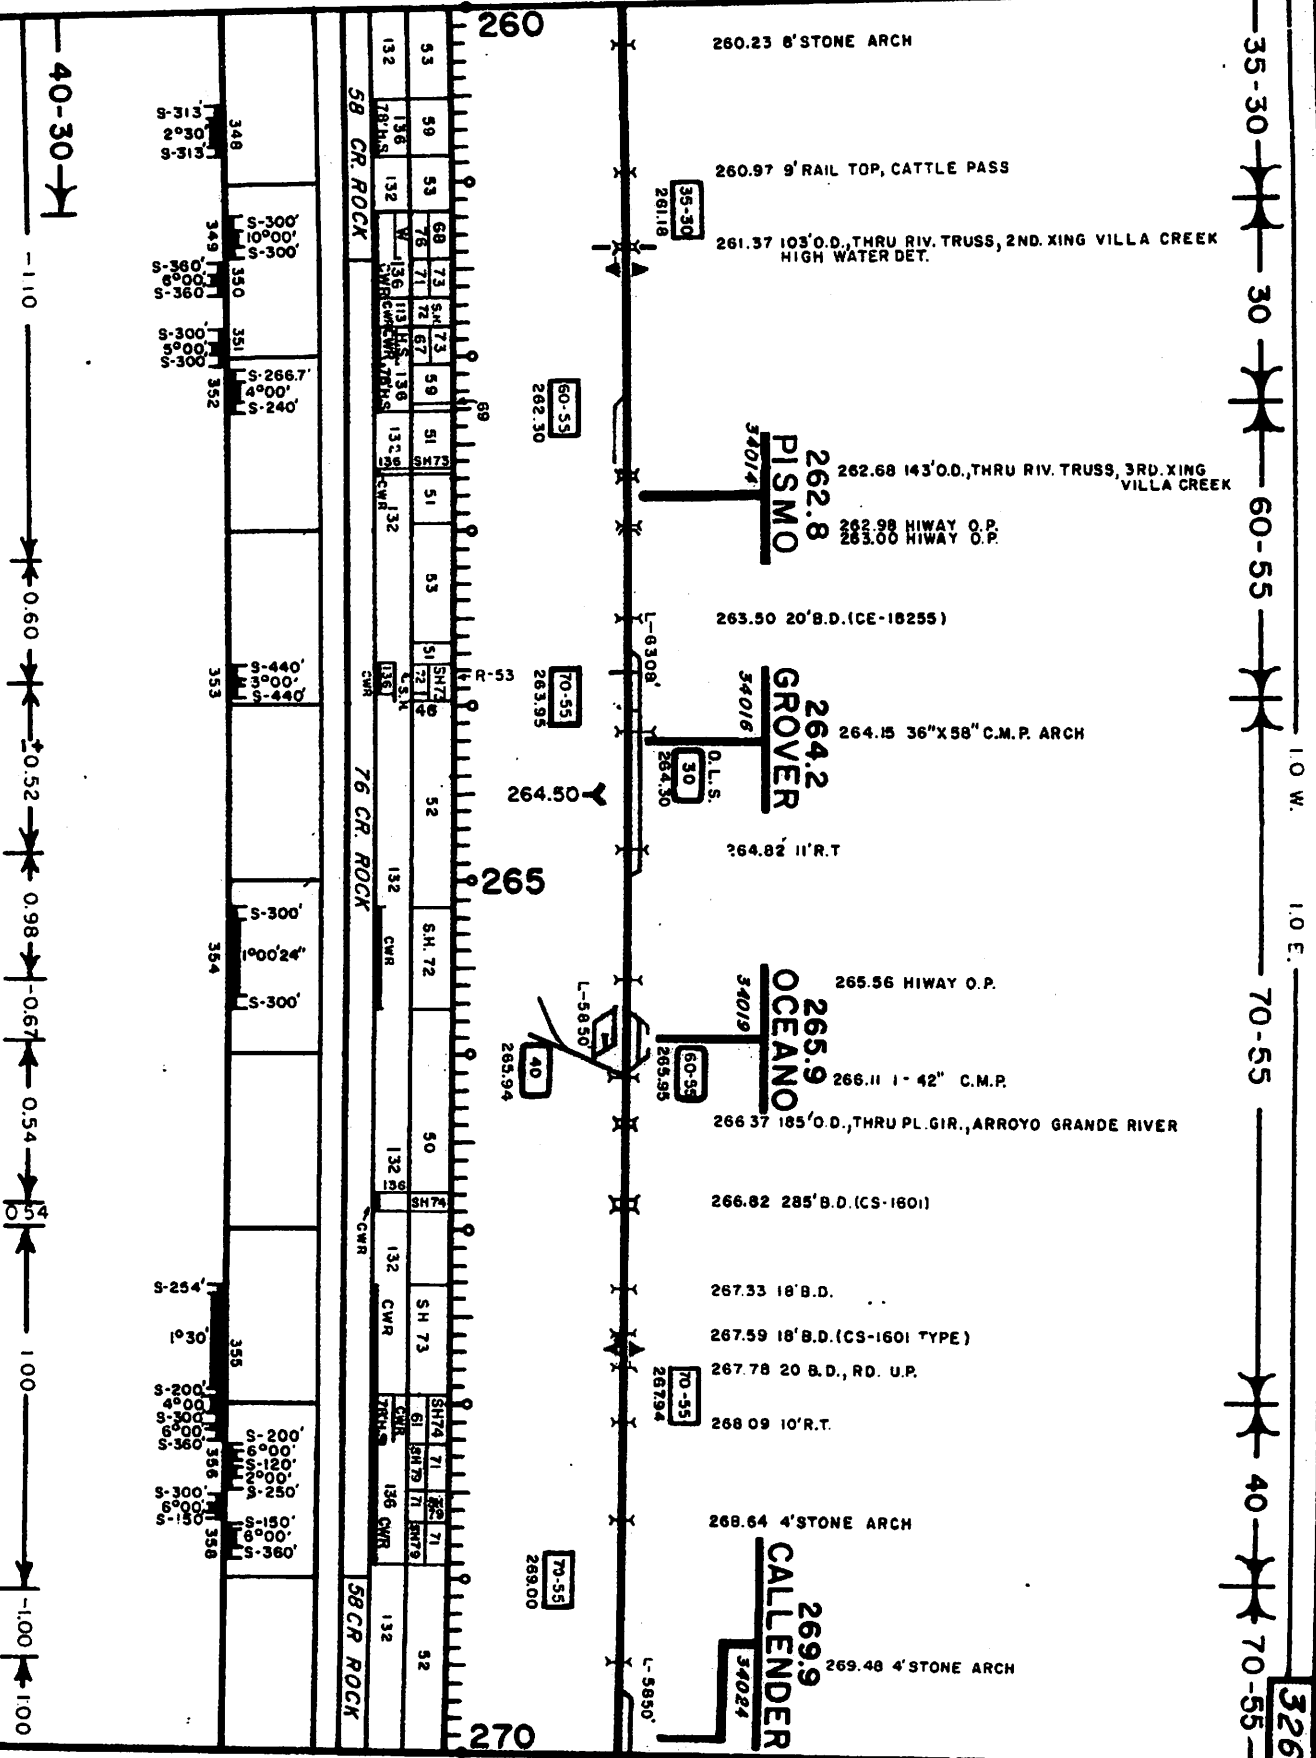

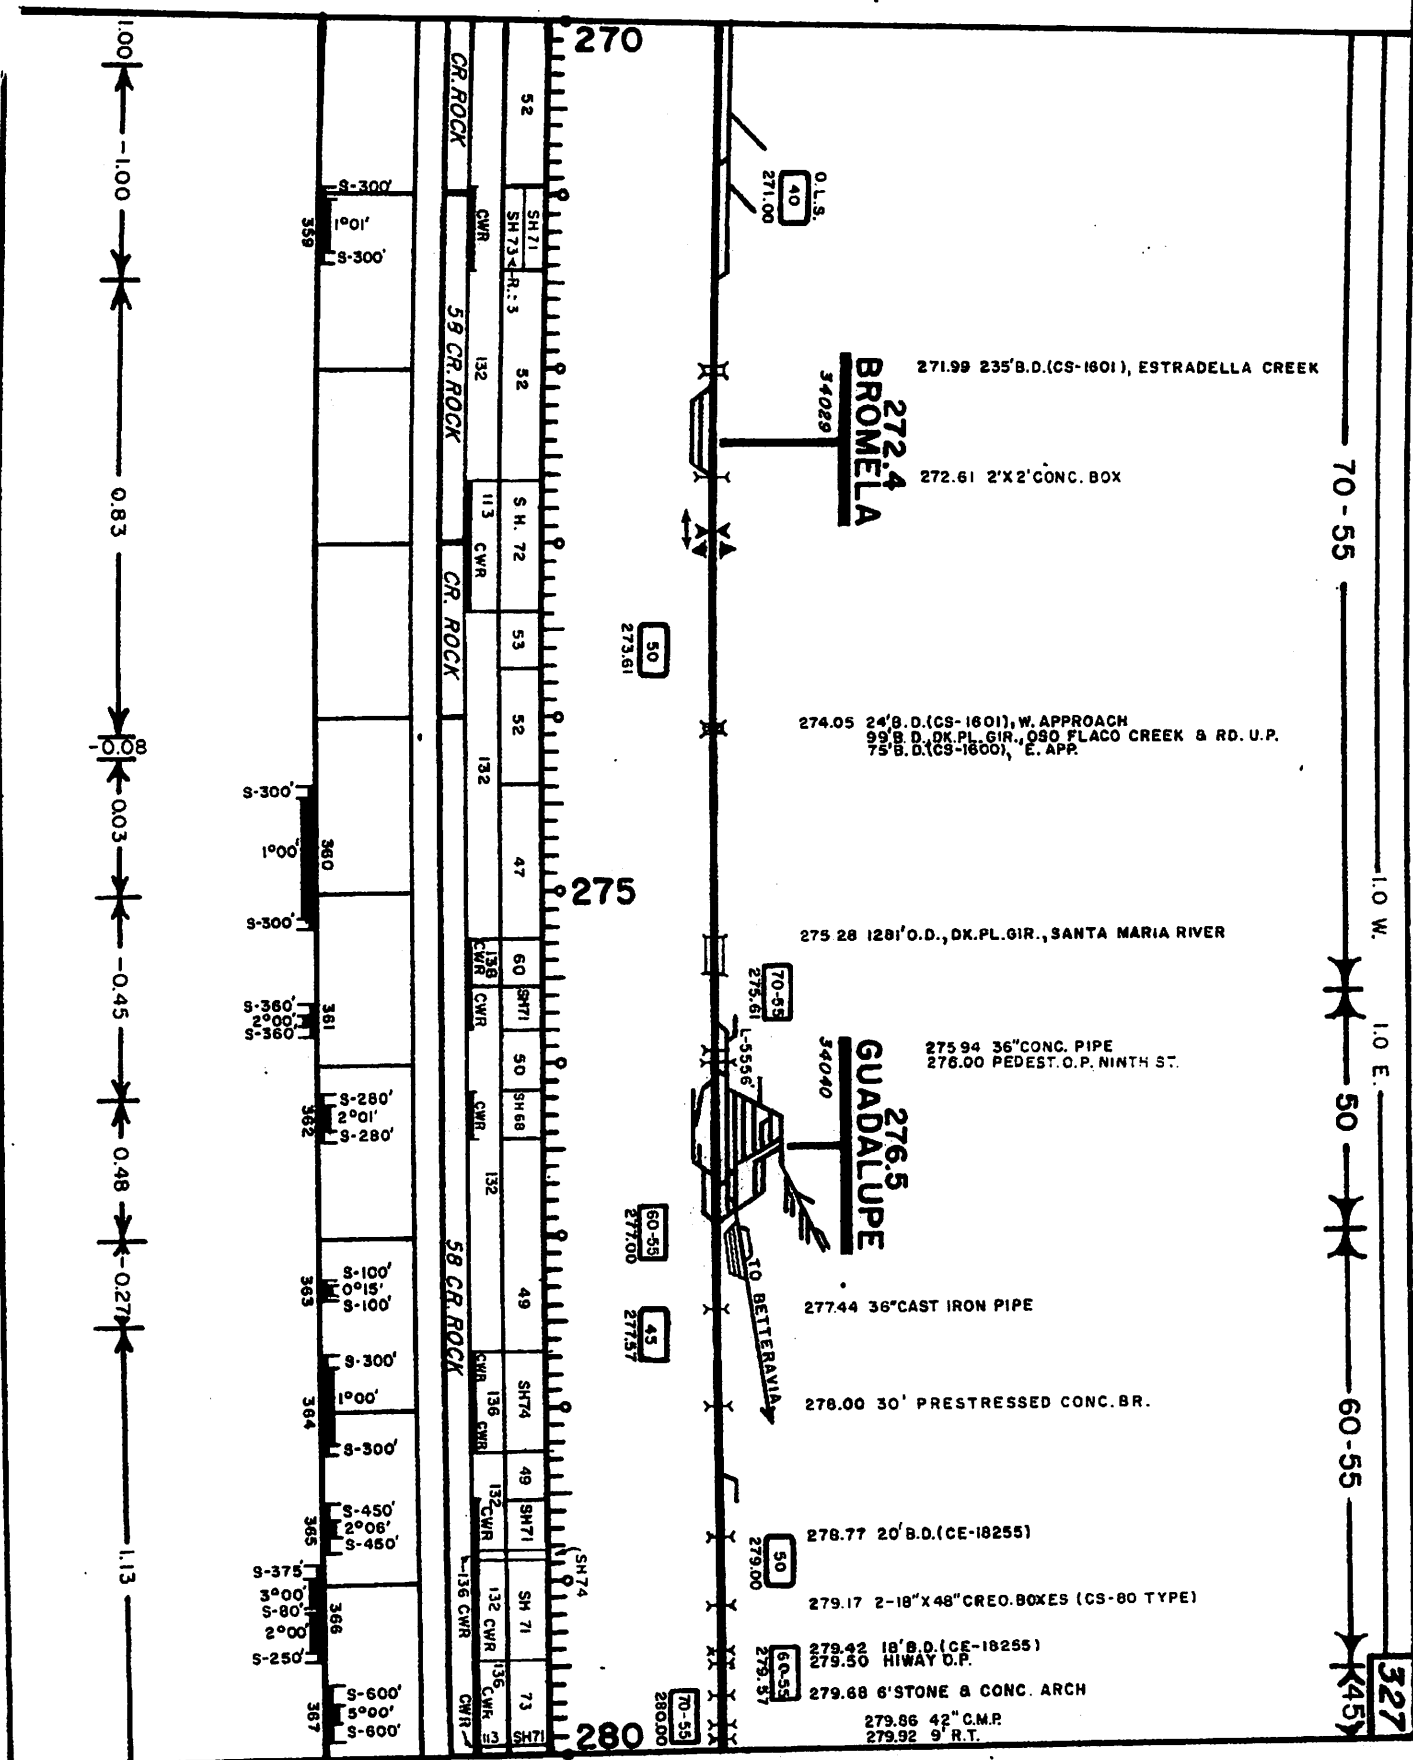


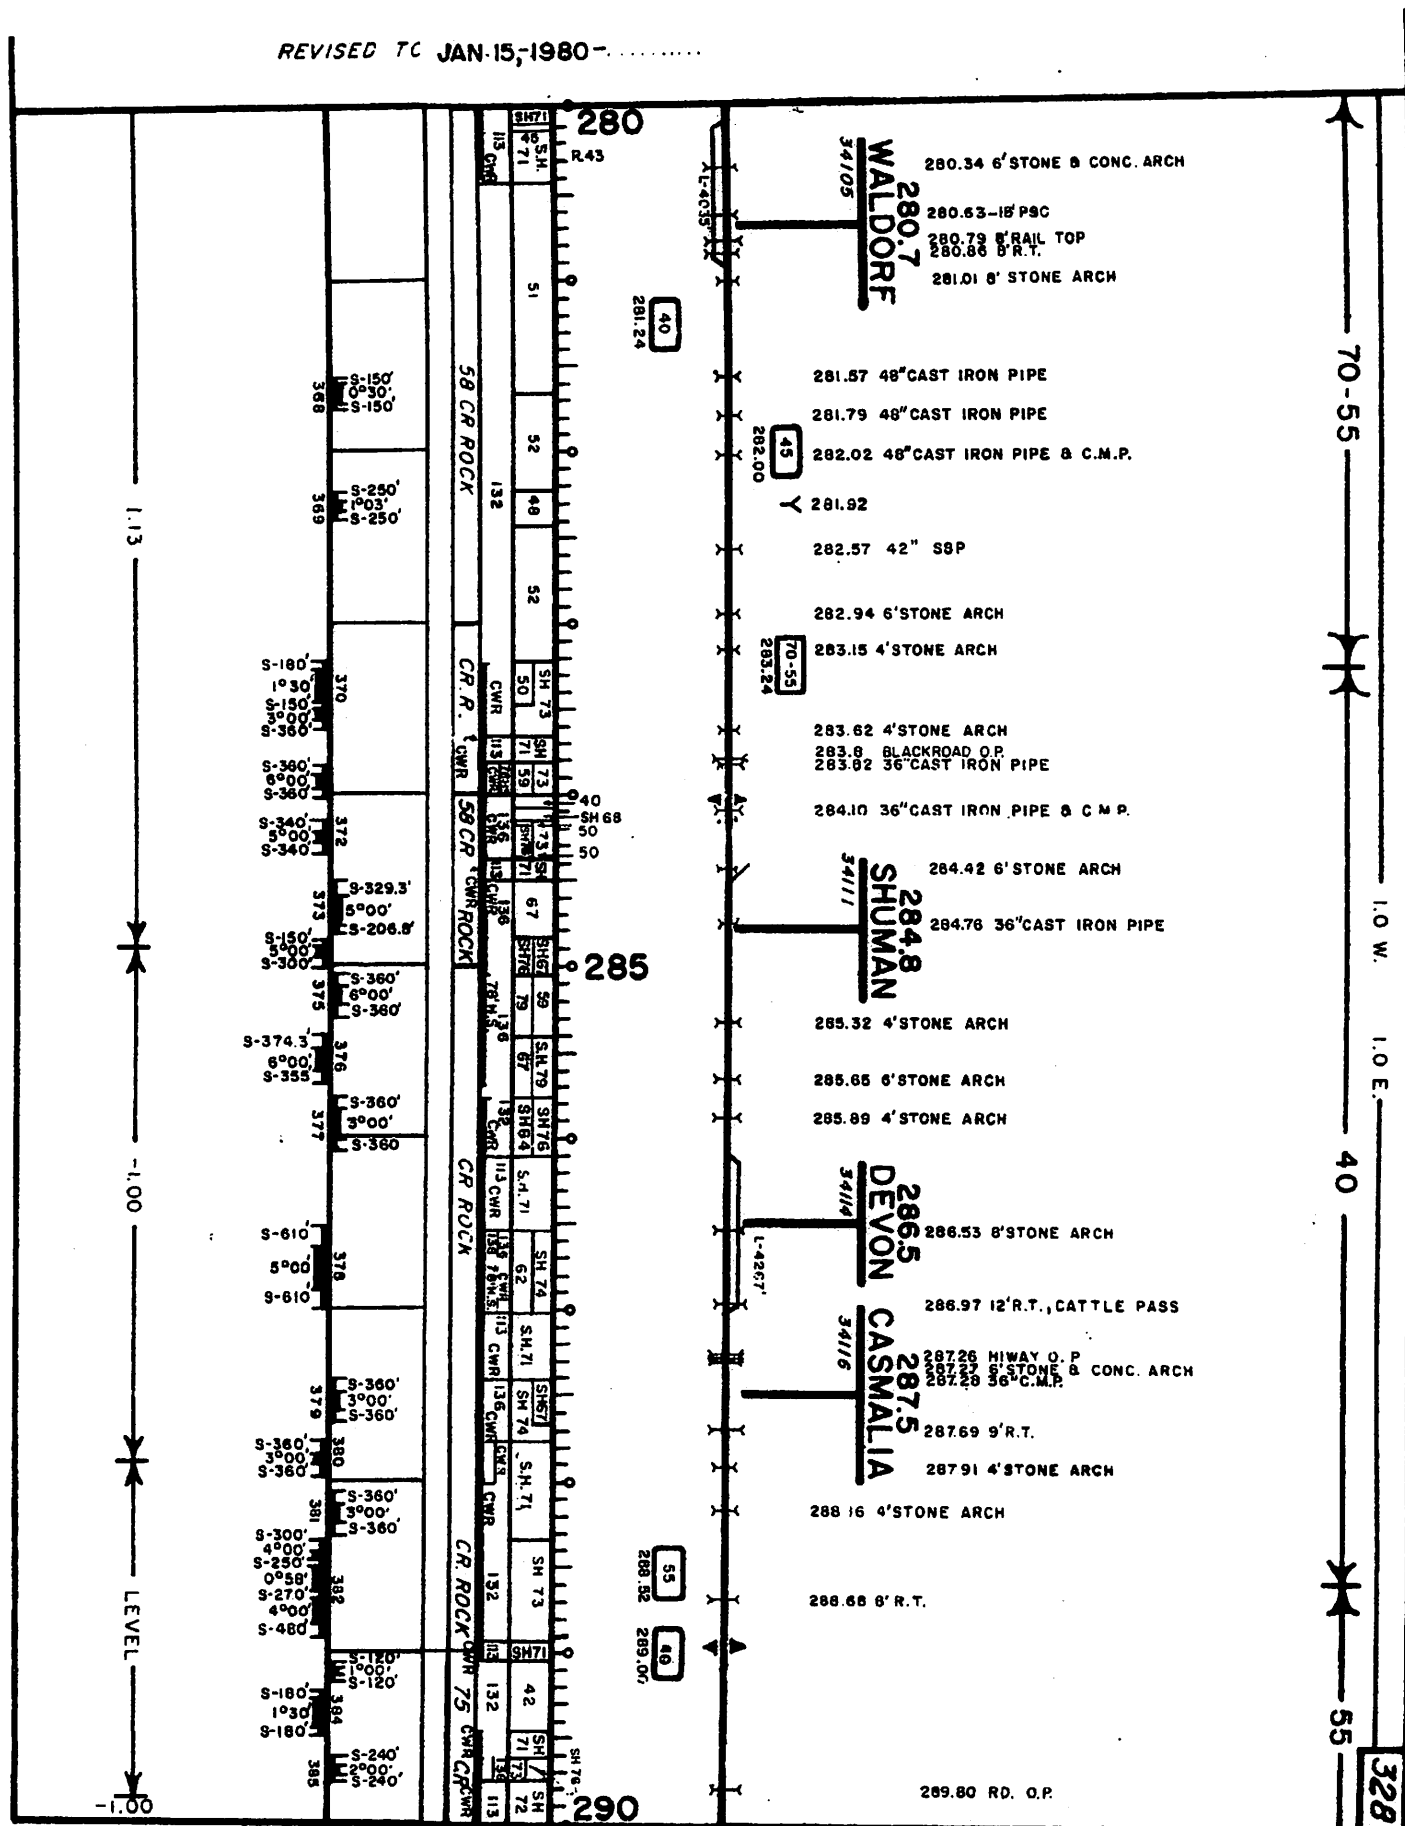

REVISED TO JAN - 15 - 1980

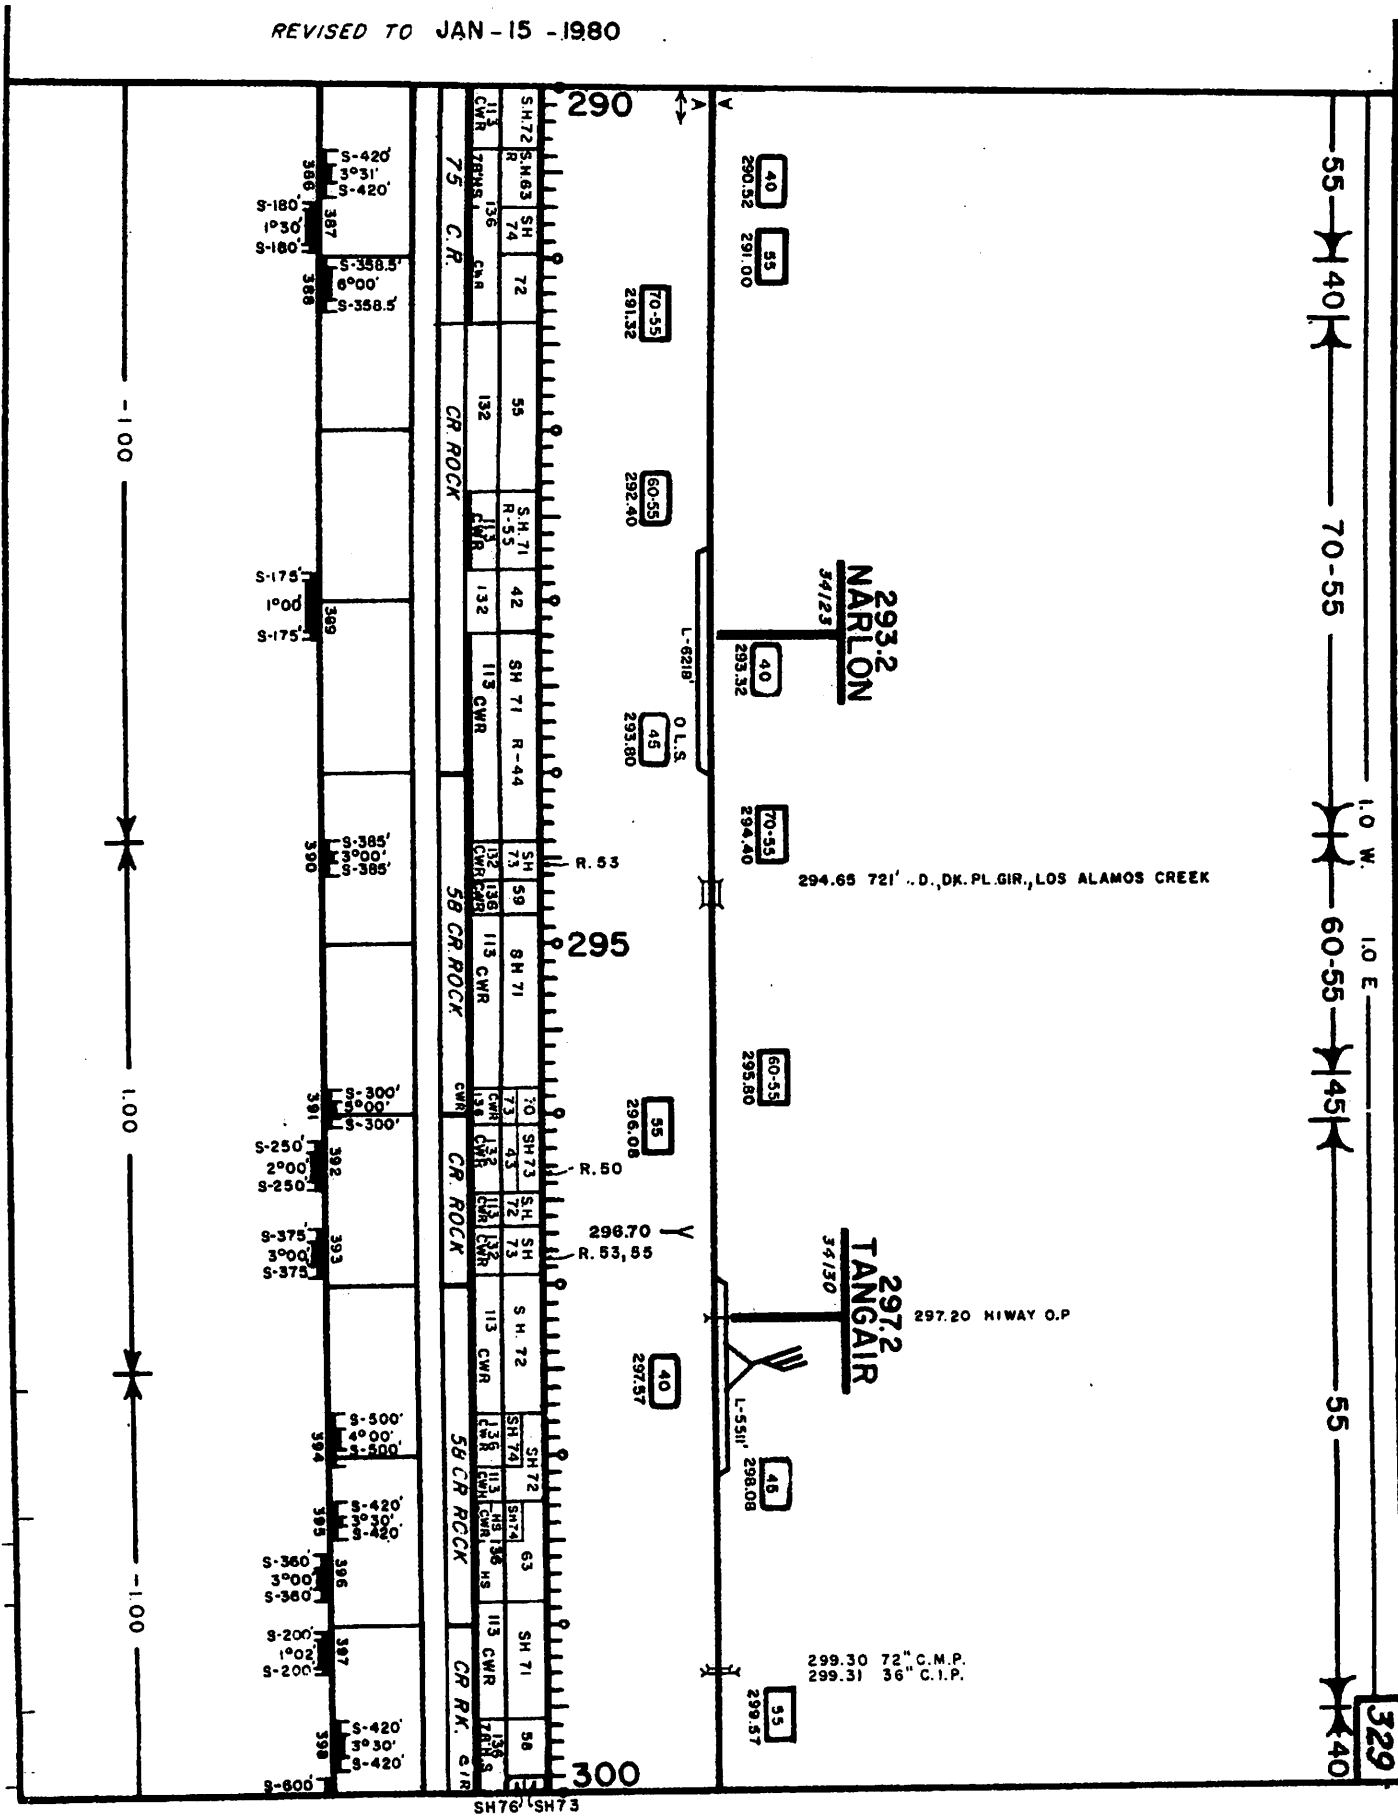


REVISED TO JAN. 15, 1980

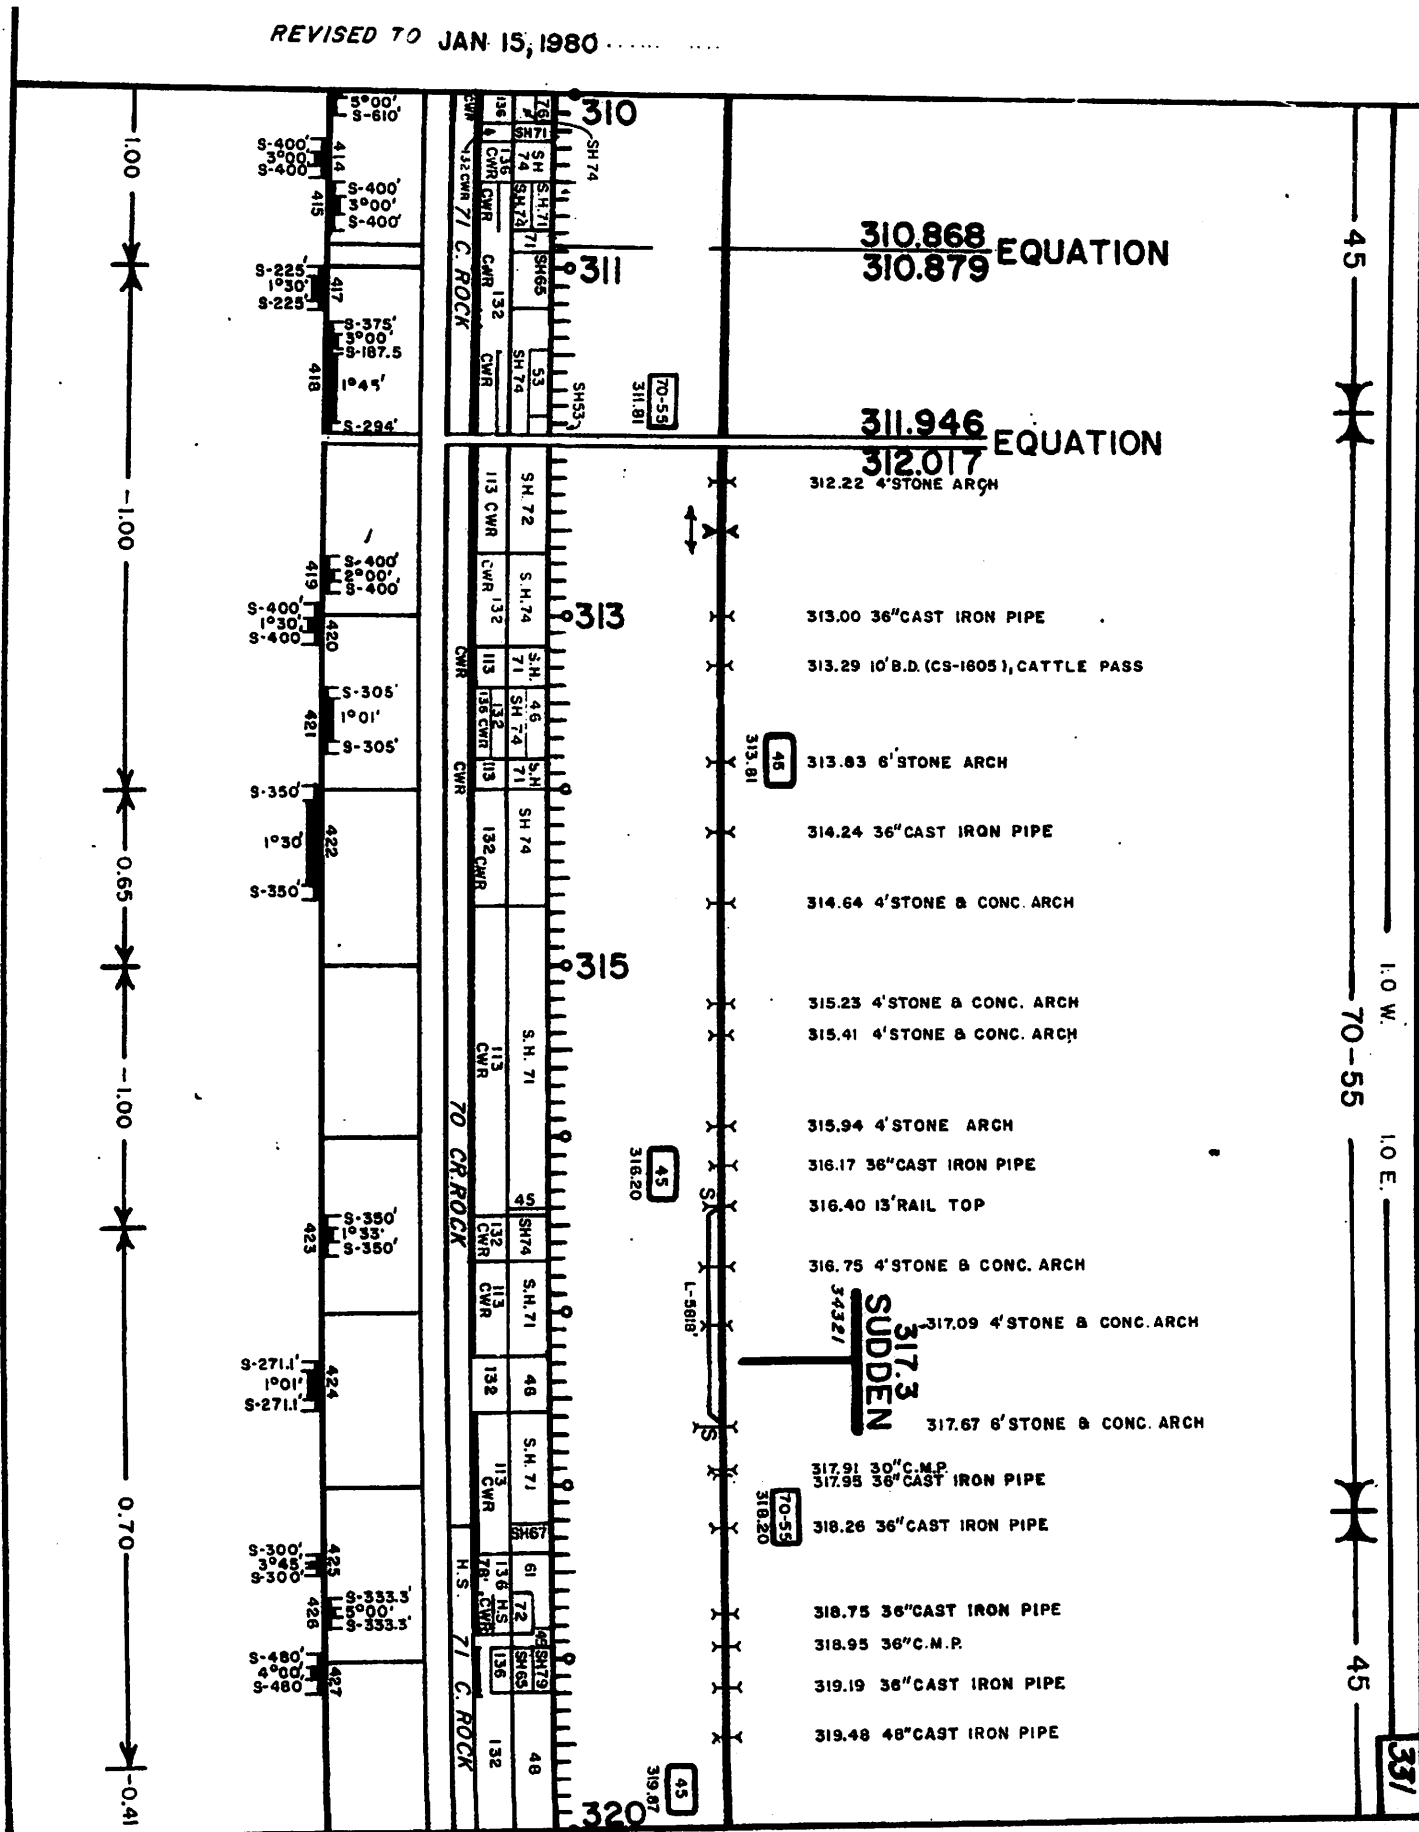


REVISED TO JAN - 15 - 1980.

Station	Description	Elevation
320.32	45' O.D., DK. PL. GIR., JALAMA CAÑON	
321.02	36" CAST IRON PIPE & CONC. PIPE	
321.36	48" CAST IRON PIPE & 36" CONC. PIPE	
321.84	9' RAIL TOP	
322.00	4' STONE ARCH	
322.43	9' R.T.	
322.48	36" CAST IRON PIPE	
322.56	24" X 20" CONC. BOX	
322.82	36" C.M.P.	
322.90	4" CONC. ARCH	
323.00	4" CONC. ARCH	
323.43	6' STONE ARCH	
323.57	42" C.M.P.	
323.98	6' STONE & CONC. ARCH	
325.3	CONCEPCION	
325.36	48" C.M.P.	
325.68	2-17" X 38" CREO. BOX (CS-80 TYPE)	
325.81	13" X 22" C.M.P. ARCH	
326.01	12' STONE ARCH	
327.08	12' STONE ARCH	
327.57	10' STONE & CONC. ARCH	
327.83	4' CONC. ARCH	
328.36	4' STONE & CONC. ARCH	
328.52	36" CAST IRON PIPE	
328.72	36" CAST IRON PIPE	
329.05	36" C.M.P.	
329.51	8' STONE & CONC. ARCH	
329.69	4' STONE & CONC. ARCH	
329.97	36" C.M.P.	


REVISED TO: JAN 15, 1980

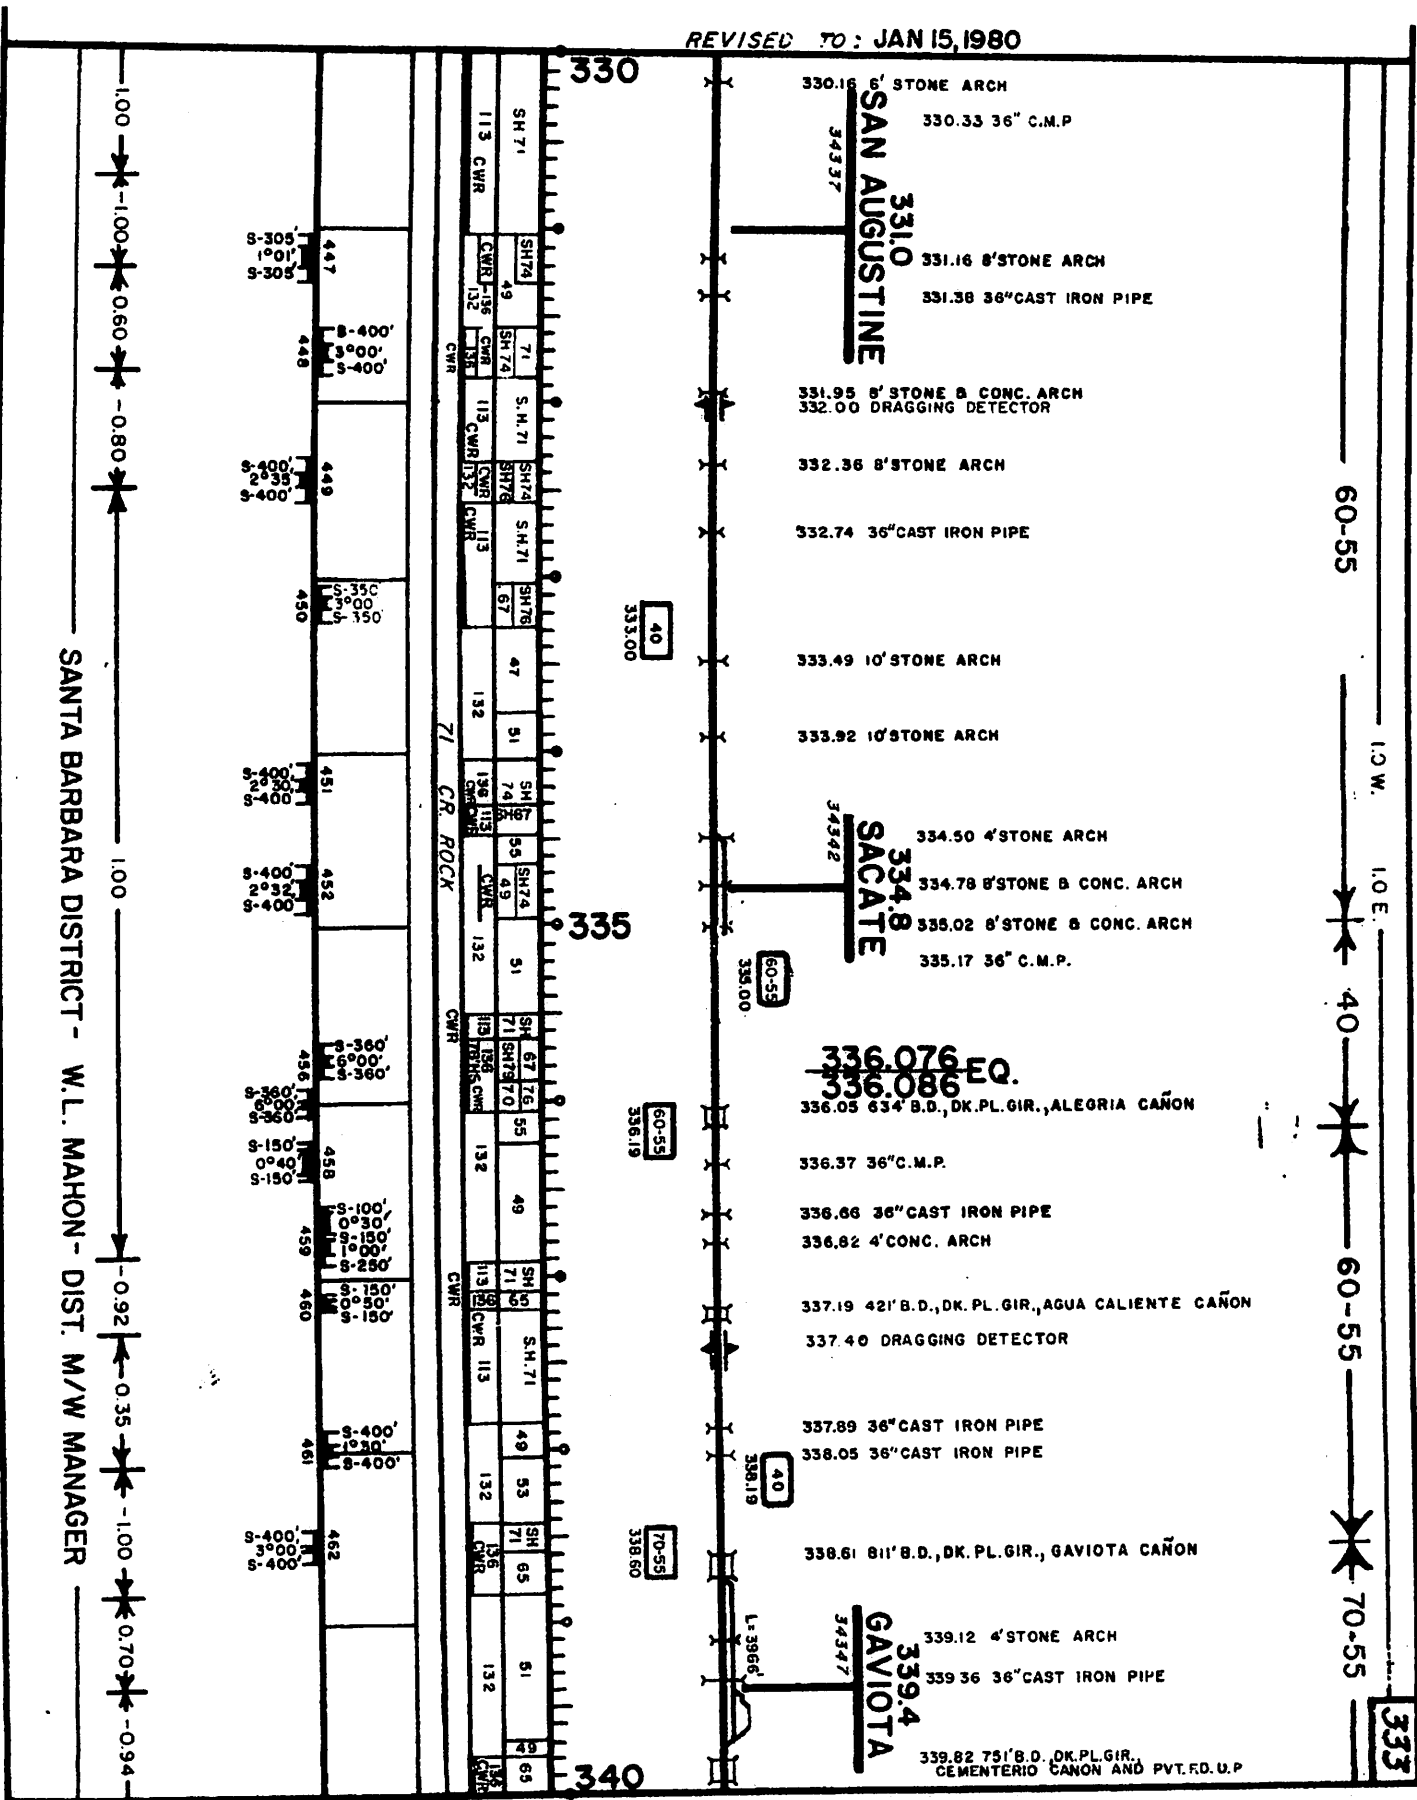


REVISED TO JAN, 15, 1980.

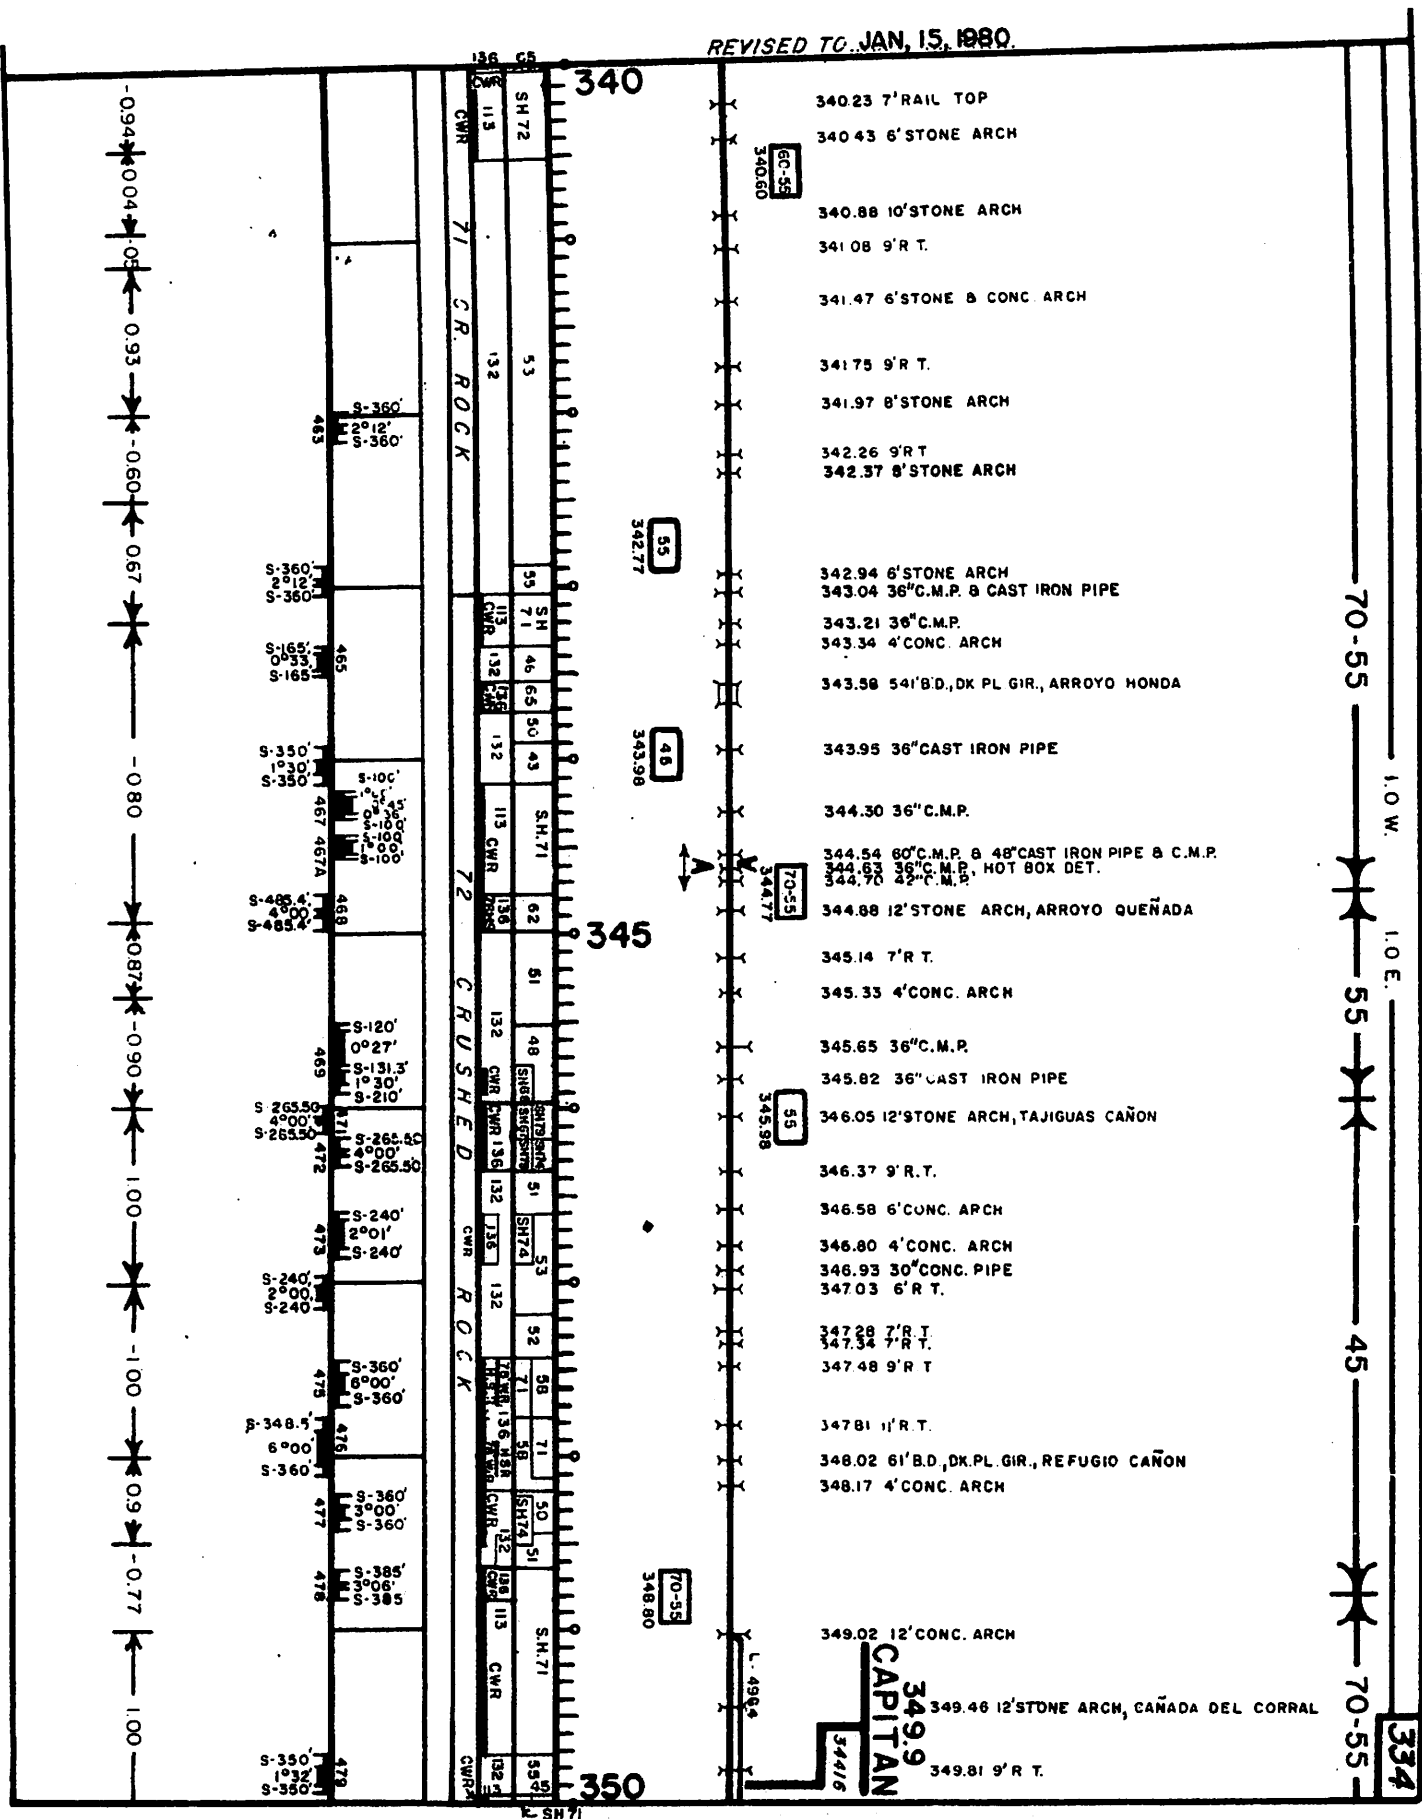



REVISED TO JAN 15, 1980

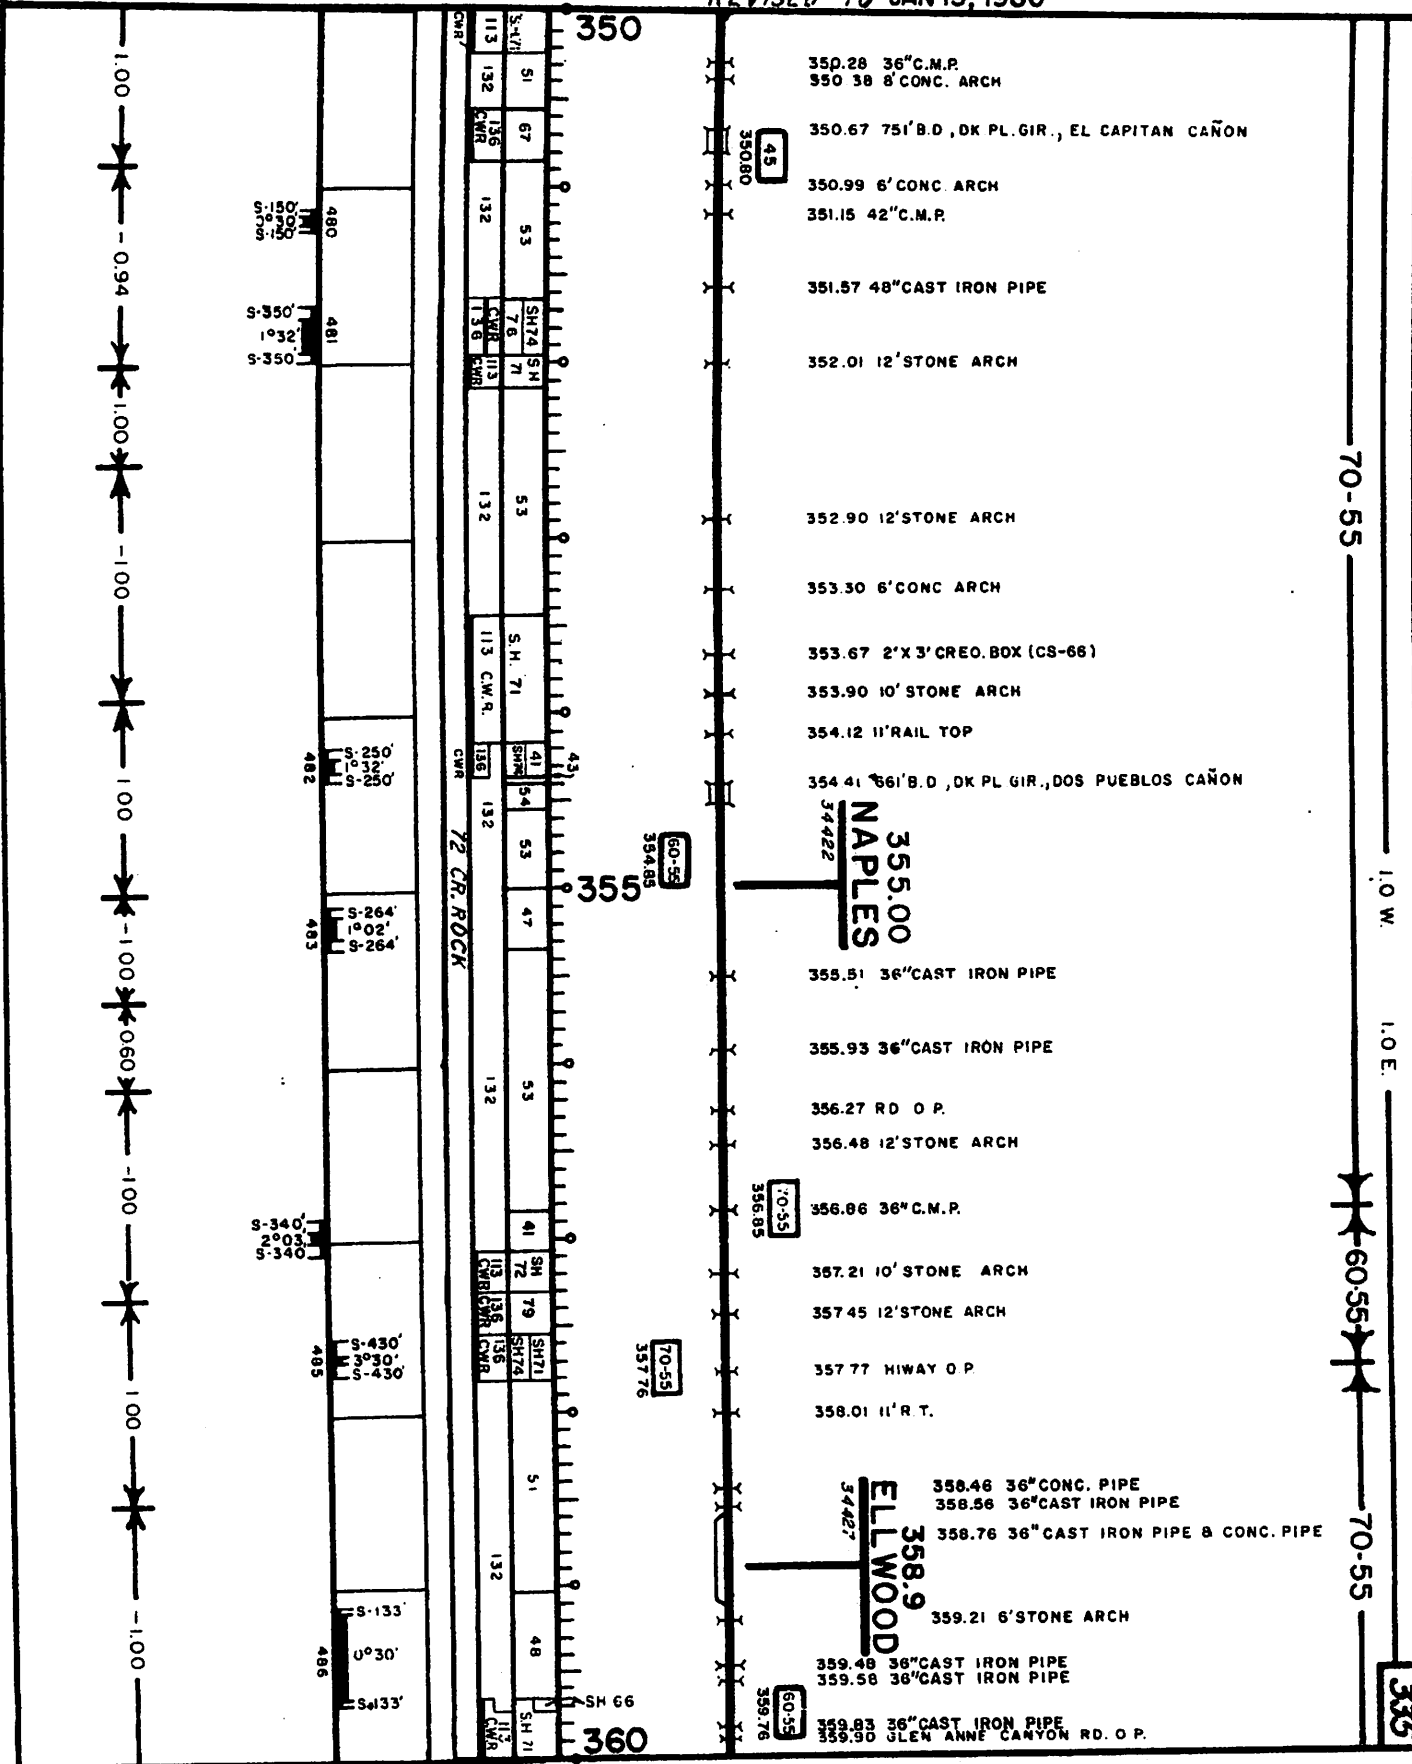

REVISED 170 JAN 15, 1980

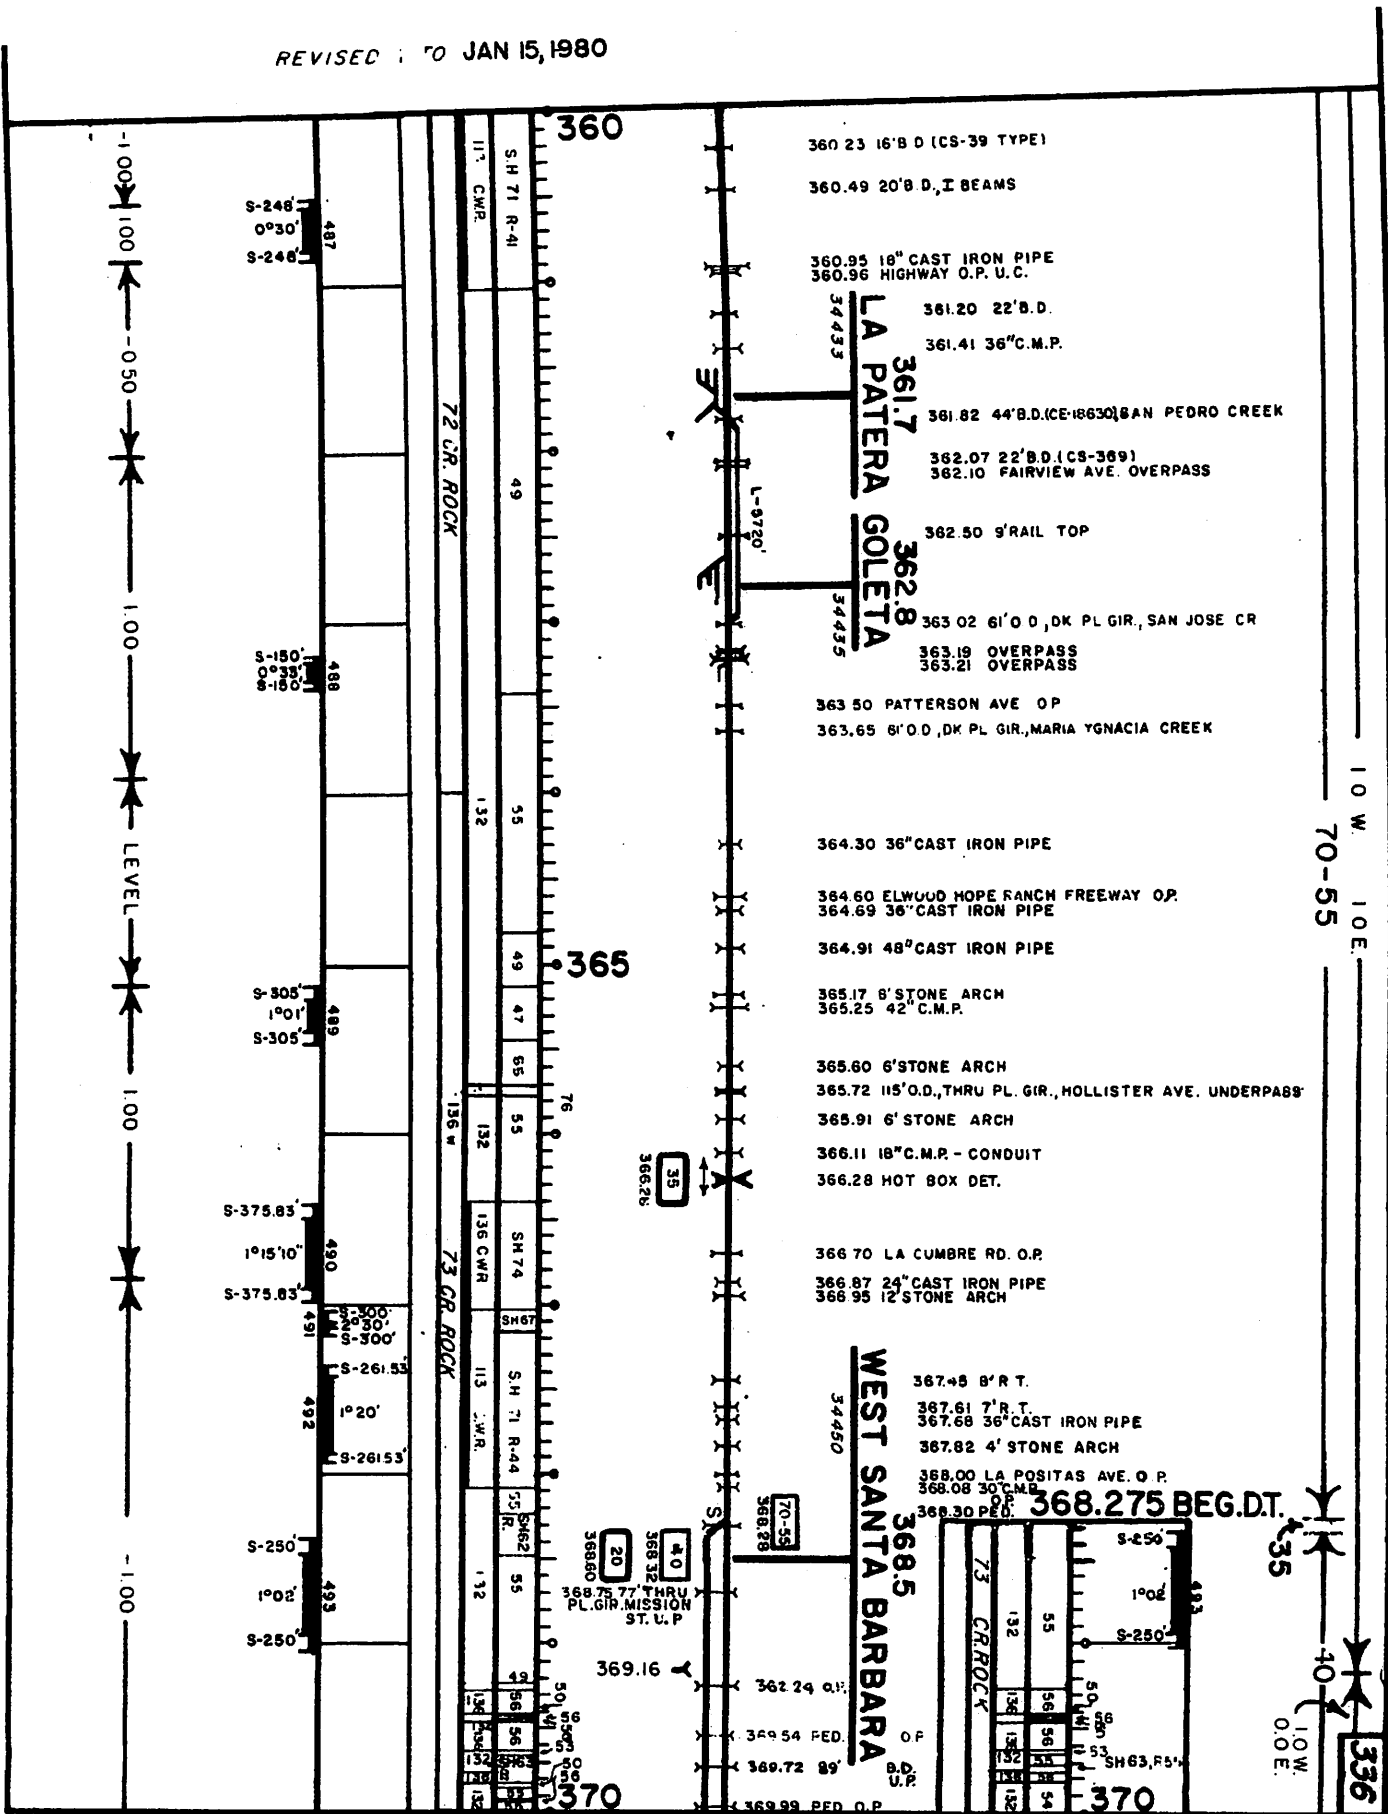

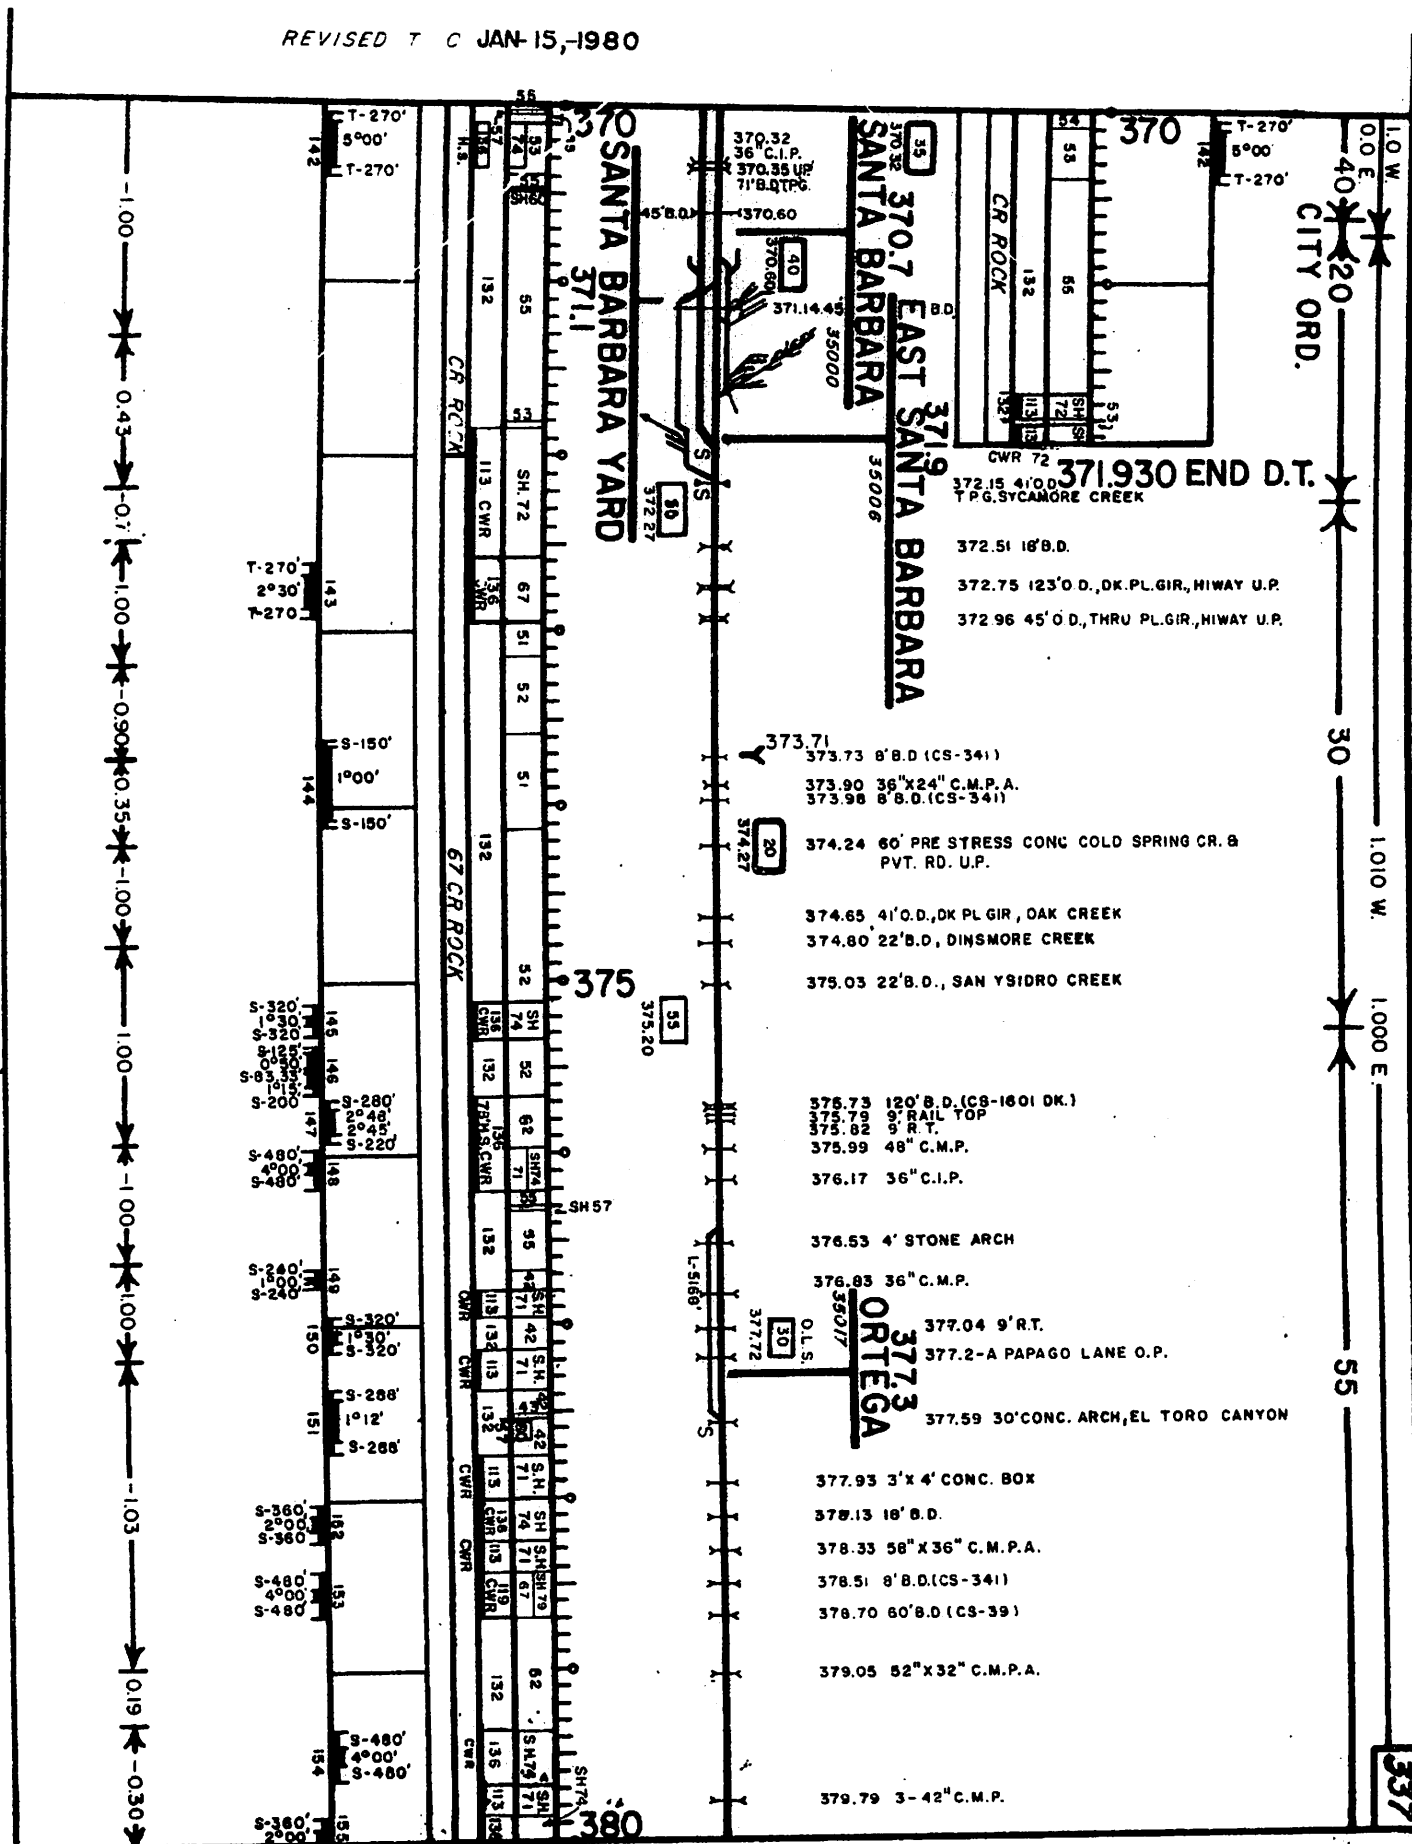

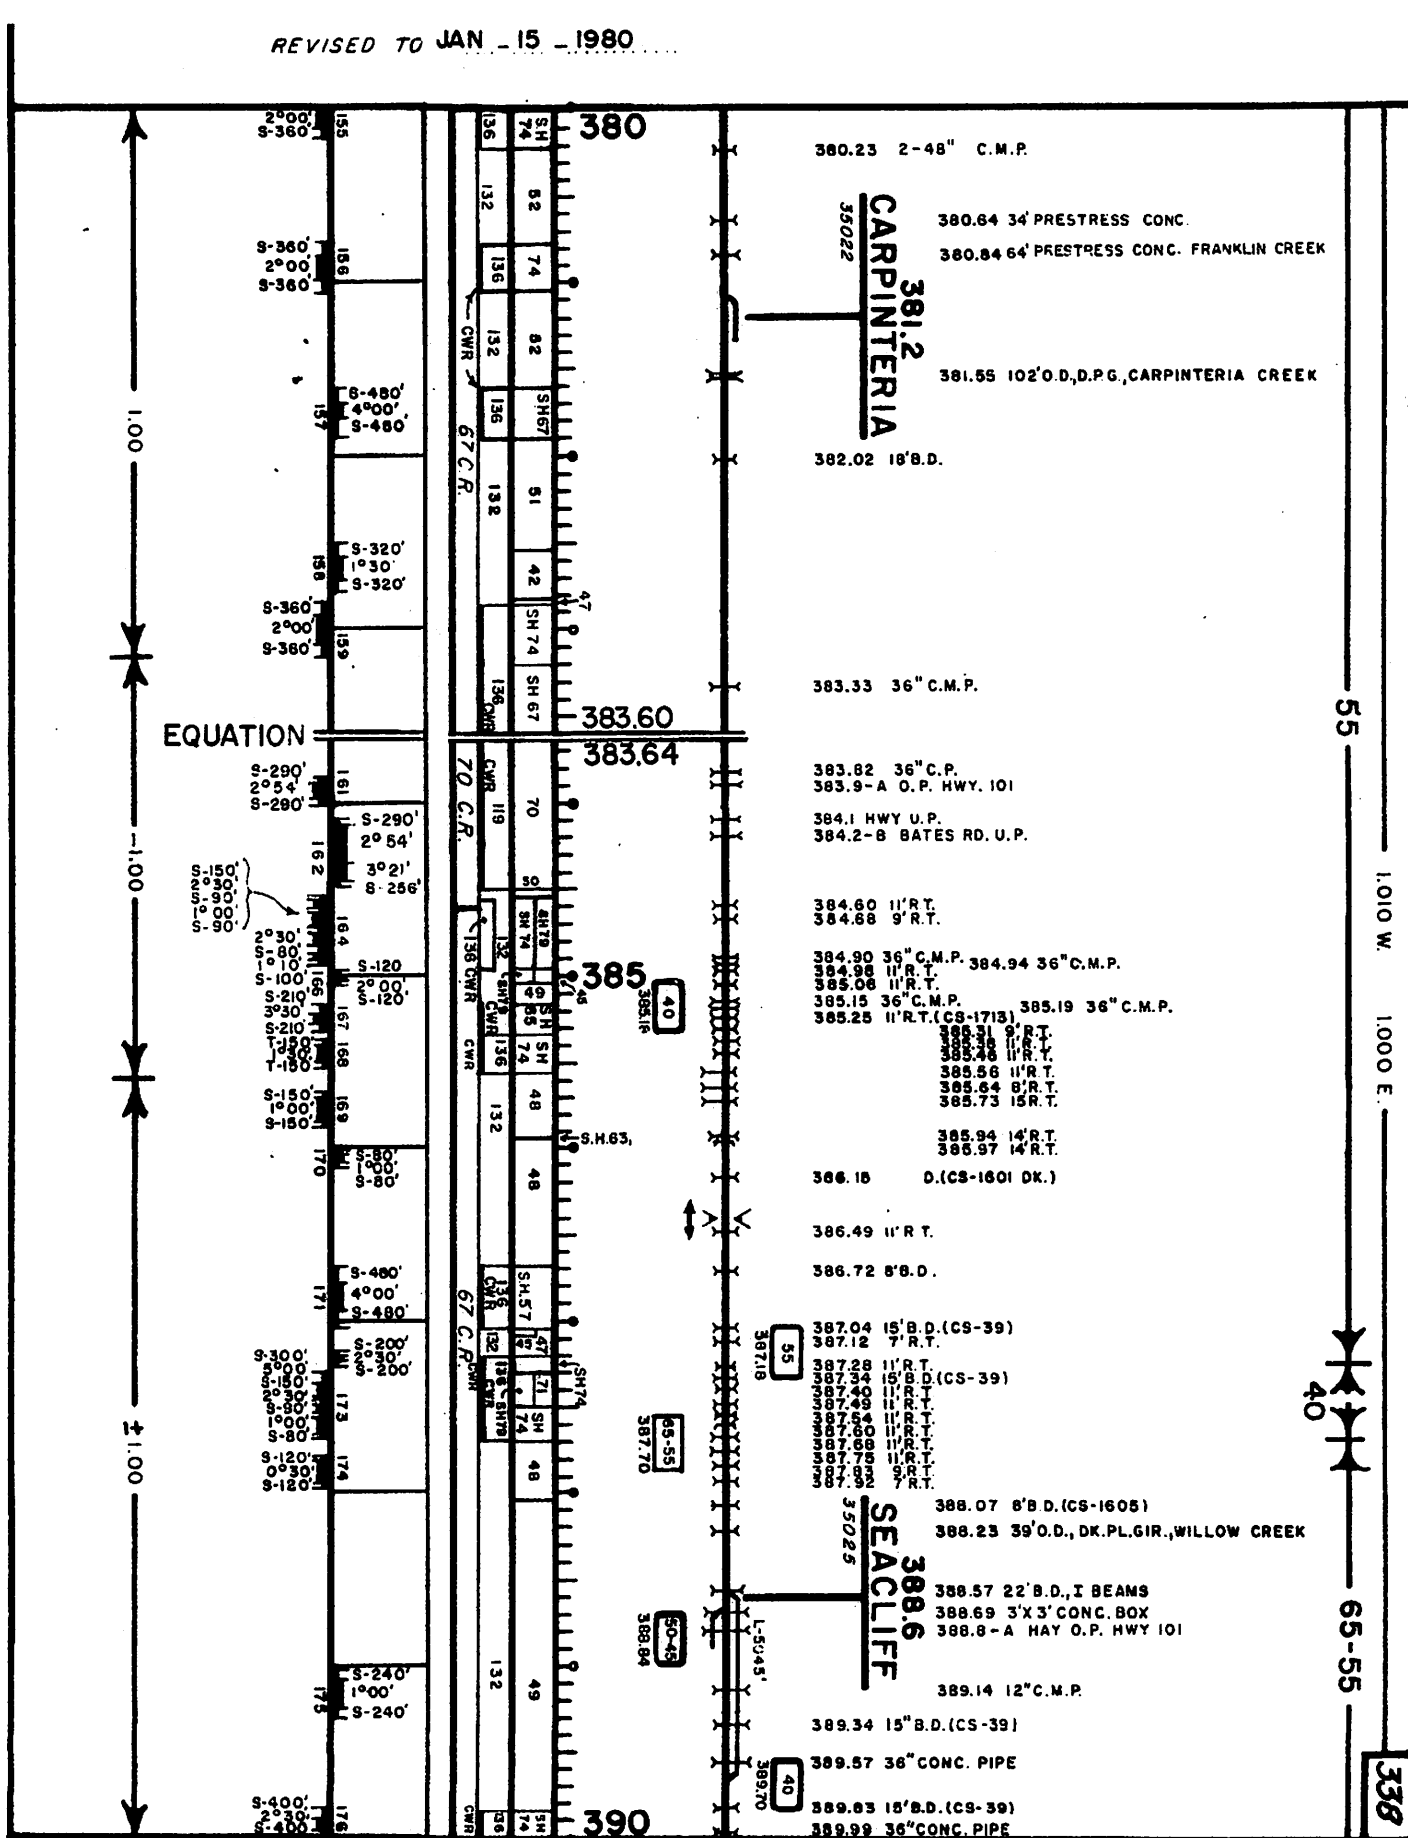

65-55-1
50-45

1.000 E

70-55

1.000 E


†

0.409 W


1.80

10

339

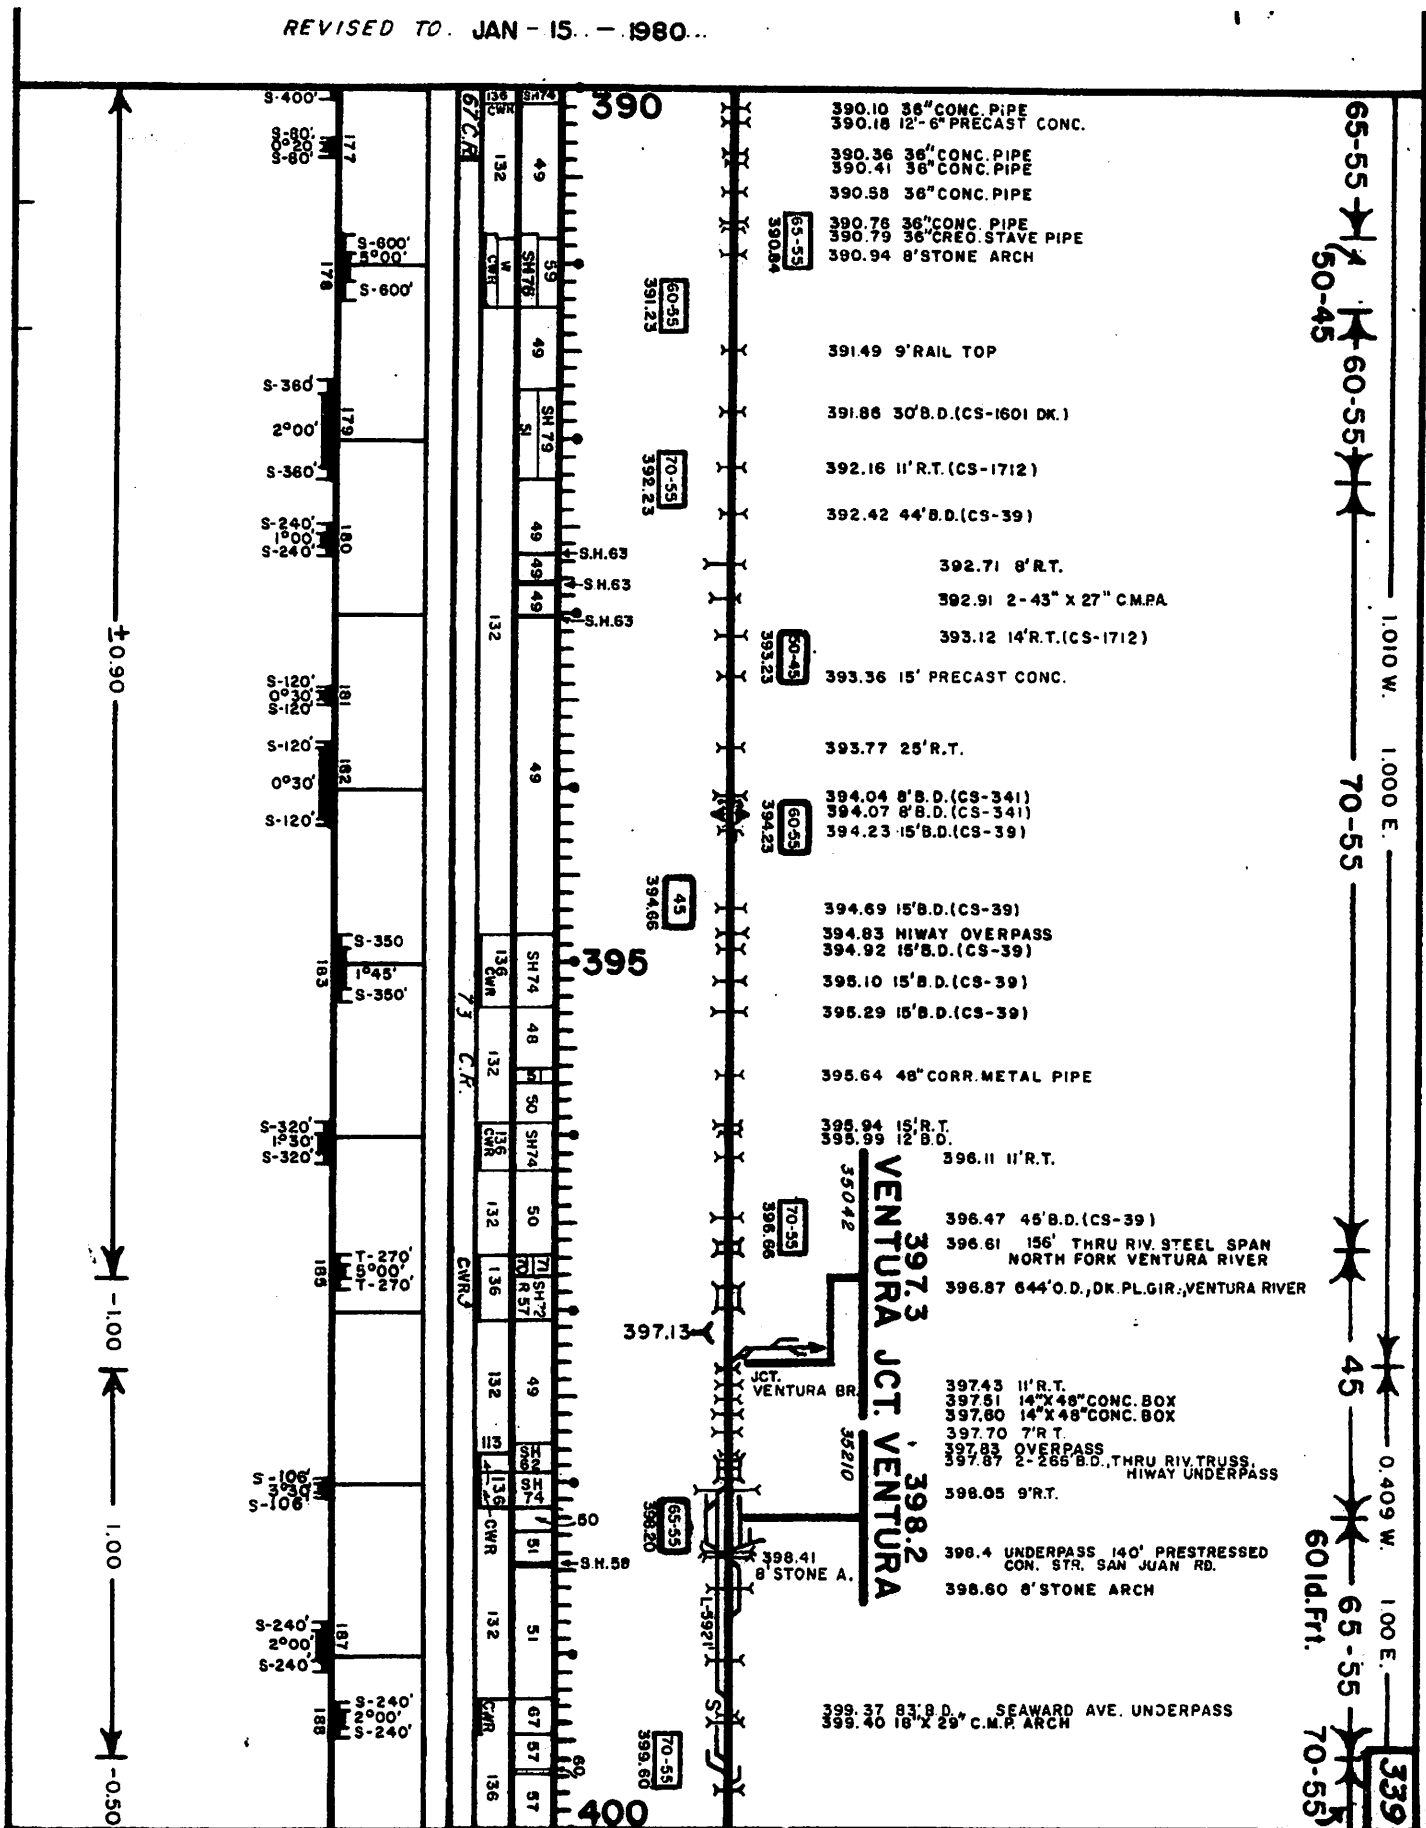


REVISED TO JAN 15 1980

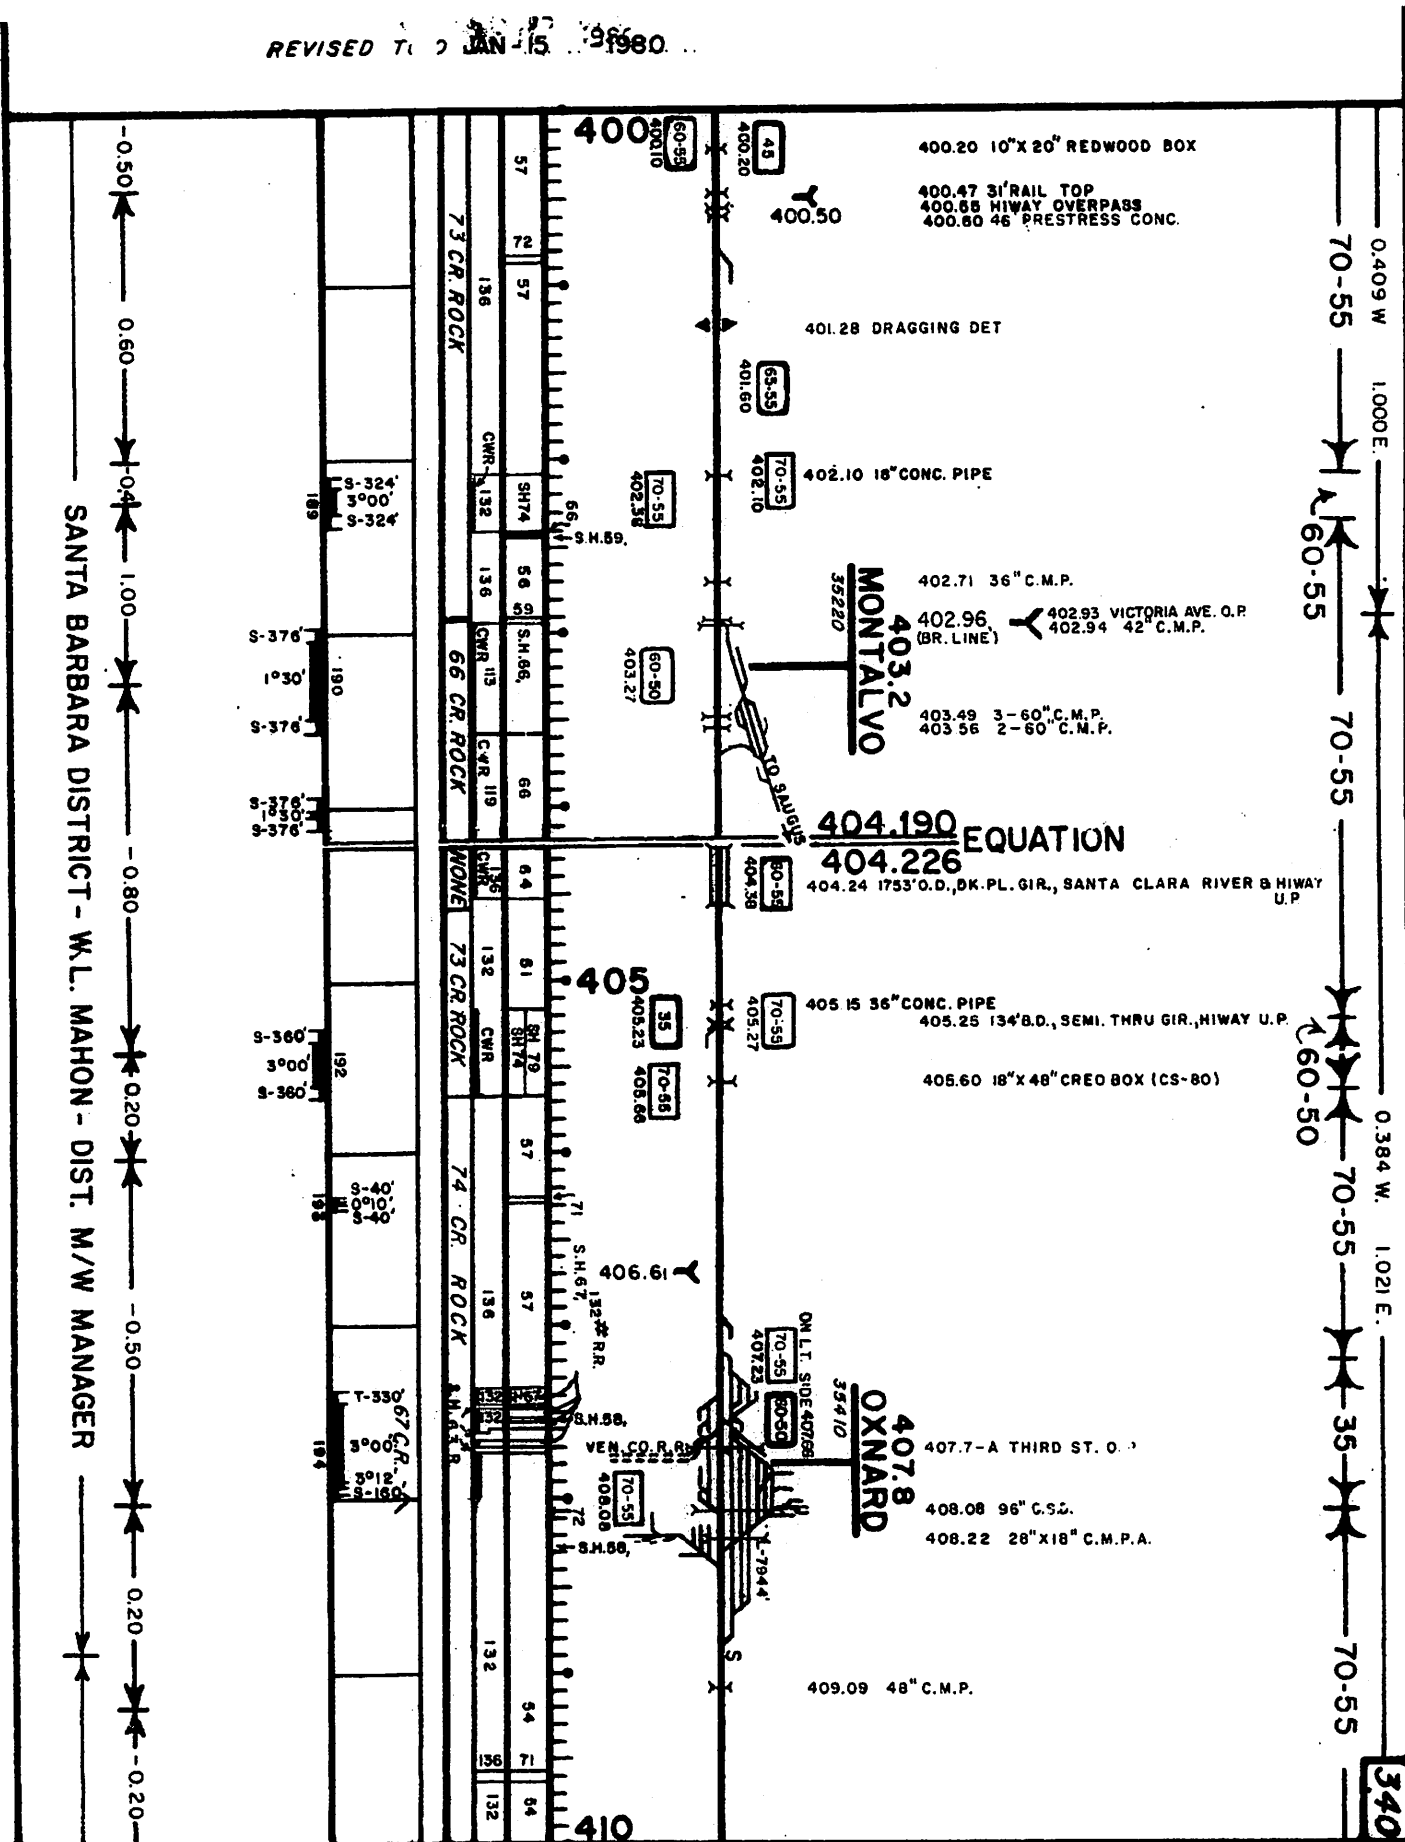

SANTA BARBARA DISTRICT - W.L. MAHON - DIST. M/W MANAGER

70-55

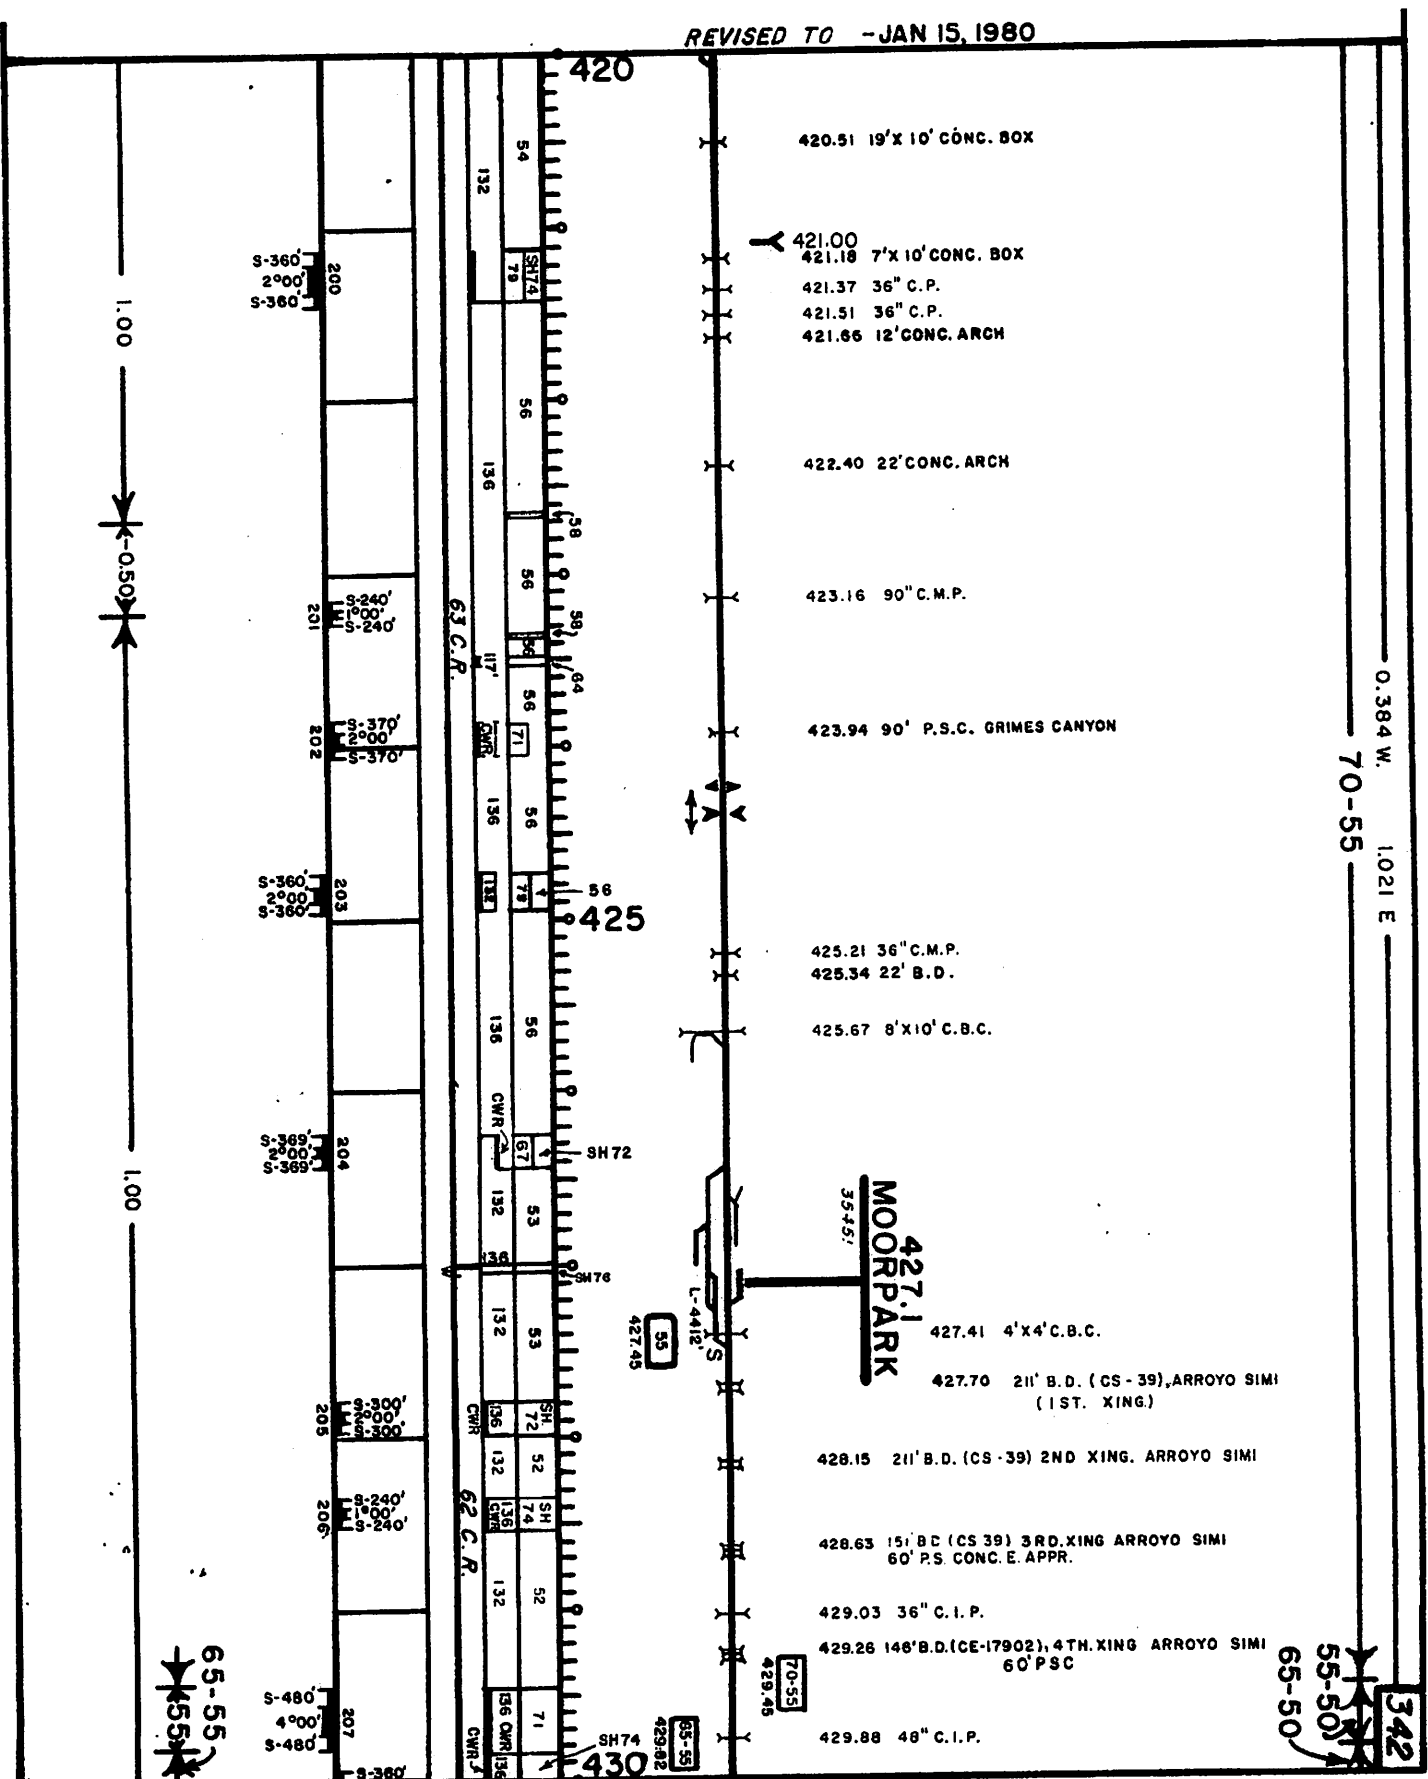

9-0-5

BURBANK DISTRICT - C.B. BURROWS - DIST. M/W MANAGER

-0.34

8-320
1°30'00"
8-320


449.24 2-25' CONC. BOXES, ALISO CREEK
449.9 RESEDA AVE. U.R.
449.9 PARTHENIA ST. U.R.

443.57 8' STONE ARCH
443.6 48" CAST IRON PIPE
443.7 DRAGGING DET.
443.77 36" CAST IRON PIPE
443.9 SANTA SUSANA RD. C. P.
92
02 TUNNEL NO. 28 (CONC.)
444.11 4' STONE ARCH
444.24 16" B.D. (CS-1601 TYPE
444.32 6' CONC. BOX


4439
NORTH RIDGE
40110

0.384 W. 1.021 E. 1.0 W. 0.00E. 1.00 W. 0.40E. 344


344

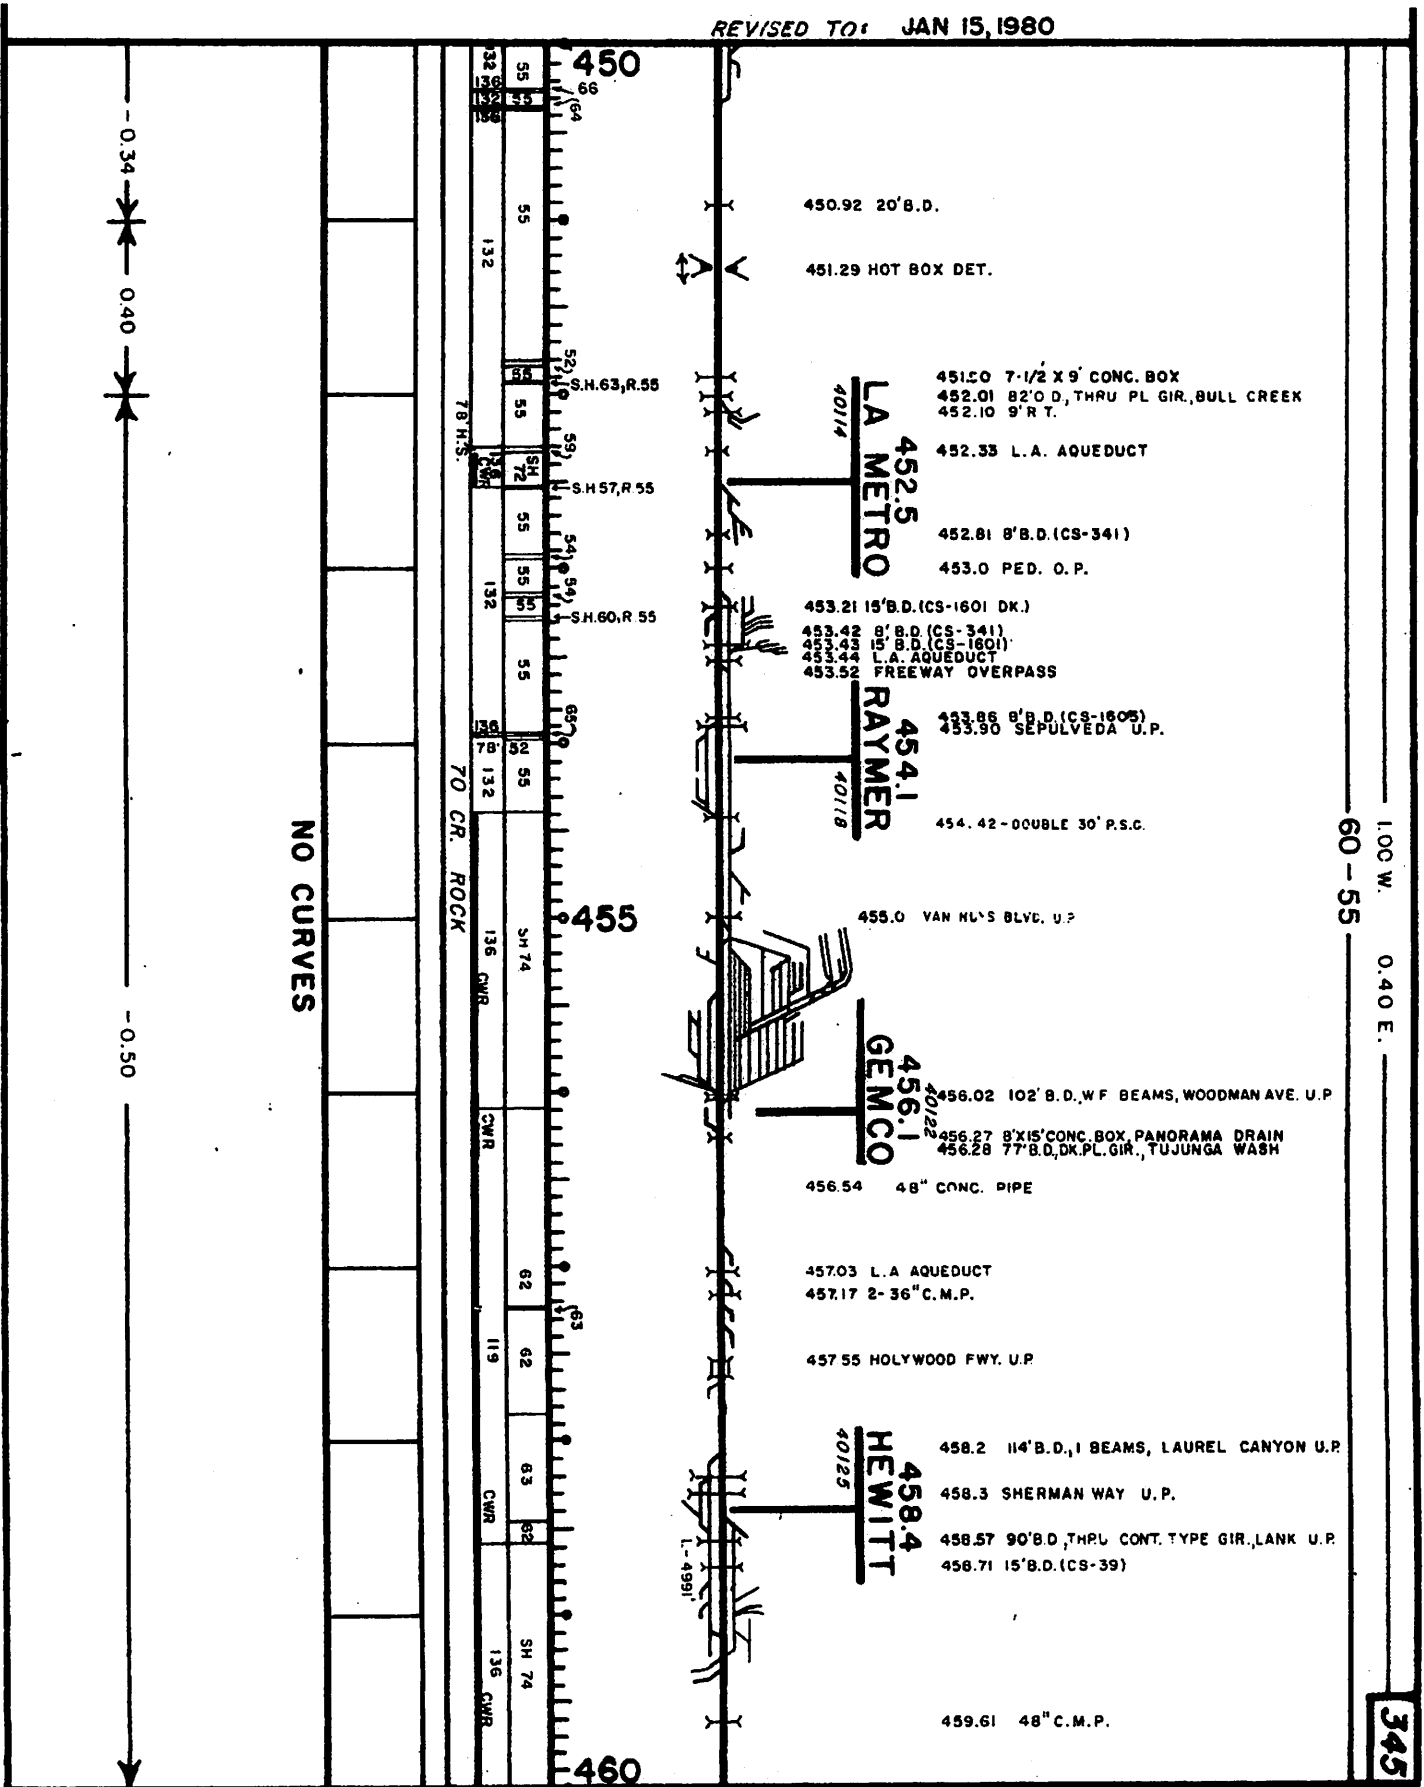

REVISED TO: JAN 15, 1980

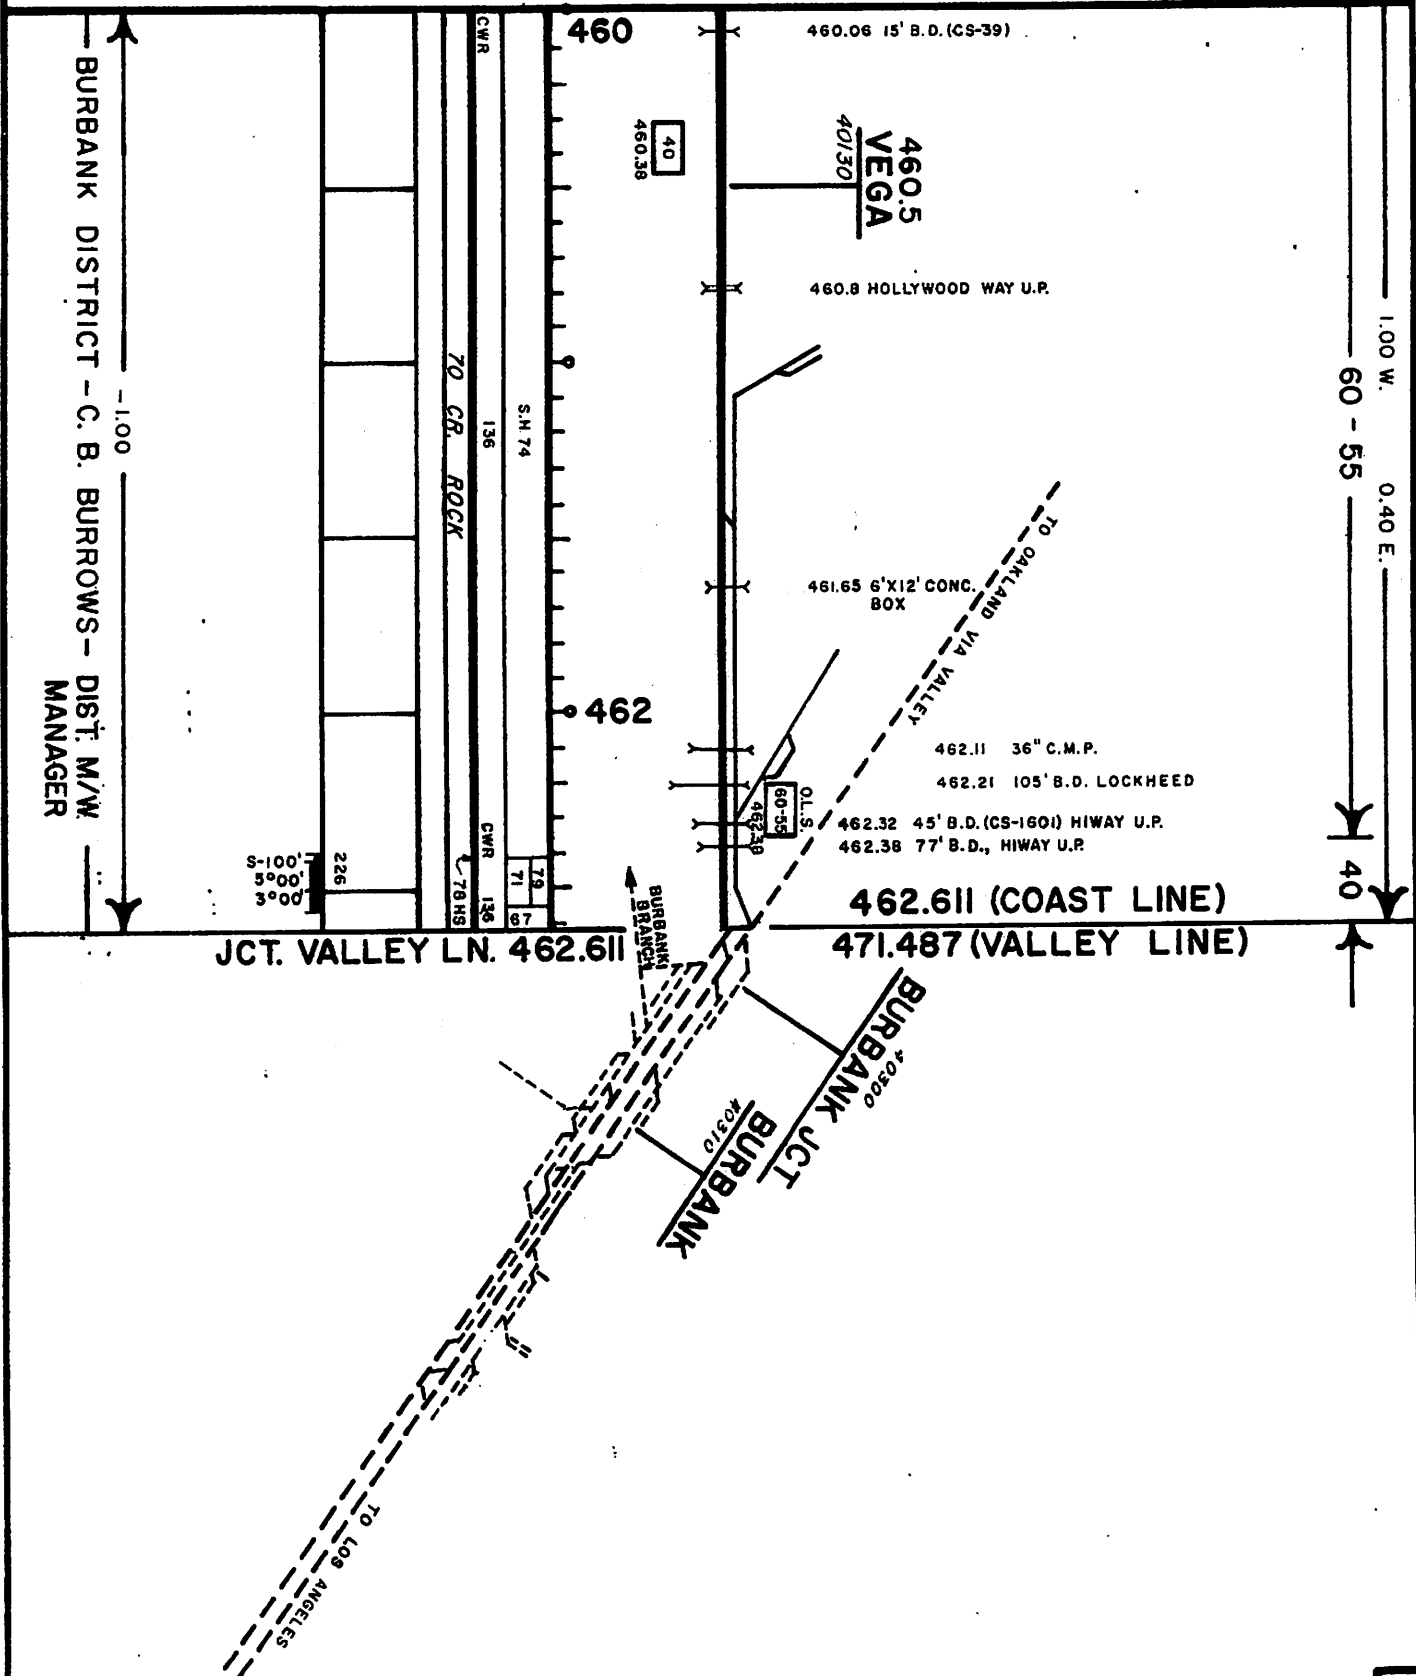

REVISED TO: JAN. 4, 1982.

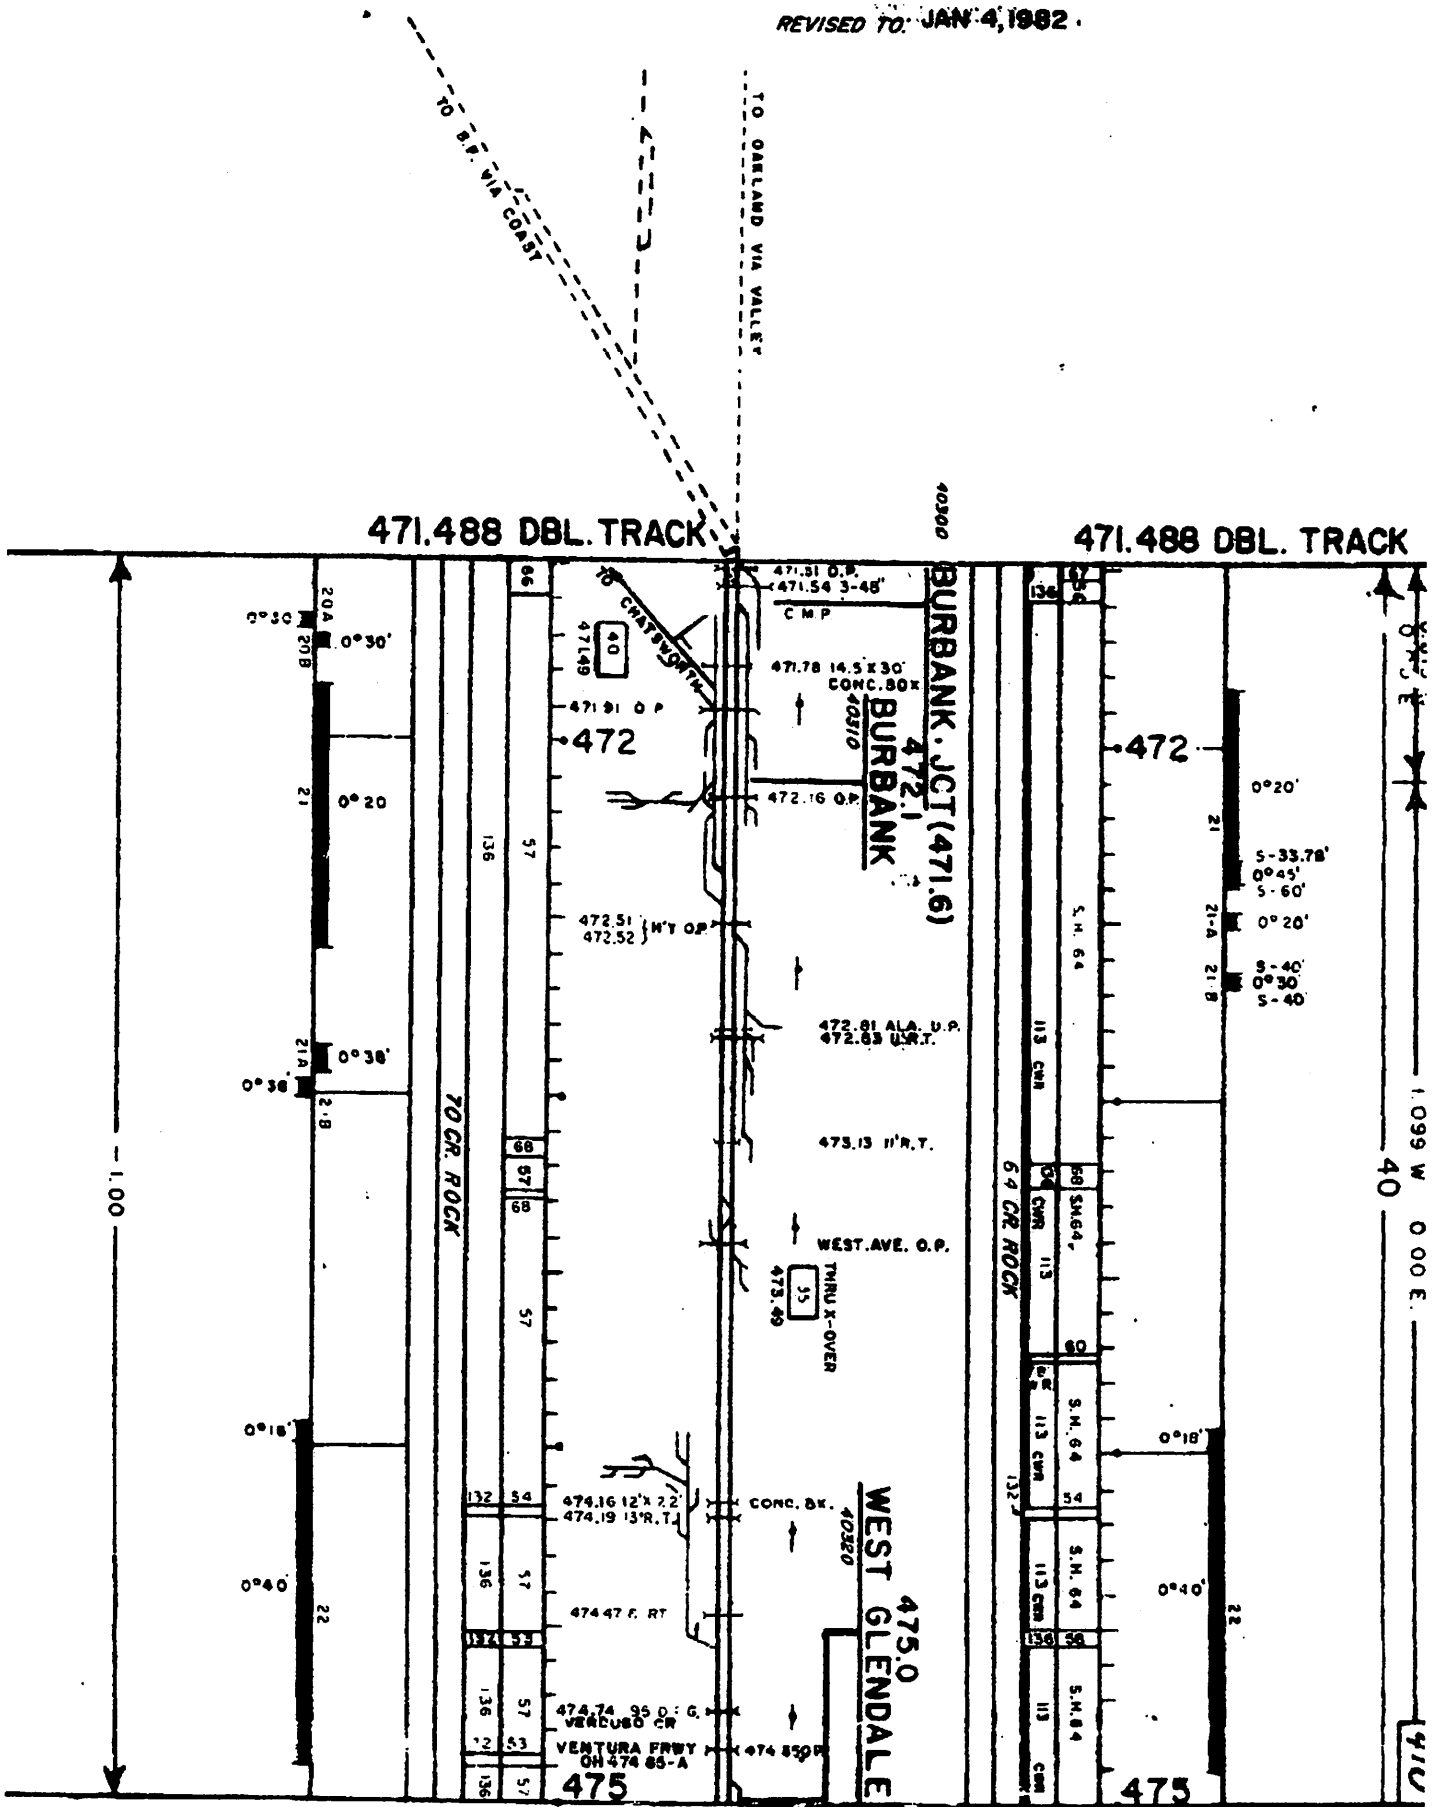

REVISED TO JAN 4, 1982

1.099 W. 0.00 E.

40

8976 W 411
0.000 E 111

475

